




U.S. DEPARTMENT OF VETERANS AFFAIRS
VETERAN BENEFITS ADMINISTRATION
STATION 201, BLDG 215, STE 200X
1ST AVENUE NORTH 22ND STREET
HINES, IL 60141
HINES FINANCE CENTER

VA PROJECT NUMBER: 201VB3032
100% DESIGN



PROJECT LOCATION
EDWARD HINES, JR. VA MEDICAL CENTER CAMPUS

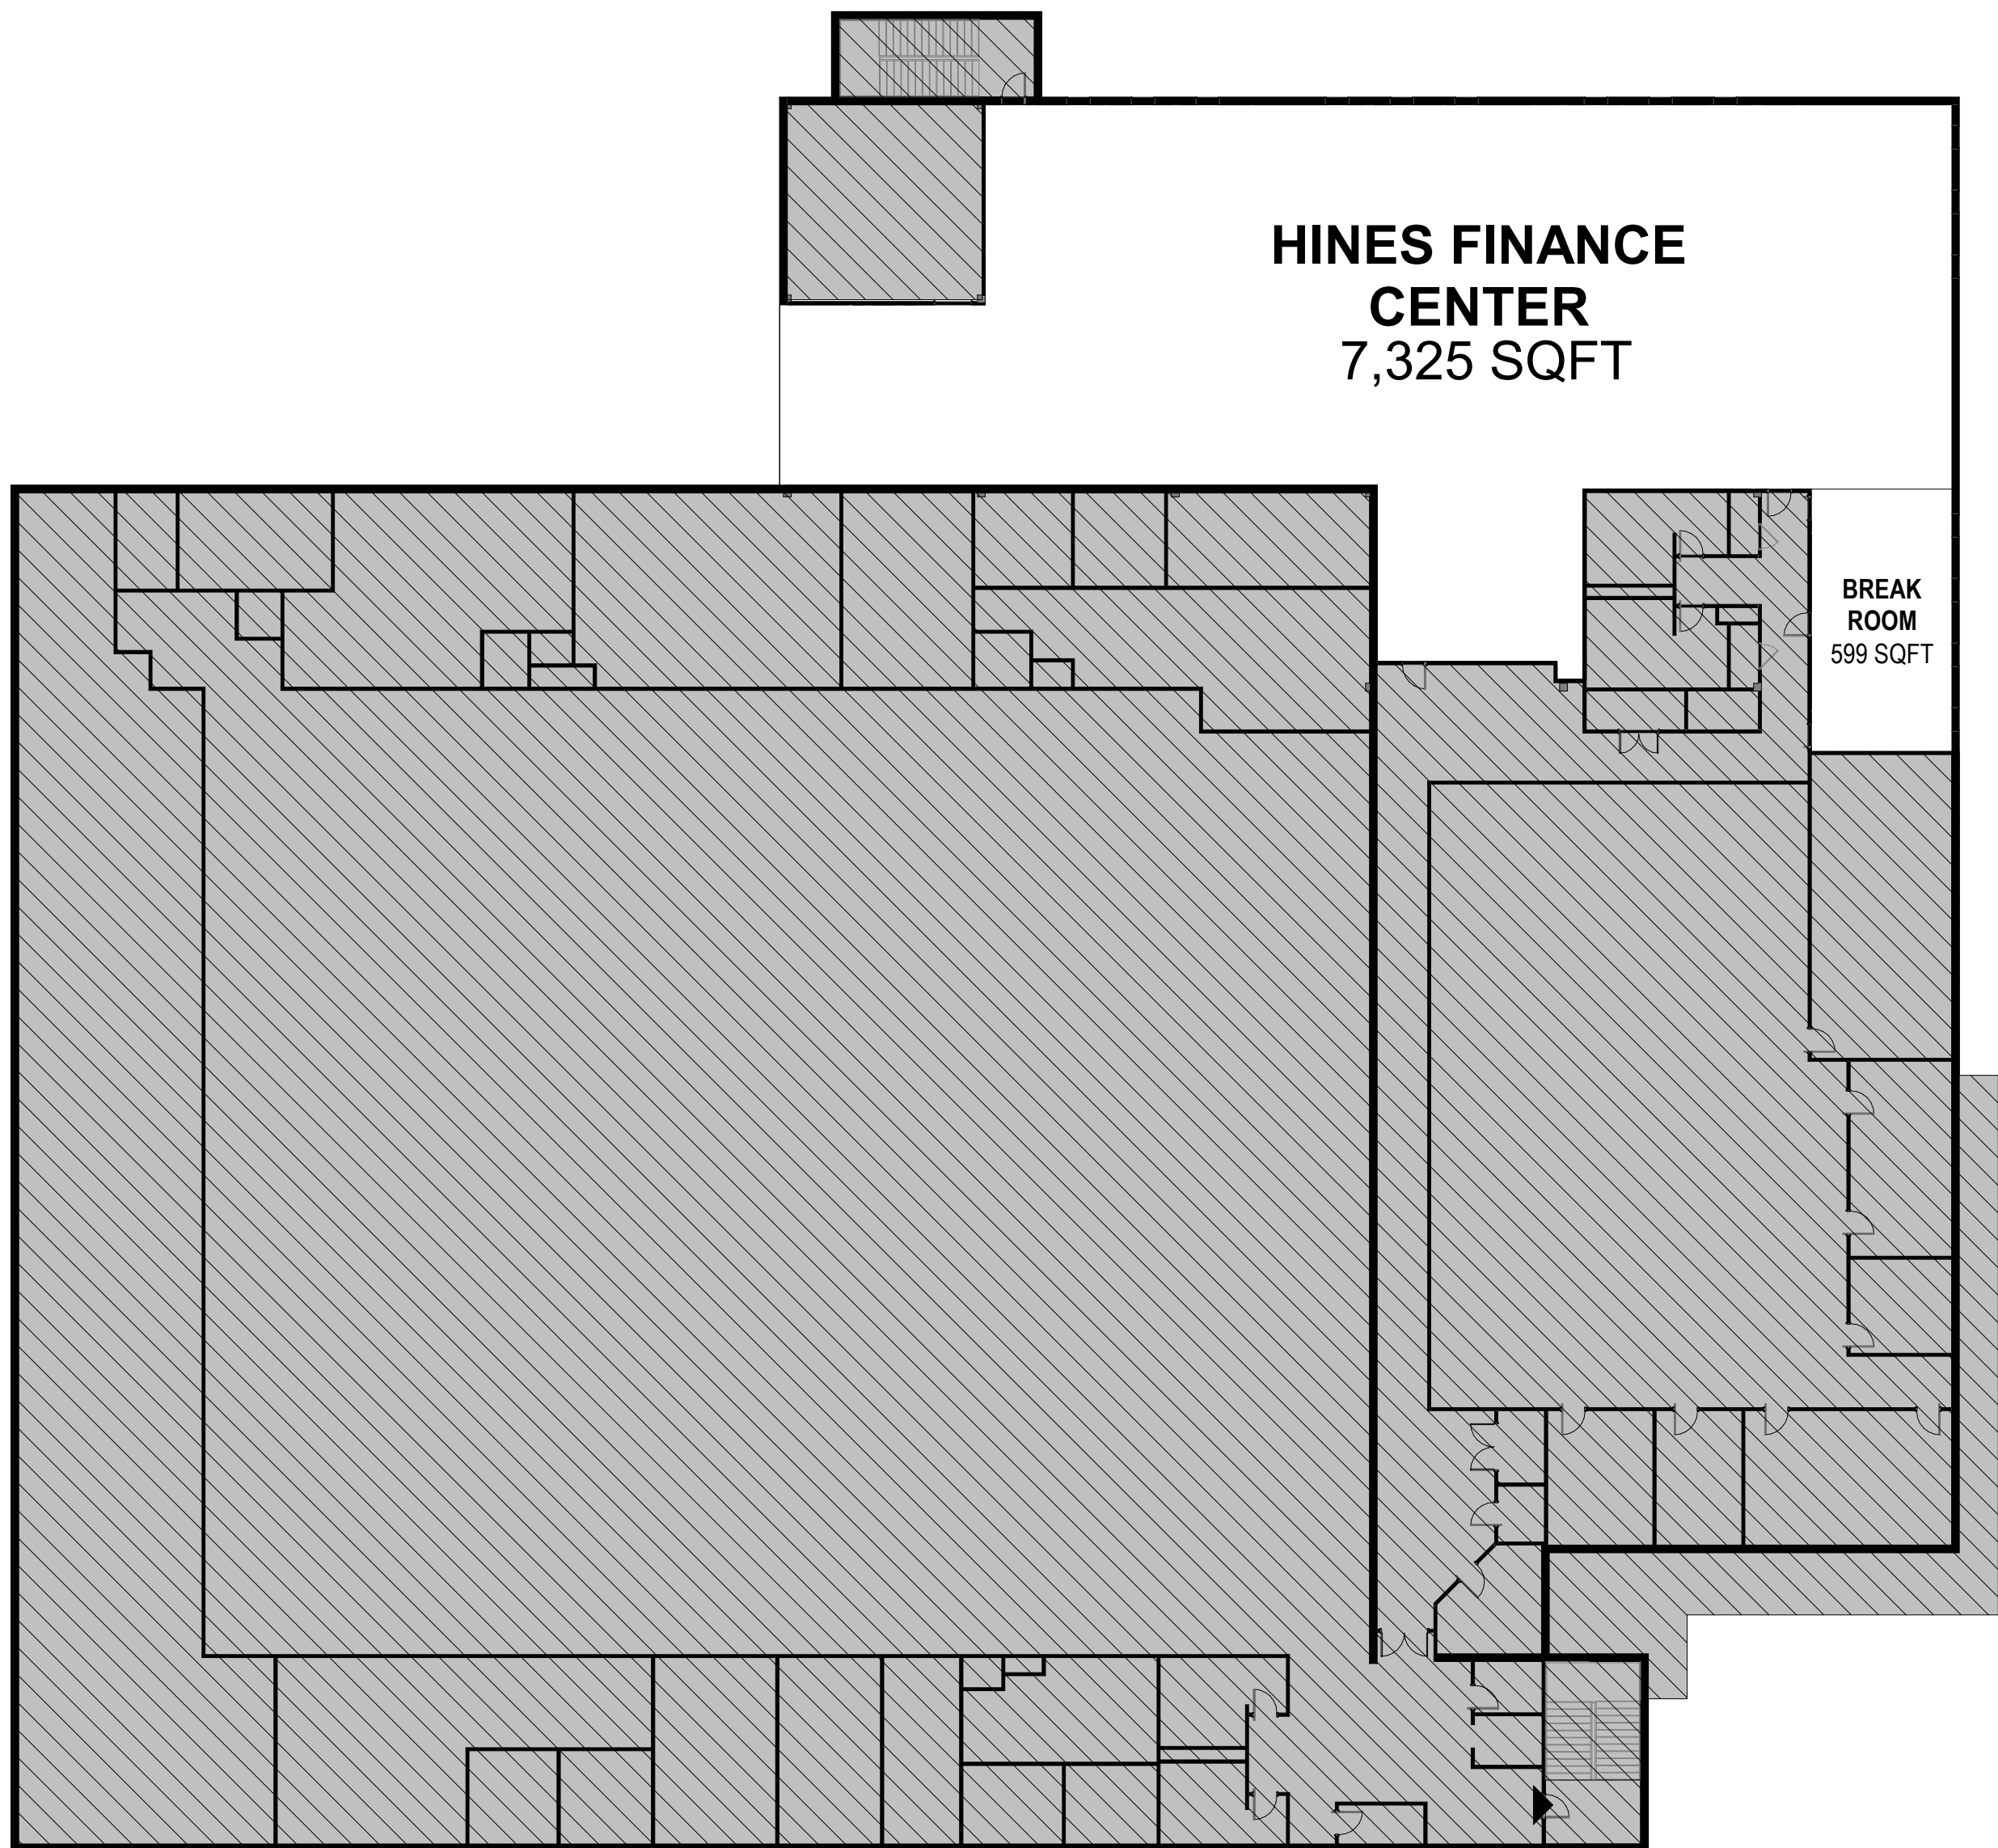

PROJECT SCOPE AREA
BUILDING 215 - LEVEL 2

SHEET INDEX		
SEQ	NUMBER	SHEET NAME
[01] GENERAL		
1	GI-000	COVER SHEET
2	GI-001	GENERAL INFORMATION
3	GI-011	LEVEL 2 - LIFE SAFETY PLAN
[02] ARCHITECTURAL		
4	AD-100	LEVEL 2 - DEMOLITION FLOOR PLAN
5	AD-200	LEVEL 2 - DEMOLITION REFLECTED CEILING PLAN
6	AE-100	LEVEL 2 - FLOOR PLAN - DIMENSION PLAN
7	AE-101	LEVEL 2 - FLOOR PLAN - FF&E
8	AE-102	LEVEL 2 - FLOOR PLAN - FLOOR FINISH
9	AE-200	LEVEL 2 - REFLECTED CEILING PLAN
10	AE-300	INTERIOR ELEVATIONS
11	AE-301	ARCHITECTURAL DETAILS
[03] FIRE PROTECTION		
12	FP-100	LEVEL 2 - FIRE PROTECTION PLAN
[04] MECHANICAL		
13	MP-000	MECHANICAL AND PLUMBING LEGEND AND ABBREVIATIONS
14	MD-101	LEVEL 2 - MECHANICAL HVAC DEMOLITION PLAN
15	MH-100	LEVEL 2 - MECHANICAL HVAC ZONING PLAN
16	MH-101	LEVEL 2 - MECHANICAL HVAC DUCT PLAN AND SCHEDULES
17	MH-102	LEVEL 2 - MECHANICAL HVAC PIPING PLAN
18	MH-200	MECHANICAL DETAILS
19	MH-300	MECHANICAL CONTROLS
[05] PLUMBING		
20	P-100	LEVEL 2 - BREAK ROOM PLUMBING ENLARGED PLAN
[06] ELECTRICAL		
21	E-000	ELECTRICAL LEGEND AND ABBREVIATIONS
22	EPD-101	LEVEL 2 - ELECTRICAL POWER DEMOLITION PLAN
23	EPD-102	LEVEL 2 - ELECTRICAL LIGHTING DEMOLITION PLAN
24	EP-101	LEVEL 2 - ELECTRICAL POWER PLAN
25	EP-102	LEVEL 2 - ELECTRICAL LIGHTING PLAN
26	EP-103	LEVEL 2 - ELECTRICAL DATA AND SECURITY PLAN
27	EP-300	ELECTRICAL ONE-LINE DIAGRAM AND DETAILS
28	EP-301	EXISTING PANEL SCHEDULES
29	EP-302	NEW PANEL SCHEDULES

TOTAL SHEETS: 29

FULLY SPRINKLERED
100% DESIGN

<table><tr><th>No.</th><th>REVISION DESCRIPTION</th><th>DATE</th></tr><tr><td> </td><td> </td><td> </td></tr><tr><td> </td><td> </td><td> </td></tr><tr><td> </td><td> </td><td> </td></tr></table>	No.	REVISION DESCRIPTION	DATE										ARCHITECT / ENGINEER:			STAMP: 	Drawing Title COVER SHEET		Project Title HINES FINANCE CENTER		Project Number 201VB3032		Veterans Benefits Administration
No.	REVISION DESCRIPTION	DATE																					
					VA Health Care System Approval:		Location STATION 201, BLDG 215, STE 200X 1ST AVENUE NORTH 22ND STREET HINES, IL 60141		GI-000														
SPUR SBBL COLLABORATIVE JV, INC 100 N. STONE AVENUE, STE 1102 TUCSON, AZ 85701 (405) 842-6100 IL ARCH. LICENSE NO.: 001023503 EXP. 11/30/22 IL MECH. ENGR. LICENSE NO.: 062.071715 EXP. 11/30/21 IL ELEC. ENGR. LICENSE NO.: 062.072296 EXP. 11/30/21					MECH / ELEC / PLUMB / TECH ENGINEER SPUR DESIGN 11020 KING STREET, SUITE 350 OVERLAND PARK, KS 66210 (913) 369-7200		Date 06/14/2021	Checked TAB	Drawn JET														
									Drawing # 1 OF 29														

6/10/2021 3:44:46 PM


GENERAL DEMOLITION NOTES

1. ALL EXISTING WALL DIMENSIONS ARE TO FINISH FACE, UNLESS OTHERWISE NOTED
2. THE CONTRACTOR SHALL VERIFY DIMENSIONS OF AS-BUILT CONDITIONS, AND NOTIFY THE ARCHITECT IN WRITING OF ANY DISCREPANCIES. ALL INFORMATION SHOWN ON THE CONSTRUCTION DOCUMENTS IS BASED ON FIELD OBSERVATIONS AND/OR THE ORIGINAL CONSTRUCTION DOCUMENTS OF THE FACILITY.
3. USE CONSTRUCTION BARRIERS AS REQUIRED TO MITIGATE DUST AND DEBRIS THROUGHOUT DEMOLITION AND CONSTRUCTION. DO NOT REMOVE BARRIERS FROM WORK AREA UNTIL COMPLETED PROJECT AREA HAS BEEN INSPECTED BY THE SAFETY OFFICER.
4. THE CONTRACTOR SHALL PROVIDE PROTECTIVE COVERINGS TO PROTECT EXISTING FLOOR, WALL AND CEILING FINISHES IN EXISTING AREAS NOT DESIGNATED FOR DEMOLITION OR NEW CONSTRUCTION. THE CONTRACTOR SHALL BE RESPONSIBLE FOR THE REPAIR OF ANY DAMAGE CAUSED BY HIS WORK OR ANY SUBCONTRACTOR.
5. THE CONTRACTOR SHALL VERIFY THAT NEW MECHANICAL SYSTEMS CAN BE INSTALLED IN EXISTING SPACES TO CLEAR EXISTING CEILING AND OTHER CONSTRUCTED ITEMS AND MAINTAIN FLOOR TO CEILING HEIGHTS INDICATED ON DRAWINGS. IF DISCREPANCIES OCCUR DUE TO EXISTING CONDITIONS, CONSULT WITH THE ARCHITECT BEFORE PROCEEDING.
6. THE FINISH FACE OF MATERIAL OF NEW PARTITIONS SHALL ALIGN ON BOTH SIDES OF THE PARTITION WITH THE FACE OF THE MATERIALS ON EXISTING COLUMNS, WALLS, OR PARTITIONS, UNLESS NOTED OTHERWISE.
7. NO WORK TO BE DONE IN AREAS HATCHED GRAY IN PLANS, HOWEVER WORK MIGHT NEED TO BE PERFORMED IN CEILING OR EXISTING CHASES THROUGHOUT BUILDING. REFERENCE MECHANICAL AND ELECTRICAL DRAWINGS FOR EXTENT OF WORK. COORDINATE ACCESS TO ROOMS OUTSIDE OF SCOPE WITH OWNER.
8. CAREFULLY REMOVE AND RETAIN ANY EXISTING ARTWORK AND RETURN TO OWNER FOR REINSTALLATION.
9. SPRINKLER CONTRACTOR IS RESPONSIBLE FOR FIELD VERIFYING THE OPERATION, LOCATION AND ROUTING OF THE EXISTING SPRINKLER SYSTEM, INCLUDING RELATED PIPING SYSTEMS, COMPONENTS, SPRINKLERS AND ACCESSORIES PRIOR TO START OF PROJECT.
10. EXISTING SPRINKLER SYSTEMS TO BE MODIFIED TO CONFORM TO THE NEW LAYOUT. ALL EXISTING SPRINKLERS, REMOVED OR DISTURBED IN RENOVATION AREAS, SHALL BE DISPOSED OF AND REPLACED WITH NEW SPRINKLERS.

DEMOLITION FLOOR PLAN LEGEND

	AREA IS NOT IN CONTRACT
	EXISTING WALLS TO REMAIN
	EXISTING WALLS TO BE DEMOLISHED
	EXISTING DOOR AND FRAME TO REMAIN
	EXISTING DOOR AND FRAME TO BE DEMOLISHED
	KEYNOTE: REFERENCE KEYNOTE LEGEND

DEMOLITION KEYNOTE LEGEND	
2.02	REMOVE EXISTING WALL AS REQUIRED FOR NEW CONSTRUCTION
2.03	REMOVE EXISTING DOOR AND FRAME
2.04	REMOVE EXISTING ACCESS FLOORING SYSTEM AND PREP EXISTING FLOOR SURFACE FOR NEW ACCESS FLOORING SYSTEM
2.05	REMOVE EXISTING WALL BASE AND FINISHES, PREP WALL SURFACE FOR NEW WALL BASE AND FINISHES
2.07	REMOVE DOOR AND RETAIN, REMOVE AND PROTECT GLASS WITH ETCHED SEAL LOGO TO BE REINSTALLED IN WINDOW AS PART OF THE RENOVATION DESIGN.
2.08	REMOVE EXISTING STORAGE CABINETS AND RETAIN FOR REUSE IN RENOVATION DESIGN.
2.09	REMOVE EXISTING WORKSTATIONS IN ENTIRETY.
2.10	REMOVE AND RETAIN PRINTER FOR REUSE IN RENOVATION DESIGN.
2.11	REMOVE AND RETAIN BIN FOR REUSE IN RENOVATION DESIGN.
2.12	REMOVE AND RETAIN ALL ARTWORK AND RETURN TO OWNER FOR REINSTALLATION.

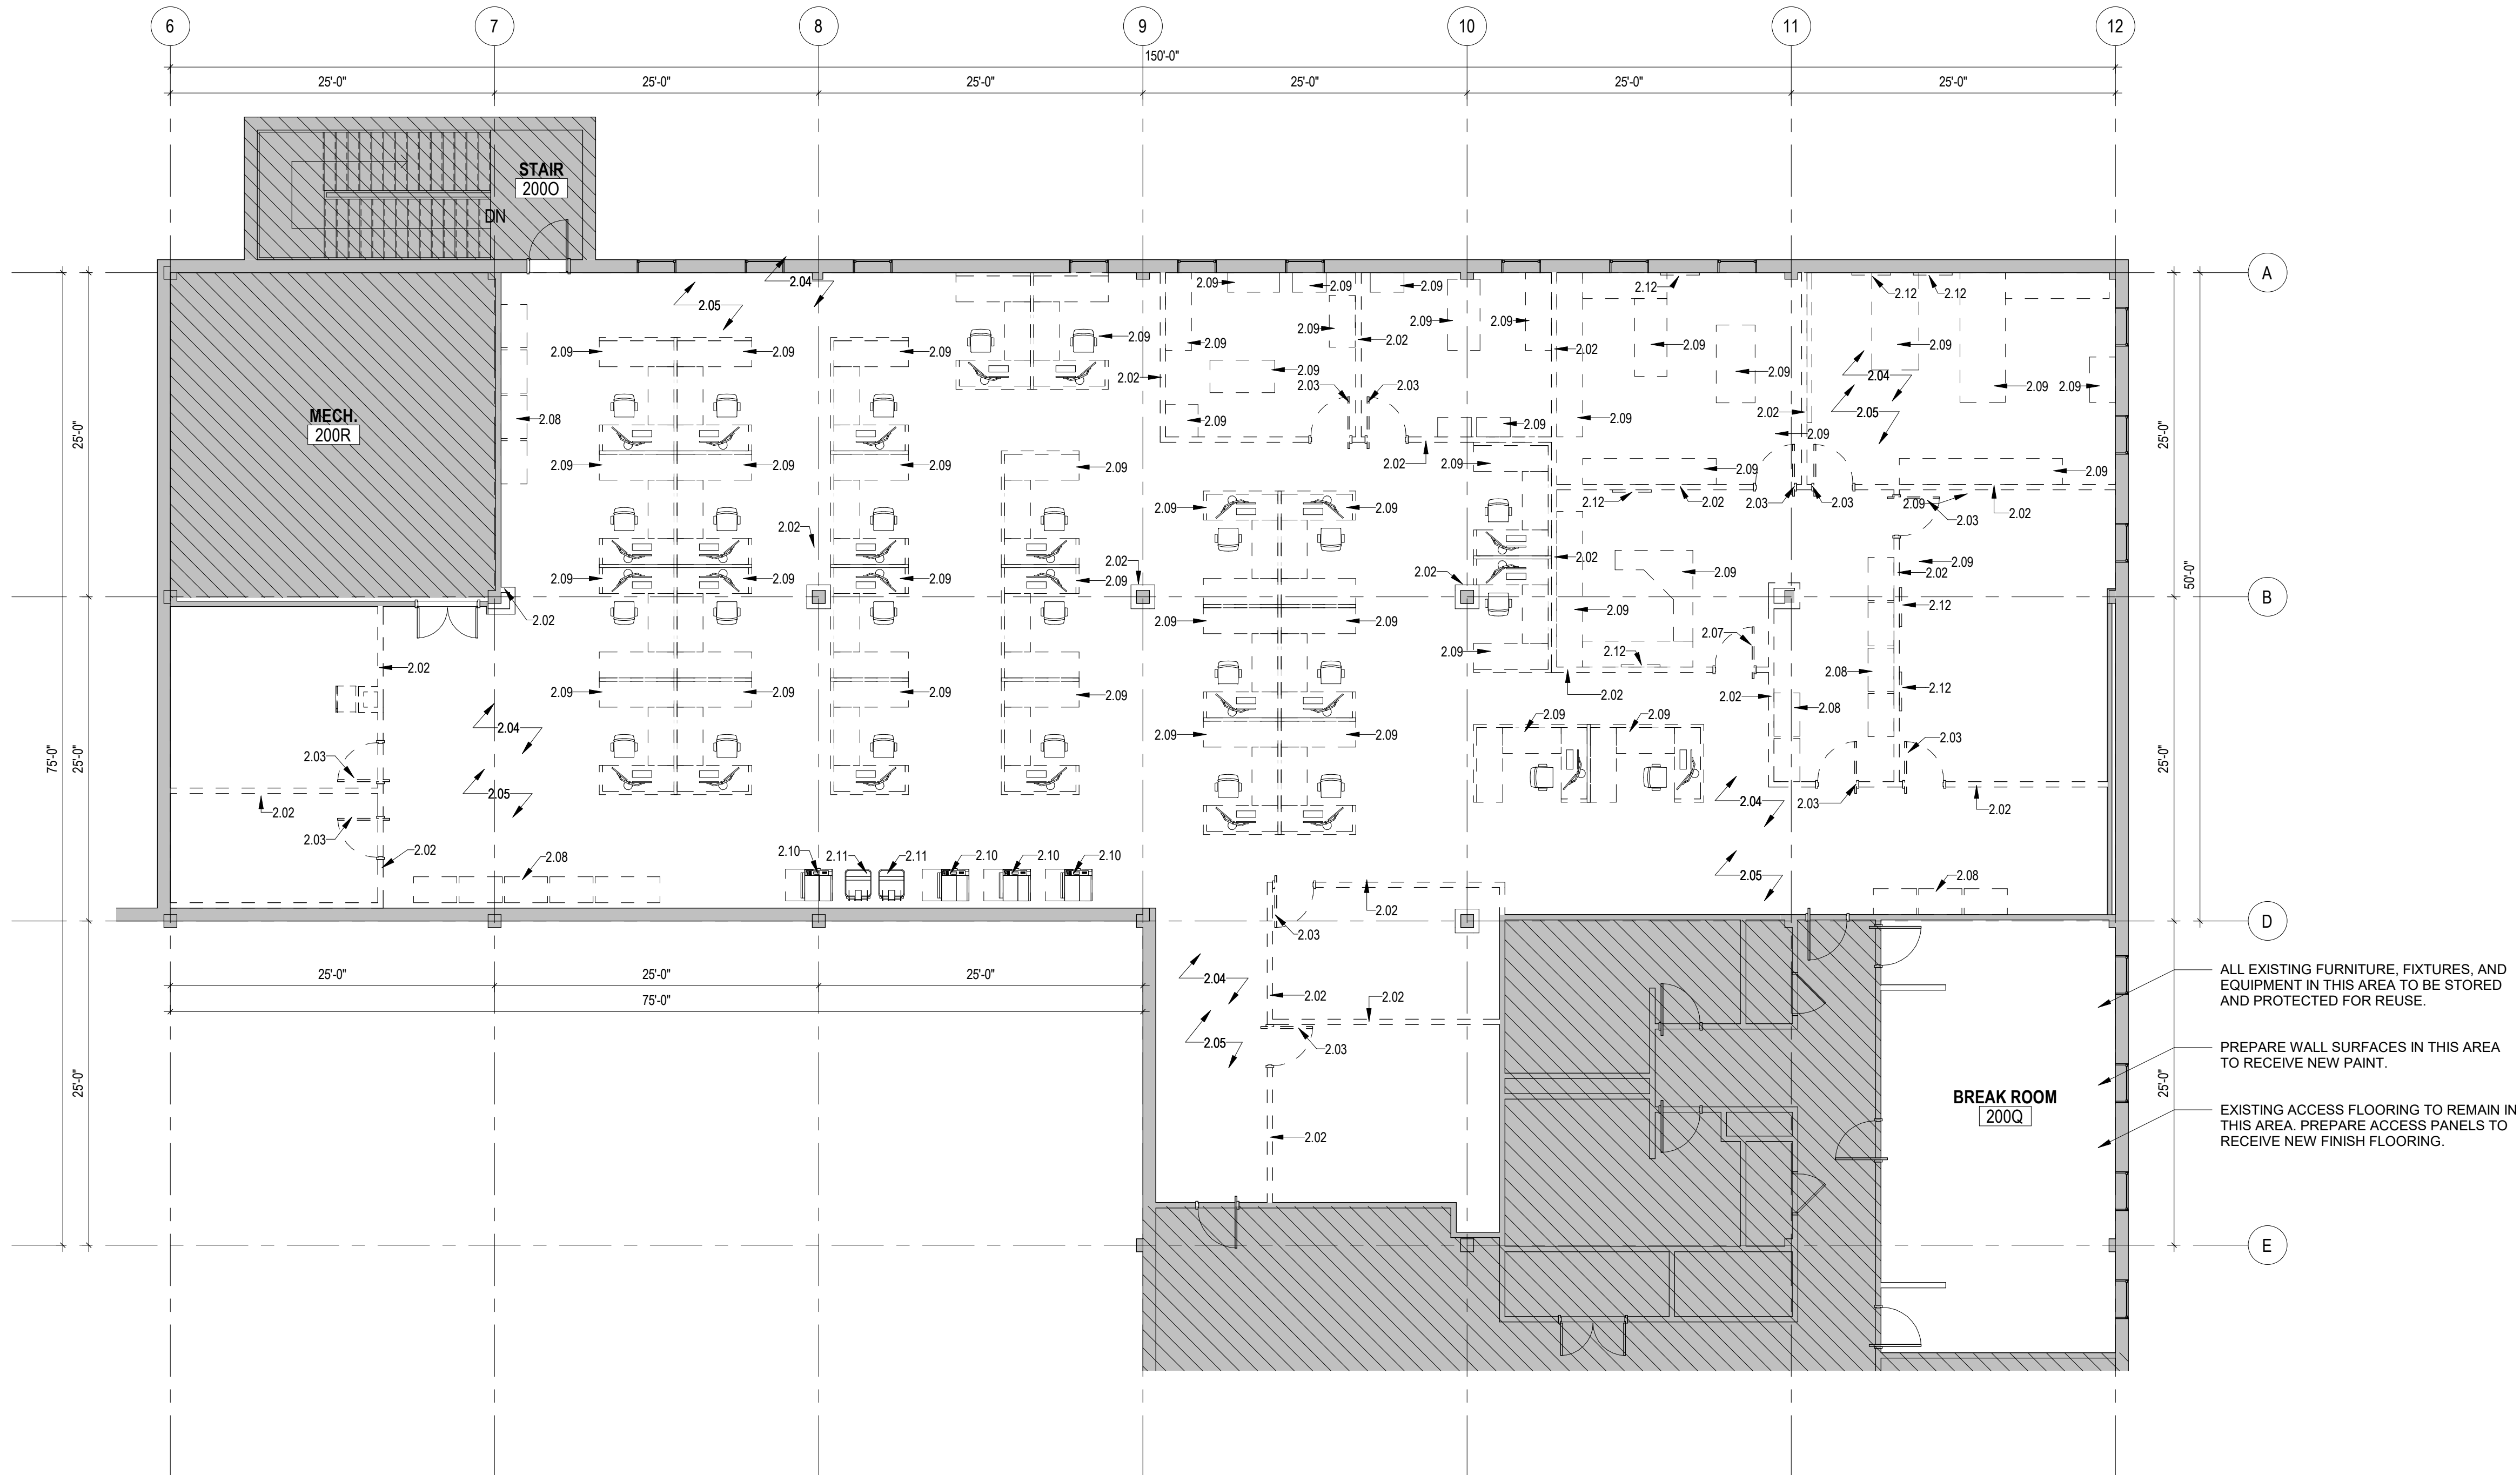

- ALL EXISTING FURNITURE, FIXTURES, AND EQUIPMENT IN THIS AREA TO BE STORED AND PROTECTED FOR REUSE.
- PREPARE WALL SURFACES IN THIS AREA TO RECEIVE NEW PAINT.
- EXISTING ACCESS FLOORING TO REMAIN IN THIS AREA. PREPARE ACCESS PANELS TO RECEIVE NEW FINISH FLOORING.

1 LEVEL 2 - DEMOLITION FLOOR PLAN
1/8" = 1'-0"

No.	REVISION DESCRIPTION	DATE

ARCHITECT / ENGINEER:



SPUR SBBL COLLABORATIVE JV, INC
100 N. STONE AVENUE, STE 1102
TUCSON, AZ 85701
(405) 842-6100

IL ARCH. LICENSE NO.: 001023503 EXP. 11/30/22
IL MECH. ENGR. LICENSE NO.: 062.071715 EXP. 11/30/21
IL ELECT. ENGR. LICENSE NO.: 062.072296 EXP. 11/30/21

MECH / ELEC / PLUMB / TECH ENGINEER
SPUR DESIGN
11020 KING STREET, SUITE 350
OVERLAND PARK, KS 66210
(913) 369-7200

STAMP:



Drawing Title LEVEL 2 - DEMOLITION FLOOR PLAN	Project Title HINES FINANCE CENTER
VA Health Care System Approval:	Location STATION 201, BLDG 215, STE 200X 1ST AVENUE NORTH 22ND STREET HINES, IL 60141
Checked TAB	Drawn JET

Date 06/14/2021	Checked TAB	Drawn JET
---------------------------	----------------	--------------

Project Number 201VB3032	Drawing Number AD-100
Drawing # 4 OF 29	

Veterans Benefits Administration
VA U.S. Department of Veterans Affairs

FULLY SPRINKLERED
100% DESIGN

6/10/2021 3:44:22 PM

GENERAL DEMOLITION NOTES


1. ALL EXISTING WALL DIMENSIONS ARE TO FINISH FACE, UNLESS OTHERWISE NOTED
2. THE CONTRACTOR SHALL VERIFY DIMENSIONS OF AS-BUILT CONDITIONS, AND NOTIFY THE ARCHITECT IN WRITING OF ANY DISCREPANCIES. ALL INFORMATION SHOWN ON THE CONSTRUCTION DOCUMENTS IS BASED ON FIELD OBSERVATIONS AND/OR THE ORIGINAL CONSTRUCTION DOCUMENTS OF THE FACILITY.
3. USE CONSTRUCTION BARRIERS AS REQUIRED TO MITIGATE DUST AND DEBRIS THROUGHOUT DEMOLITION AND CONSTRUCTION. DO NOT REMOVE BARRIERS FROM WORK AREA UNTIL COMPLETED PROJECT AREA HAS BEEN INSPECTED BY THE SAFETY OFFICER.
4. THE CONTRACTOR SHALL PROVIDE PROTECTIVE COVERINGS TO PROTECT EXISTING FLOOR, WALL AND CEILING FINISHES IN EXISTING AREAS NOT DESIGNATED FOR DEMOLITION OR NEW CONSTRUCTION. THE CONTRACTOR SHALL BE RESPONSIBLE FOR THE REPAIR OF ANY DAMAGE CAUSED BY HIS WORK OR ANY SUBCONTRACTOR.
5. THE CONTRACTOR SHALL VERIFY THAT NEW MECHANICAL SYSTEMS CAN BE INSTALLED IN EXISTING SPACES TO CLEAR EXISTING CEILING AND OTHER CONSTRUCTED ITEMS AND MAINTAIN FLOOR TO CEILING HEIGHTS INDICATED ON DRAWINGS. IF DISCREPANCIES OCCUR DUE TO EXISTING CONDITIONS, CONSULT WITH THE ARCHITECT BEFORE PROCEEDING.
6. THE FINISH FACE OF MATERIAL OF NEW PARTITIONS SHALL ALIGN ON BOTH SIDES OF THE PARTITION WITH THE FACE OF THE MATERIALS ON EXISTING COLUMNS, WALLS, OR PARTITIONS, UNLESS NOTED OTHERWISE.
7. NO WORK TO BE DONE IN AREAS HATCHED GRAY IN PLANS, HOWEVER WORK MIGHT NEED TO BE PERFORMED IN CEILING OR EXISTING CHASES THROUGHOUT BUILDING. REFERENCE MECHANICAL AND ELECTRICAL DRAWINGS FOR EXTENT OF WORK. COORDINATE ACCESS TO ROOMS OUTSIDE OF SCOPE WITH OWNER.
8. CAREFULLY REMOVE AND RETAIN ANY EXISTING ARTWORK AND RETURN TO OWNER FOR REINSTALLATION.
9. SPRINKLER CONTRACTOR IS RESPONSIBLE FOR FIELD VERIFYING THE OPERATION, LOCATION AND ROUTING OF THE EXISTING SPRINKLER SYSTEM, INCLUDING RELATED PIPING SYSTEMS, COMPONENTS, SPRINKLERS AND ACCESSORIES PRIOR TO START OF PROJECT.
10. EXISTING SPRINKLER SYSTEMS TO BE MODIFIED TO CONFORM TO THE NEW LAYOUT. ALL EXISTING SPRINKLERS, REMOVED OR DISTURBED IN RENOVATION AREAS, SHALL BE DISPOSED OF AND REPLACED WITH NEW SPRINKLERS.

DEMOLITION CEILING PLAN LEGEND

	AREA IS NOT IN CONTRACT
	EXISTING ACOUSTICAL CEILING GRID AND TILES
	EXISTING LIGHT FIXTURE
	EXISTING EXIT LIGHT
	EXISTING AUDIO / VISUAL FIRE ALARM
	EXISTING RETURN AIR GRILLE
	EXISTING SUPPLY AIR DIFFUSER
	EXISTING EXHAUST AIR GRILLE
	EXISTING DAYLIGHT SENSORS
	KEYNOTE; REFERENCE KEYNOTE LEGEND

DEMOLITION KEYNOTE LEGEND

- 2.20 REMOVE EXISTING CEILING TILE AND GRID SYSTEM THROUGHOUT. REMOVE ALL EXISTING CEILING-MOUNTED MECHANICAL EQUIPMENT AND FIXTURES THROUGHOUT. REFERENCE MECHANICAL DEMOLITION PLANS FOR ADDITIONAL INFORMATION. REMOVE EXISTING CEILING-MOUNTED ELECTRICAL EQUIPMENT AND FIXTURES THROUGHOUT. REFERENCE ELECTRICAL DEMOLITION PLANS FOR ADDITIONAL INFORMATION.

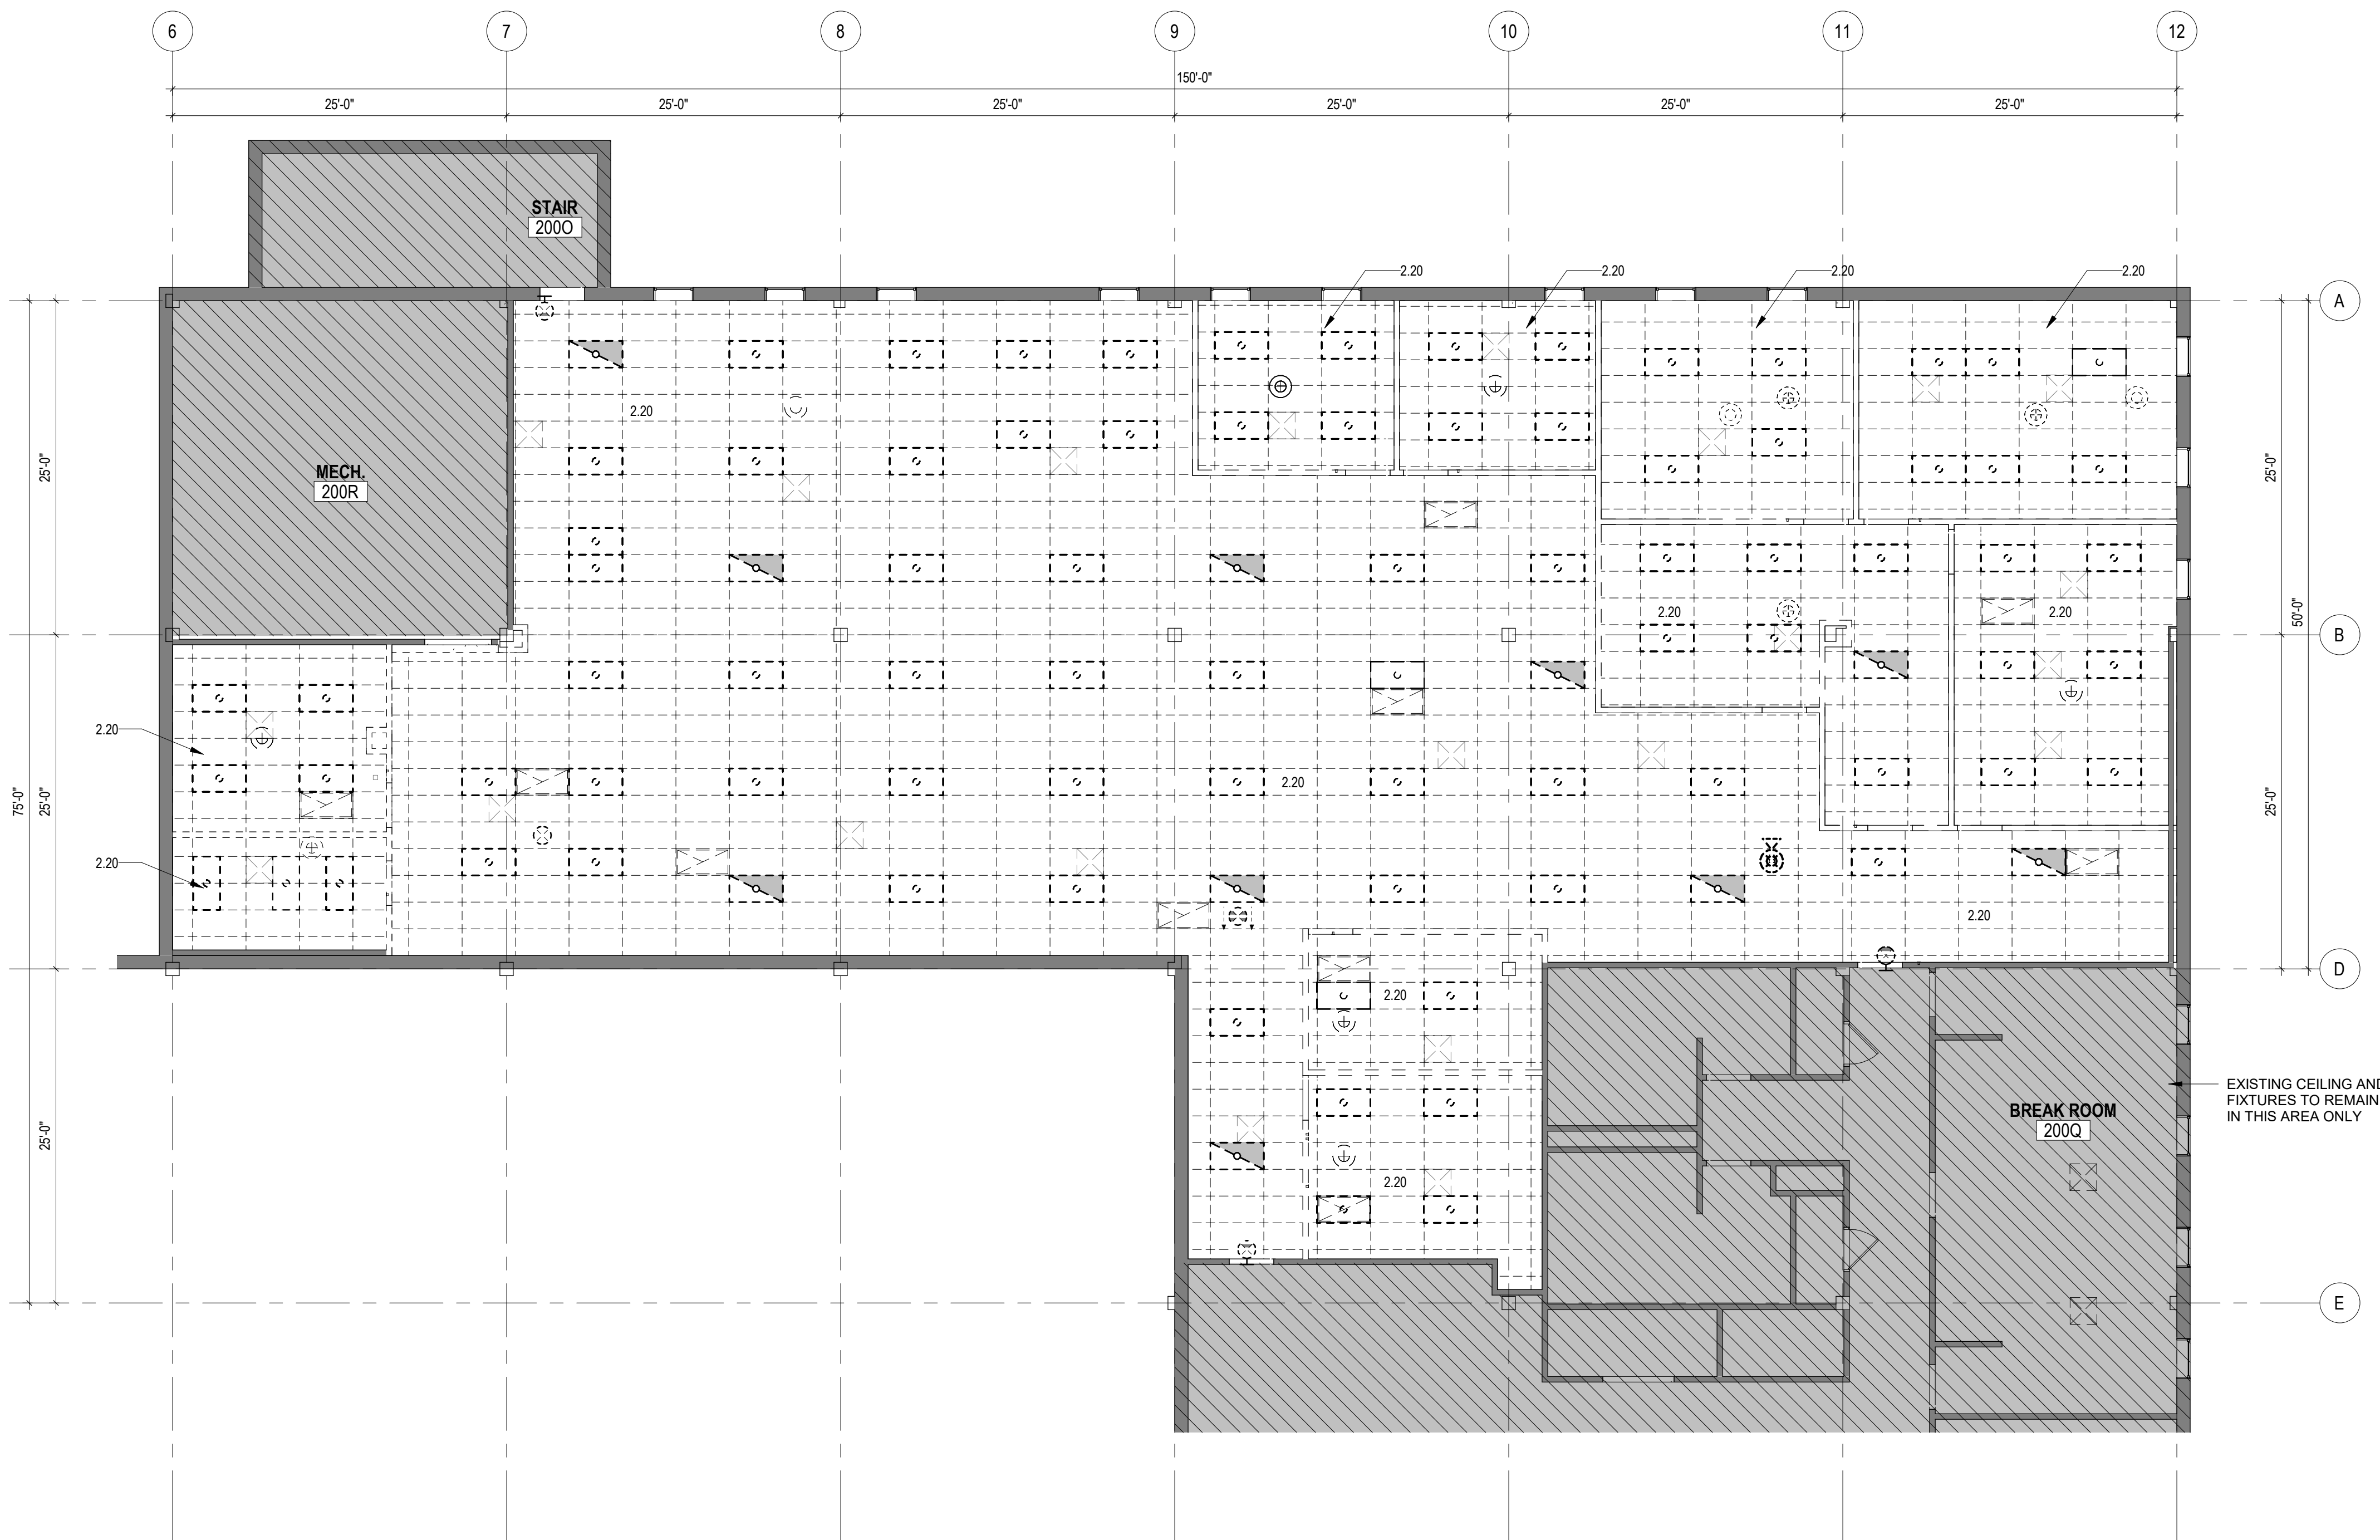

1 LEVEL 2 - DEMOLITION CEILING PLAN
1/8" = 1'-0"

No.	REVISION DESCRIPTION	DATE

ARCHITECT / ENGINEER:



SPUR SBBL COLLABORATIVE JV, INC
100 N. STONE AVENUE, STE 1102
TUCSON, AZ 85701
(405) 842-6100

IL ARCH. LICENSE NO.: 001023503 EXP. 11/30/22
IL MECH. ENGR. LICENSE NO.: 062.071715 EXP. 11/30/21
IL ELECT. ENGR. LICENSE NO.: 062.072296 EXP. 11/30/21

MECH / ELEC / PLUMB / TECH ENGINEER
SPUR DESIGN
11020 KING STREET, SUITE 350
OVERLAND PARK, KS 66210
(913) 369-7200

STAMP:



Drawing Title
LEVEL 2 - DEMOLITION REFLECTED
CEILING PLAN

VA Health Care System Approval:

Project Title
HINES FINANCE CENTER

Location STATION 201, BLDG 215, STE 200X
1ST AVENUE NORTH 22ND STREET
HINES, IL 60141

Date
06/14/2021

Checked
TAB

Drawn
JET

Project Number
201VB3032

Drawing Number

AD-200

Drawing # 5 OF 29

FULLY SPRINKLERED
100% DESIGN

Veterans
Benefits
Administration



6/10/2021 3:44:23 PM

3'8"

1'-0" 2'-0" 2'-0" 1'-0"

2"

5'4"

5'0"

1'-0" 2'-0" 2'-0" 1'-0"

2"

5'4"

5'0"

4'6"

1'-0" 2'-0" 1'-10" 2'-0" 2'-0"

2"

5'4"

5'0"

VA SEAL

REUSE ETCHED GLAZING FROM EXISTING DOOR: REFERENCE DEMOLITION FLOOR PLAN KEYNOTES.

WALL BASE AS SCHEDULED FINISHED FLOOR AS SCHEDULED

INTERIOR WINDOW ALUMINUM FRAME WITH TRIM

W1

INTERIOR WINDOW ALUMINUM FRAME WITH TRIM

W2

* = TEMPERED GLASS

WINDOW SCHEDULE					
MARK	WIDTH	HEIGHT	SILL HEIGHT	HEAD HEIGHT	DESCRIPTION
W1	3'-8"	5'-4"	1'-6"	6'-10"	INTERIOR WINDOW, ALUMINUM FRAME WITH TRIM
W1	3'-8"	5'-4"	1'-6"	6'-10"	INTERIOR WINDOW, ALUMINUM FRAME WITH TRIM
W2	4'-6"	5'-4"	1'-6"	6'-10"	INTERIOR WINDOW, ALUMINUM FRAME WITH TRIM, ETCHED VA SYMBOL IN CENTER PANEL

The technical drawings illustrate three door configurations with their respective dimensions and components:

- D1: WOOD DOOR IN HOLLOW METAL FRAME**
 - Dimensions: 2" (top and side), PER SCHED. (height), SCHED DIM. (width).
 - Components: 1 (Top panel), 2 (Middle panel), 3 (Bottom panel), AE-301 (Hardware).
- D2: SLIDING DOOR AND FRAME ASSEMBLY, SINGLE**
 - Dimensions: PER MANUFACTURER (width), PER SCHED. (height), PER MANUFACTURER (height), PER SCHEDULE (height).
 - Components: 4 (Top panel), AE-301 (Hardware), 5 (Side panel), AE-301 (Hardware).
- D3: SLIDING DOOR AND FRAME ASSEMBLY, DOUBLE**
 - Dimensions: PER MANUFACTURER (width), PER SCHED. (height), PER MANUFACTURER (height), PER SCHEDULE (height).
 - Components: 4 (Top panel), AE-301 (Hardware), 5 (Side panel), AE-301 (Hardware).

Legend: * = TEMPERED GLASS

DOOR SCHEDULE										
MARK	TYPE	TYPE	MATERIAL	PANEL	WIDTH	HEIGHT	RATING	TYPE	FRAME	DESCRIPTION
D02	D2	FL	WOOD / FROSTED GLASS	3'-7 1/4"	6'-11 3/4"	-	2	ANODIZED ALUM		SINGLE SLIDING BARN DOOR
D03	D2	FL	WOOD / FROSTED GLASS	3'-7 1/4"	6'-11 3/4"	-	2	ANODIZED ALUM		SINGLE SLIDING BARN DOOR
D04	D2	FL	WOOD / FROSTED GLASS	3'-7 1/4"	6'-11 3/4"	-	2	ANODIZED ALUM		SINGLE SLIDING BARN DOOR
D05.1	D3	FL	WOOD / FROSTED GLASS	36 11/16"	6'-11 3/4"	-	3	ANODIZED ALUM		DOUBLE SLIDING DOOR, BI-PARTING
D05.2	D1	F	WOOD	3'-6"	7'-0"	-	1	HM / PAINT		SINGLE SWING DOOR
D05.3	D1	F	WOOD	3'-0"	7'-0"	-	1	HM / PAINT		SINGLE SWING DOOR
D06	D2	FL	WOOD / FROSTED GLASS	3'-7 1/4"	6'-11 3/4"	-	2	ANODIZED ALUM		SINGLE SLIDING BARN DOOR
D07	D2	FL	WOOD / FROSTED GLASS	3'-7 1/4"	6'-11 3/4"	-	2	ANODIZED ALUM		SINGLE SLIDING BARN DOOR
D08	D2	FL	WOOD / FROSTED GLASS	3'-7 1/4"	6'-11 3/4"	-	2	ANODIZED ALUM		SINGLE SLIDING BARN DOOR
D09	D2	FL	WOOD / FROSTED GLASS	3'-7 1/4"	6'-11 3/4"	-	2	ANODIZED ALUM		SINGLE SLIDING BARN DOOR
D10	D2	FL	WOOD / FROSTED GLASS	3'-7 1/4"	6'-11 3/4"	-	2	ANODIZED ALUM		SINGLE SLIDING BARN DOOR
D11	D3	FL	WOOD / FROSTED GLASS	36 11/16"	6'-11 3/4"	-	3	ANODIZED ALUM		DOUBLE SLIDING DOOR, BI-PARTING
D12	D2	FL	WOOD / FROSTED GLASS	3'-7 1/4"	6'-11 3/4"	-	2	ANODIZED ALUM		SINGLE SLIDING BARN DOOR
D13	D2	FL	WOOD / FROSTED GLASS	3'-7 1/4"	6'-11 3/4"	-	2	ANODIZED ALUM		SINGLE SLIDING BARN DOOR
D14	D1	FL	WOOD / FROSTED GLASS	3'-7 1/4"	6'-11 3/4"	-	2	ANODIZED ALUM		SINGLE SLIDING BARN DOOR
D15	D2	FL	WOOD / FROSTED GLASS	3'-7 1/4"	6'-11 3/4"	-	2	ANODIZED ALUM		SINGLE SLIDING BARN DOOR
D16.1	D2	FL	WOOD / FROSTED GLASS	3'-7 1/4"	6'-11 3/4"	-	2	ANODIZED ALUM		SINGLE SLIDING BARN DOOR
D16.2	D1	F	WOOD	3'-6"	7'-0"	-	1	HM / PAINT		SINGLE SWING DOOR
D16.3	D1	F	WOOD	3'-0"	7'-0"	-	1	HM / PAINT		SINGLE SWING DOOR
D17A	D1	F	WOOD	3'-0"	7'-0"	-	1	HM / PAINT		SINGLE SWING DOOR
D18	D2	FL	WOOD / FROSTED GLASS	3'-7 1/4"	6'-11 3/4"	-	2	ANODIZED ALUM		SINGLE SLIDING BARN DOOR


PARTITION SCHEDULE			
MARK	WALL TYPE	DESCRIPTION	ACTUAL WIDTH
A1	NON-INSULATED	5/8" GYPSUM BOARD ONE SIDE 7/8" HAT CHANNEL	1 1/2"
B1	INSULATED	5/8" GYPSUM BOARD ONE SIDE OF 3 5/8" METAL STUD W/ BATT INSULATION	4 1/4"
B2	INSULATED	5/8" GYPSUM BOARD ONE SIDE OF 6" METAL STUD W/ BATT INSULATION	6 5/8"
C1	INSULATED	5/8" GYPSUM BOARD EACH SIDE OF 3 5/8" METAL STUD W/ BATT INSULATION	4 7/8"
C2	INSULATED	5/8" GYPSUM BOARD EACH SIDE OF 6" METAL STUD W/ BATT INSULATION	7 1/4"

1. ALL DUCT FRAMES TO BE LOCATED 4" FROM OUTSIDE OF FRAME TO FINISH FACE OF ADJACENT WALL UNLESS NOTED OTHERWISE.
2. REFER TO ARCHITECTURAL DETAILS - DOORS AND WINDOWS (AE-300) FOR DOOR AND WINDOW INFORMATION.
3. ALL NEW WALLS ARE DIMENSIONED TO CENTERLINE OF METAL STUD. UNLESS NOTED OR SHOWN OTHERWISE. ALL EXISTING WALLS TO REMAIN ARE DIMENSIONED TO THE FACE OF THE FINISHED WALL.
4. BLOCK OUT SLAB FOR PENETRATIONS SHALL BE 2" LARGER THAN DUCT SIZE TO ALLOW TOLERANCE FOR DUCT PASSAGE AND FIRE SAFING. COORDINATE WITH MEP FOR DUCT SIZES.
5. FURR AROUND ALL COLUMN PROTRUSIONS AS NEEDED UNLESS NOTED OTHERWISE.

1. NOT ALL PARTITIONS TYPES SHOWN HERE MAY BE USED. REFER TO PLANS FOR LOCATION AND TYPES OF EACH PARTITION.
2. PAINT CONTINUOUS "X" TALL, STENCILED LETTERS: ABOVE CEILING, ON BOTH SIDES OF ALL FIRE AND SMOKE WALLS DESIGNATING THE PARTITION RATING INDICATED ON THE LIFE SAFETY PLAN.
3. REFER TO FINISH SCHEDULE AND INTERIOR ELEVATIONS FOR LOCATIONS OF ALL FIRE WALL. PROVIDE AND INSTALL CEMENTIOUS BACKER BOARD IN LIEU OF GYP BOARD AT ALL SCHEDULED FIRE LOCATIONS. UNLESS NOTED OTHERWISE, THE WALL BE INSTALLED PER THE COUNCIL OF AMERICA LATEST STANDARDS FOR EACH TYPE OF BACKING MATERIAL REPRESENTED IN WALL/PARTITION.
4. ALL SUSPENDED WALLS AND PARTITIONS SHALL HAVE GYP BOARD WHICH EXTENDS A MINIMUM OF 6" ABOVE THE SUSPENDED CEILING UNLESS SHOWN AND/OR NOTED OTHERWISE BY THE ARCHITECT.
5. REFER TO STRUCTURAL DRAWINGS FOR ALL LOAD BEARING WALL CONDITIONS IN REGARDS TO STRUCTURAL REQUIREMENTS.
6. "ALUM" MEANS SIMILAR COMPONENTS OF CONSTRUCTION, E. G. WALLS, JAMBS, ETC. SHALL ALIGN ACROSS VOIDS AND JOINTS.
7. PARTITIONS SHALL BE CONTINUOUS OVER DOORS SAME ADJACENT WALLS (UNLESS NOTED OTHERWISE) WHERE DRYWALL CONTINUES ABOVE CEILING AND ABOVE THE CEILING LINE UP TO THE STRUCTURE ABOVE. ALL GYPSUM BOARD RETURNS SHALL HAVE CORNERS BEHIND MINIMUM 1/4" TO CEILING. ALL PENETRATIONS IN DRYWALL CONTINUING ABOVE FINISHED CEILING SHALL BE EFFECTIVELY SEALED TO PREVENT SOUND LEAKAGE AND FIRE STOPPING TAPE/CAULK AT ALL RATED PARTITIONS.
8. ALL MECHANICAL CHASERS AND OTHER NOTED CHASERS ARE TO EXTEND UP TO THE UNDERSIDE OF THE CEILING STRUCTURE ABOVE ALL PLUMBING CHASERS UNLESS NOTED OTHERWISE. SHALL EXTEND ABOVE THE HIGHEST ADJOINING CEILING AND BE BRACED TO STRUCTURE.
9. ALL CONSTRUCTION DESIGNATED TO BE SUPPORTED BY ROOF STRUCTURE SHALL BE SUPPORTED BY TOP CHORD OR STRUCTURAL JOISTS AND NOT FROM THE METAL DECK.
10. COORDINATE WITH MILLWORK DRAWINGS FOR PLACEMENT OF BLOCKING IN WALLS/PARTITIONS. ALL WOOD BLOCKING IS TO BE FIRE RETARDANT TREATED.
11. SEAL RESISTANT GYP BOARD, WHERE NOTED, IS OPTIONAL ABOVE 8' AFF.
12. IMPACT THE TOP AND BOTTOM OF WALL AS WELL AS ALL PENETRATIONS WHERE SMOKE PARTITIONS ARE DESIGNATED ON THE LIFE SAFETY PLAN TO ELIMINATE THE PASSAGE OF SMOKE.
13. USE DEFLECTION TRACKS WHERE STUD WALLS ATTACH DIRECTLY TO METAL DECK.

	AREA IS NOT IN CONTRACT
	EXISTING WALLS TO REMAIN
	NEW DOOR / DOOR TAG
ROOM NAME 	ROOM TAG / ROOM NUMBER / AREA
	PARTITION TAG
	WINDOW TAG

ROOM SCHEDULE		
ROOM #	ROOM NAME	AREA
200.01	RECEPTION	262 SF
200.02	CHIEF	108 SF
200.03	CHIEF	111 SF
200.04	COLLAB	88 SF
200.05	CONFERENCE	893 SF
200.05.1	STOR	35 SF
200.06	DIRECTOR	203 SF
200.07	DEPUTY	141 SF
200.08	DEPUTY	142 SF
200.09	DEPUTY	141 SF
200.10	DEPUTY	142 SF
200.11	COLLAB	193 SF
200.12	CHIEF	116 SF
200.13	CHIEF	116 SF
200.14	CHIEF	115 SF
200.15	CHIEF	116 SF
200.16	OPEN OFFICE B	1047 SF
200.16.1	STOR	47 SF
200.17	OPEN OFFICE A	1467 SF
200.17.1	STOR	21 SF
200.17.2	PRINT	69 SF
200.18	MANAGEMENT ANALYST	355 SF
200A	CORRIDOR	186 SF
200B	CORRIDOR	326 SF
200C	CORRIDOR	457 SF
200D	CORRIDOR	149 SF
200Q	BREAK ROOM	599 SF

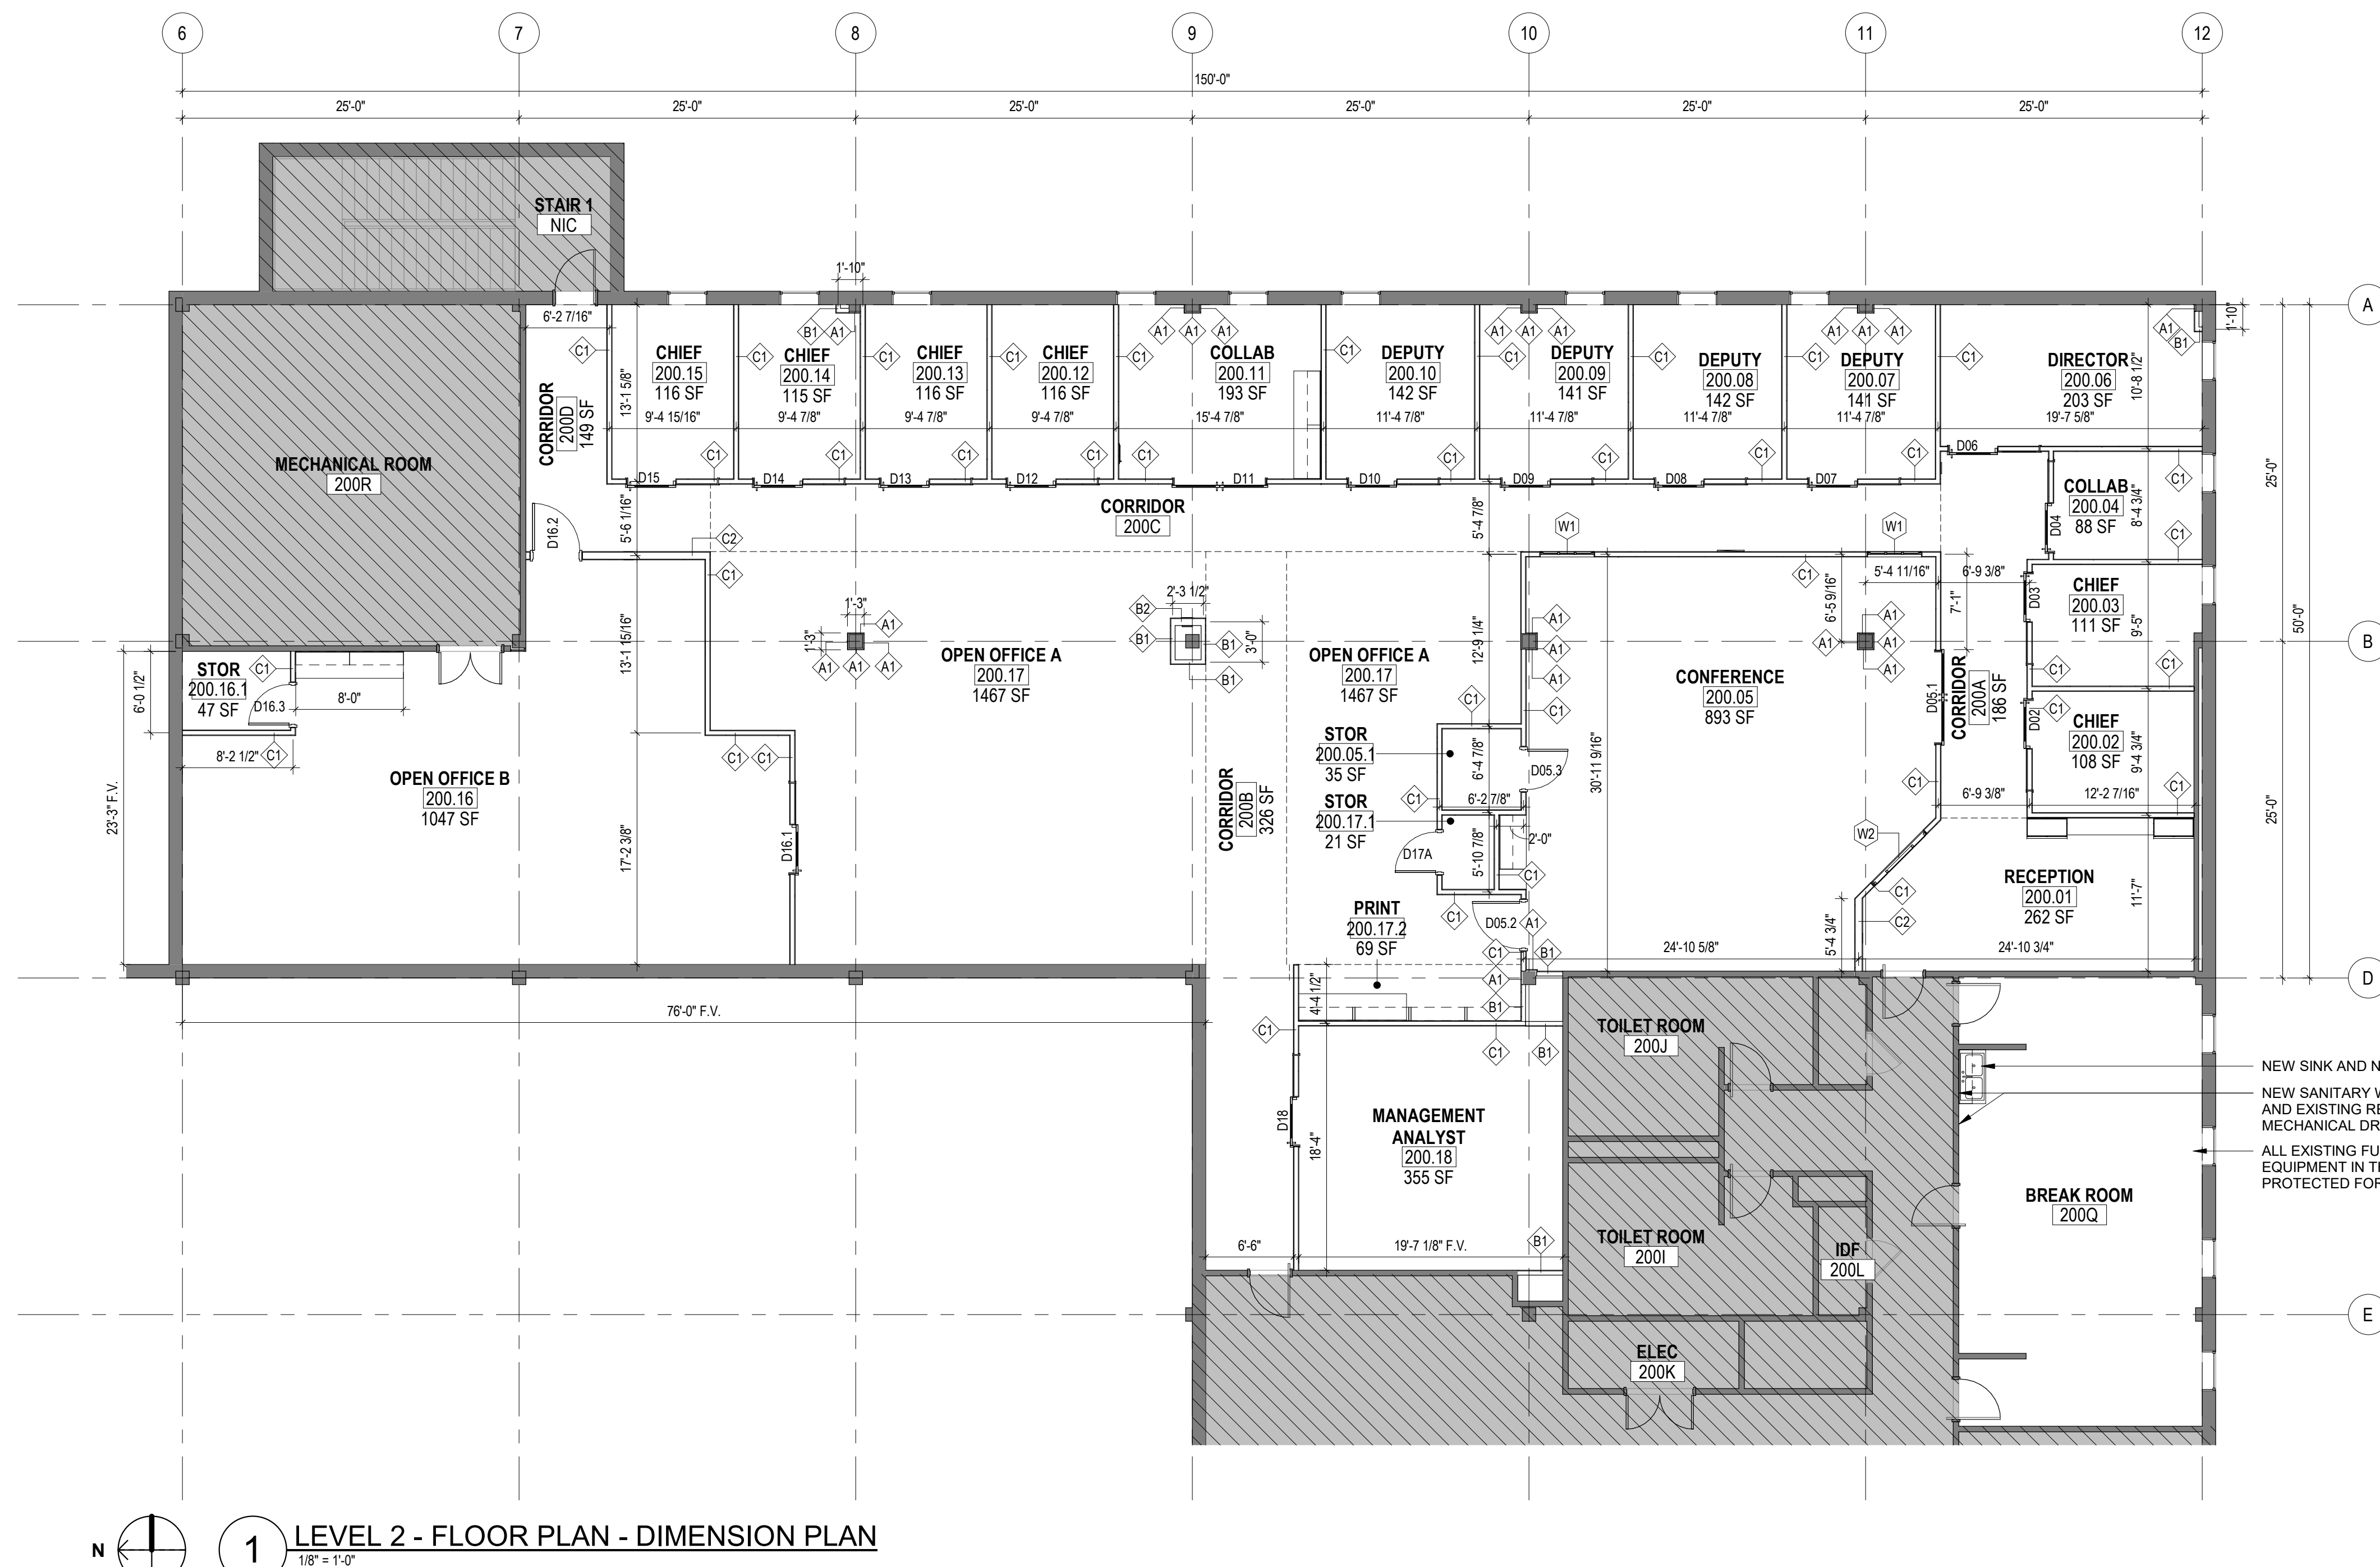

NEW SINK AND NEW CASEWORK

NEW SANITARY WATER SUPPLY CONNECTION FOR SINK
AND EXISTING REFRIGERATOR / ICE MAKER; REFERENCE
MECHANICAL DRAWINGS FOR ADDITIONAL INFORMATION

ALL EXISTING FURNITURE, FIXTURES, AND
EQUIPMENT IN THIS AREA TO BE STORED AND
PROTECTED FOR REUSE.

[illegible]

ARCHITECT / ENGINEER:




SPUR SBBL COLLABORATIVE JV, INC
100 N. STONE AVENUE, STE 1102
TUCSON, AZ 85701
(405) 842-6100

IL ARCH. LICENSE NO.: 001023503 EXP. 11/30/22
IL MECH. ENGR. LICENSE NO.: 062.071715 EXP. 11/30/21
IL ELECT. ENGR. LICENSE NO.: 062.072296 EXP. 11/30/21

MECH / ELEC / PLUMB / TECH ENGINEER
SPUR DESIGN
11020 KING STREET, SUITE 350
OVERLAND PARK, KS 66210
(913) 369-7200

STAMP:

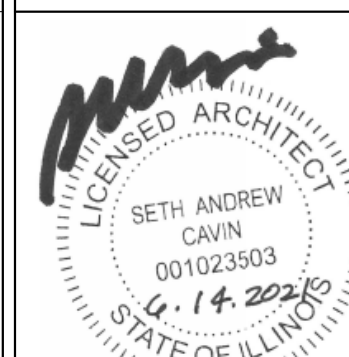

Drawing Title
**LEVEL 2 - FLOOR PLAN - DIMENSION
PLAN**

VA Health Care System Approval: _____

Project Title	HINES FINANCE CENTER
---------------	-----------------------------

Location	STATION 201, BLDG 215, STE 100 1ST AVENUE NORTH 22ND S
----------	---

Checked TAB	Draw JET
----------------	-------------

TER	Project Number 201VB3032
-----	-----------------------------

Drawing Number

AE-100


Drawing # 6 OF 29

Veterans
Benefits
Administration



FULLY SPRINKLERED
100% DESIGN

FURNITURE, FIXTURES, EQUIPMENT SCHEDULE		
MARK	DESCRIPTION	QTY
EQUIPMENT		
AED	AUTOMATED EXTERNAL DEFIBRILLATOR (AED) CABINET	1
E-1	PRINT / COPY / FAX MACHINE	7
E-2	RECYCLE BIN	4
E-3	COFFEE MAKER	1
E-4	MICROWAVE	2
E-5	TELEVISION	2
E-6	REFRIGERATOR, LARGE	2
E-7	REFRIGERATOR, SMALL	2
FEC	FIRE EXTINGUISHER CABINER, SEMI RECESSED	3
FURNITURE		
F-1	ARTWORK	3
F-2	TABLE, CONFERENCE	1
F-3	TABLE, COLLABORATION	3
F-4	TABLE, COFFEE	1
F-5	TABLE, SIDE	3
F-6	CHAIR, TASK	74
F-7	CHAIR, GUEST	16
F-8	CHAIR, CONFERENCE	18
F-9	CHAIR, STACKABLE	43
F-10	CHAIR, RECEPTION	4
F-11	STORAGE, LOCKABLE	1
WORKSTATION		
WS-1A	WORKSTATION, TYPICAL (WS-1A)	20
WS-1B	WORKSTATION, TYPICAL (WS-1B)	14
WS-2	WORKSTATION, CHIEF (WS-2)	6
WS-3	WORKSTATION, DEPUTY (WS-3)	4
WS-4	WORKSTATION, MGMT ANALYST (WS-4)	1
WS-5	WORKSTATION, DIRECTOR (WS-5)	1

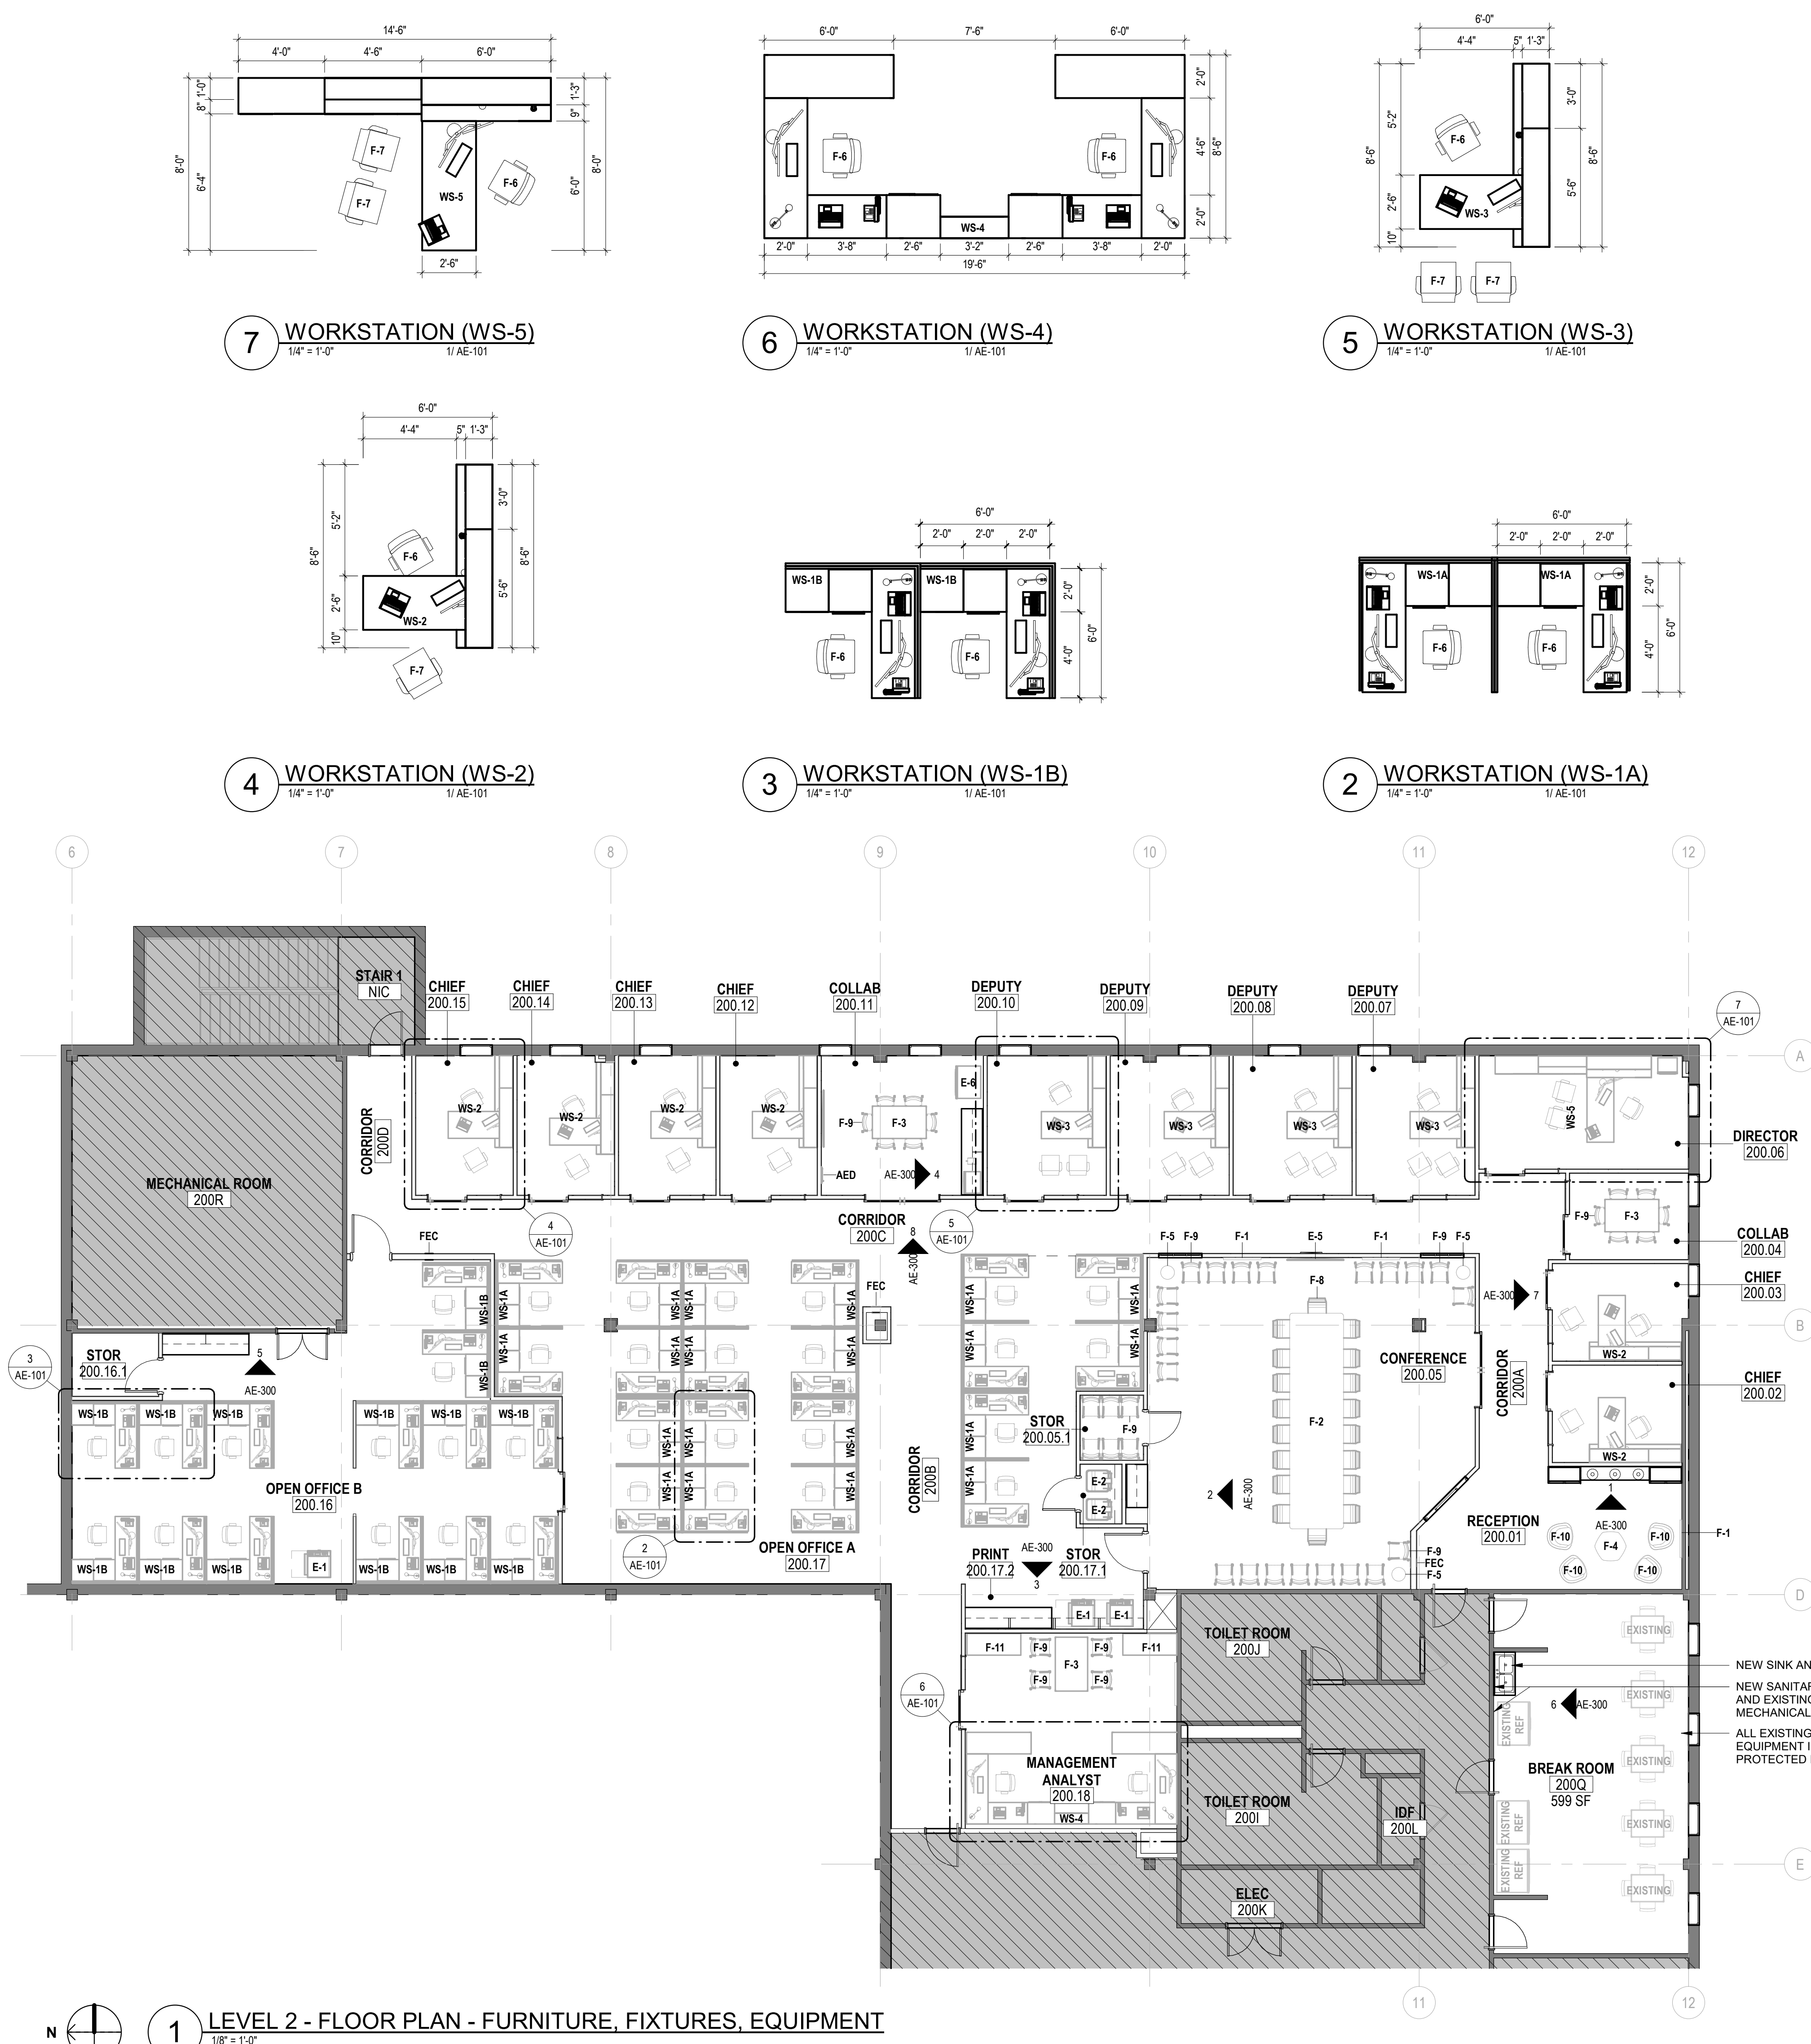

1 LEVEL 2 - FLOOR PLAN - FURNITURE, FIXTURES, EQUIPMENT
1/8" = 1'-0"

NEW SINK AND NEW CASEWORK
NEW SANITARY WATER SUPPLY CONNECTION FOR SINK AND EXISTING REFRIGERATOR / ICE MAKER; REFERENCE MECHANICAL DRAWINGS FOR ADDITIONAL INFORMATION.
ALL EXISTING FURNITURE, FIXTURES, AND EQUIPMENT IN THIS AREA TO BE STORED AND PROTECTED FOR REUSE.

No. REVISION DESCRIPTION DATE 	ARCHITECT / ENGINEER: 		SPUR SBBL COLLABORATIVE JV, INC 100 N. STONE AVENUE, STE 1102 TUCSON, AZ 85701 (405) 842-6100 IL ARCH. LICENSE NO.: 001023503 EXP. 11/30/22 IL MECH. ENGR. LICENSE NO.: 062.071715 EXP. 11/30/21 IL ELEC. ENGR. LICENSE NO.: 062.072296 EXP. 11/30/21		STAMP: 	Drawing Title LEVEL 2 - FLOOR PLAN - FF&E		Project Title HINES FINANCE CENTER		Project Number 201VB3032		Veterans Benefits Administration U.S. Department of Veterans Affairs
			VA Health Care System Approval:			Location STATION 201, BLDG 215, STE 200X 1ST AVENUE NORTH 22ND STREET HINES, IL 60141		Drawing Number AE-101				
						Date 06/14/2021		Checked TAB		Drawn JET		
								Drawing # 7 OF 29				

6/10/2021 3:44:36 PM

	AREA NOT IN CONTRACT
	GYPSUM BOARD CEILING PAINTED (P1)
	2' X 2' ACOUSTICAL CEILING TILE AND GRID
	CEILING HEIGHT, ABOVE FINISH FLOOR
	EXIT LIGHT
	RECESSED CAN LIGHT
	RECESSED CAN LIGHT, EMERGENCY
	LIGHT FIXTURE, 24" X 24"
	LIGHT FIXTURE, EMERGENCY, 24" X 24"
	LIGHT FIXTURE, RECESSED COVE
	RETURN AIR GRILLE
	SUPPLY AIR DIFFUSER
	EXHAUST AIR GRILLE
	ACCESS DOOR



Veterans
Benefits
Administration

VA  **U.S. Department
of Veterans Affairs**

[illegible]

SPURR
DESIGN

IL ARCH. LICENSE NO.: 001023503 EXP. 11/30/22
IL MECH. ENGR. LICENSE NO.: 062.071715 EXP. 11/30/21
IL ELECT. ENGR. LICENSE NO.: 062.072296 EXP. 11/30/21

MECH / ELEC / PLUMB / TECH ENGINEER
SPUR DESIGN
11020 KING STREET, SUITE 350
OVERLAND PARK, KS 66210
(913) 369-7200

VA Health Care System Approval: _____

Location	STATION 201, BLDG 215, STE 200X 1ST AVENUE NORTH 22ND STREET HINES IL 60141
----------	---

Date
06/14/2021

Checked	TAB
---------	-----

Drawn
SNP


Drawing Number

AE-200


Drawing # 9 OF 29

INTERIOR ELEVATIONS - GENERAL NOTES


1. ALL WALLS TO BE PAINTED (PT1), UNLESS NOTED OTHERWISE. REFERENCE SHEET AE-102 FOR ROOM FINISH SCHEDULE.
2. ALL COUNTERTOPS TO BE (SS1), UNLESS NOTED OTHERWISE. REFERENCE SHEET AE-301 FOR MILLWORK SECTIONS.
3. ALL RUBBER WALL BASE TO BE (RB1), UNLESS NOTED OTHERWISE. REFERENCE SHEET AE-102 FOR ROOM FINISH SCHEDULE.
4. ALL WINDOW SILLS TO BE (SS1), UNLESS NOTED OTHERWISE. REFERENCE SHEET AE-301 FOR WINDOW SILL DETAIL.
5. ALL NEW FLUSH WOOD DOORS TO BE FINISHED WITH PLASTIC LAMINATE (PLAM3), UNLESS NOTED OTHERWISE. REFERENCE SHEET AE-301 FOR DOOR AND WINDOW DETAILS.
6. ALL NEW SLIDING DOORS TO HAVE FROSTED GLASS PANEL. DOOR RAILS AND STILES TO BE FINISHED WITH PLASTIC LAMINATE (PLAM3) UNLESS NOTED OTHERWISE. REFERENCE SHEET AE-301 FOR DOOR AND WINDOW DETAILS.

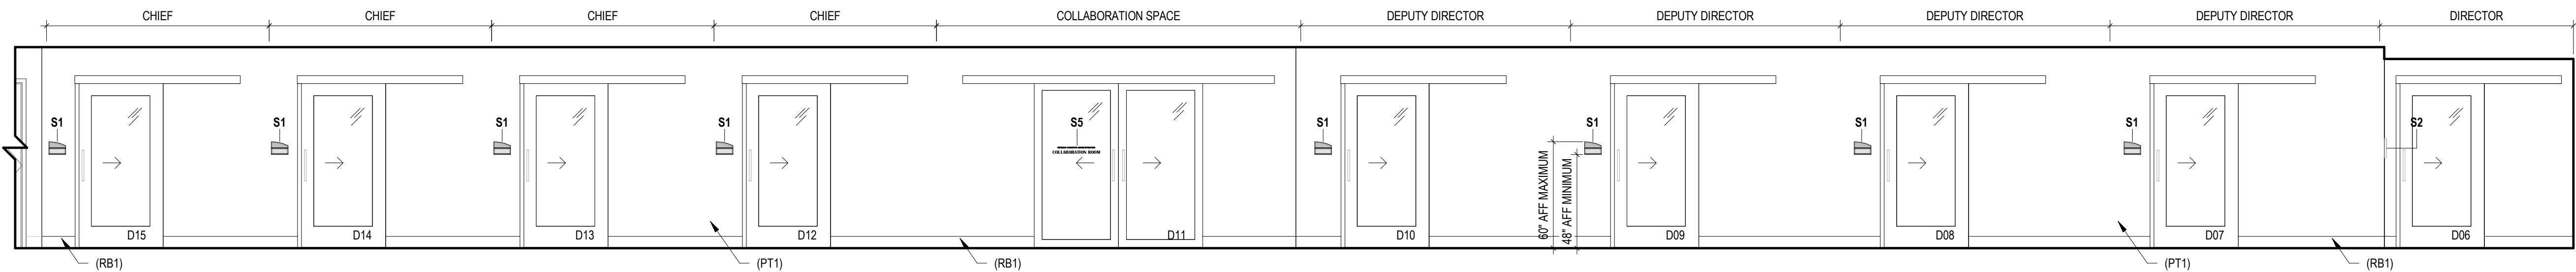


8 ELEVATION - CORRIDOR AT OFFICE ENTRY
1/4" = 1'-0"

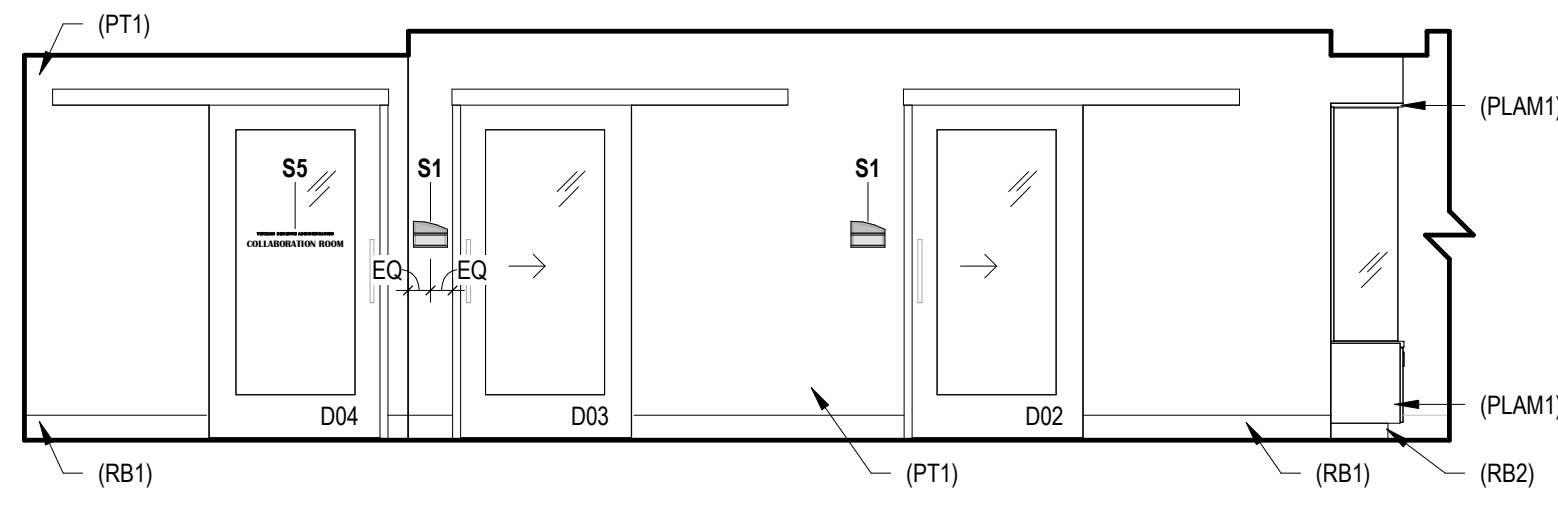


7 ELEVATION - COORIDOR AT OFFICES AND COLABORATION ENTRY
1/4" = 1'-0"

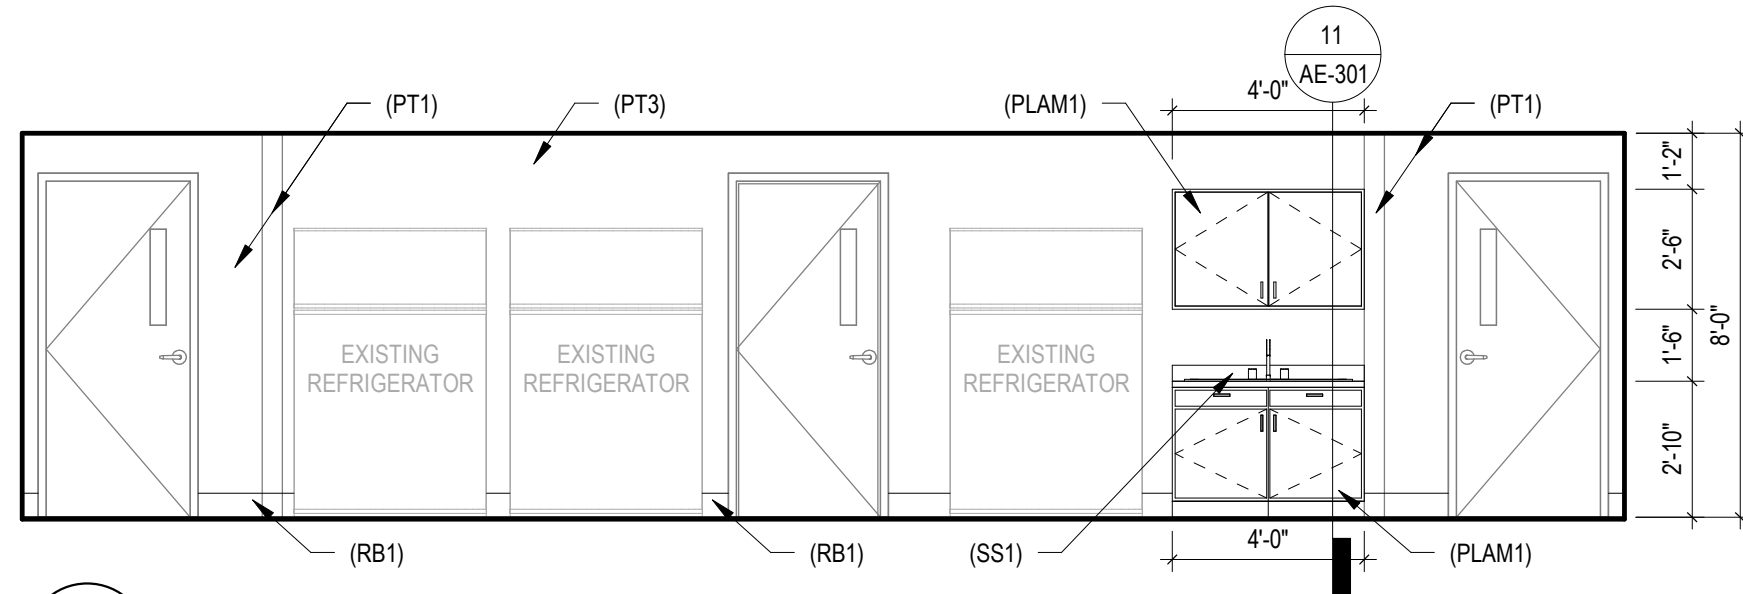


6 ELEVATION - KITCHENETTE AT BREAK ROOM
1/4" = 1'-0"

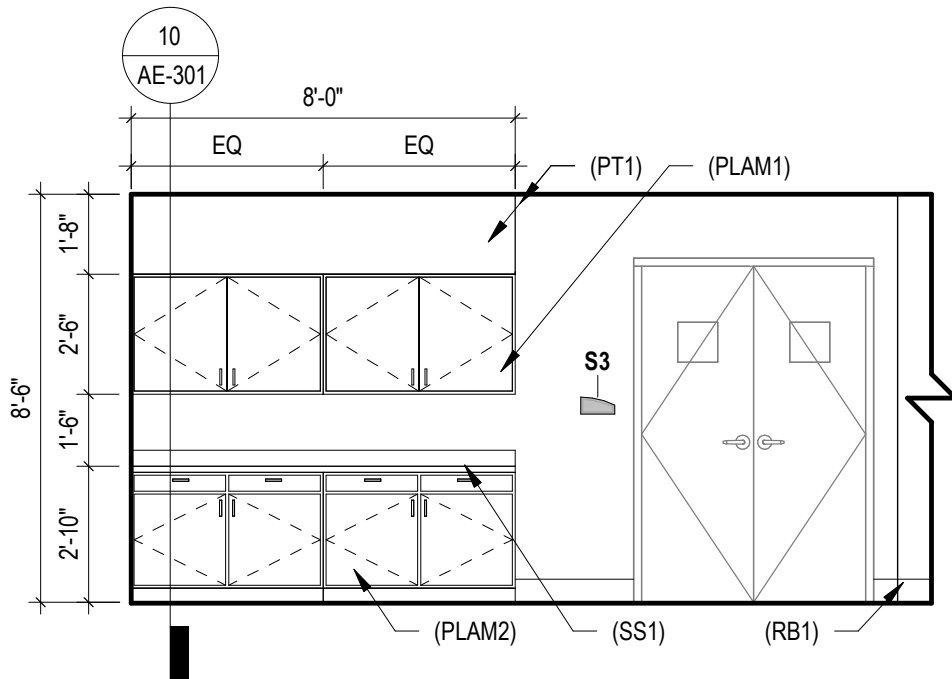


5 ELEVATION - WORK COUNTER AT OPEN OFFICE
1/4" = 1'-0"

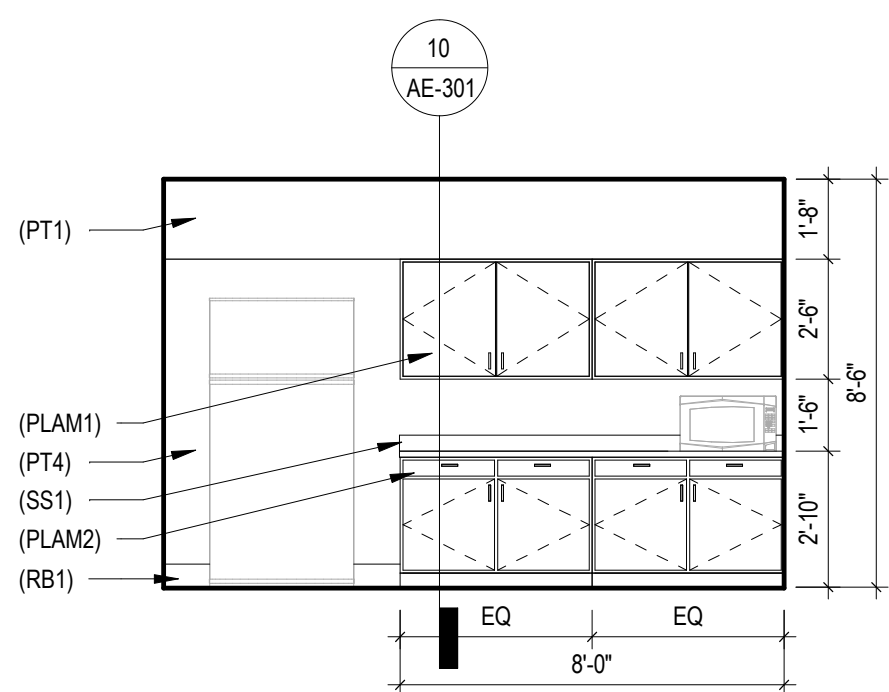


4 ELEVATION - KITCHENETTE AT COLLAB
1/4" = 1'-0"

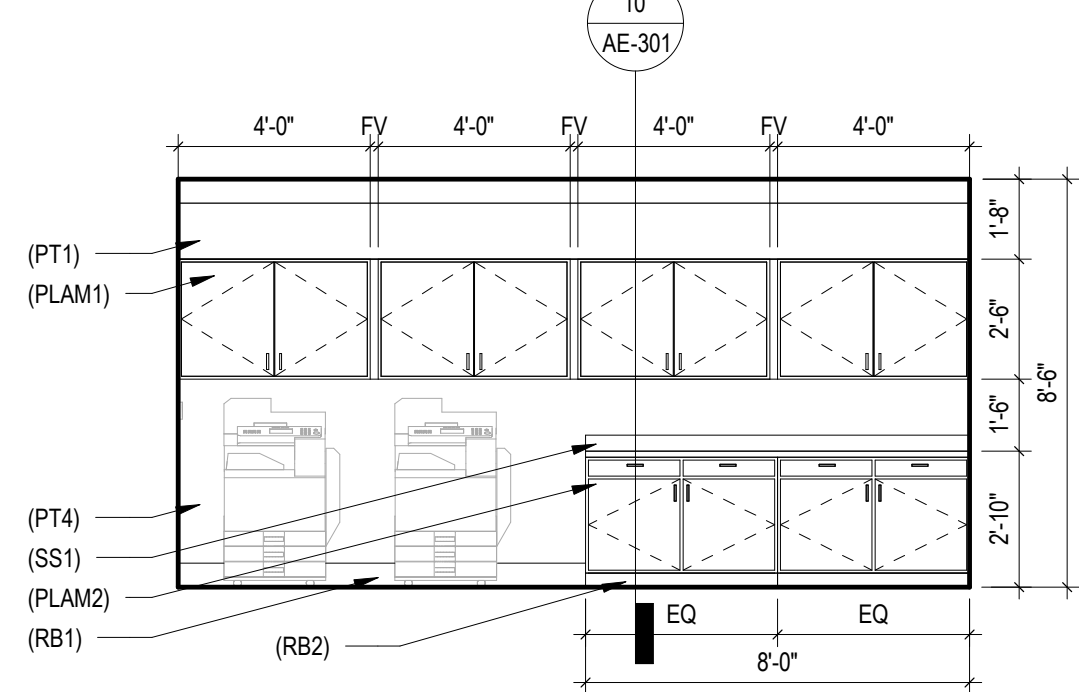

3 ELEVATION - WORK COUNTER AT PRINT AREA
1/4" = 1'-0"

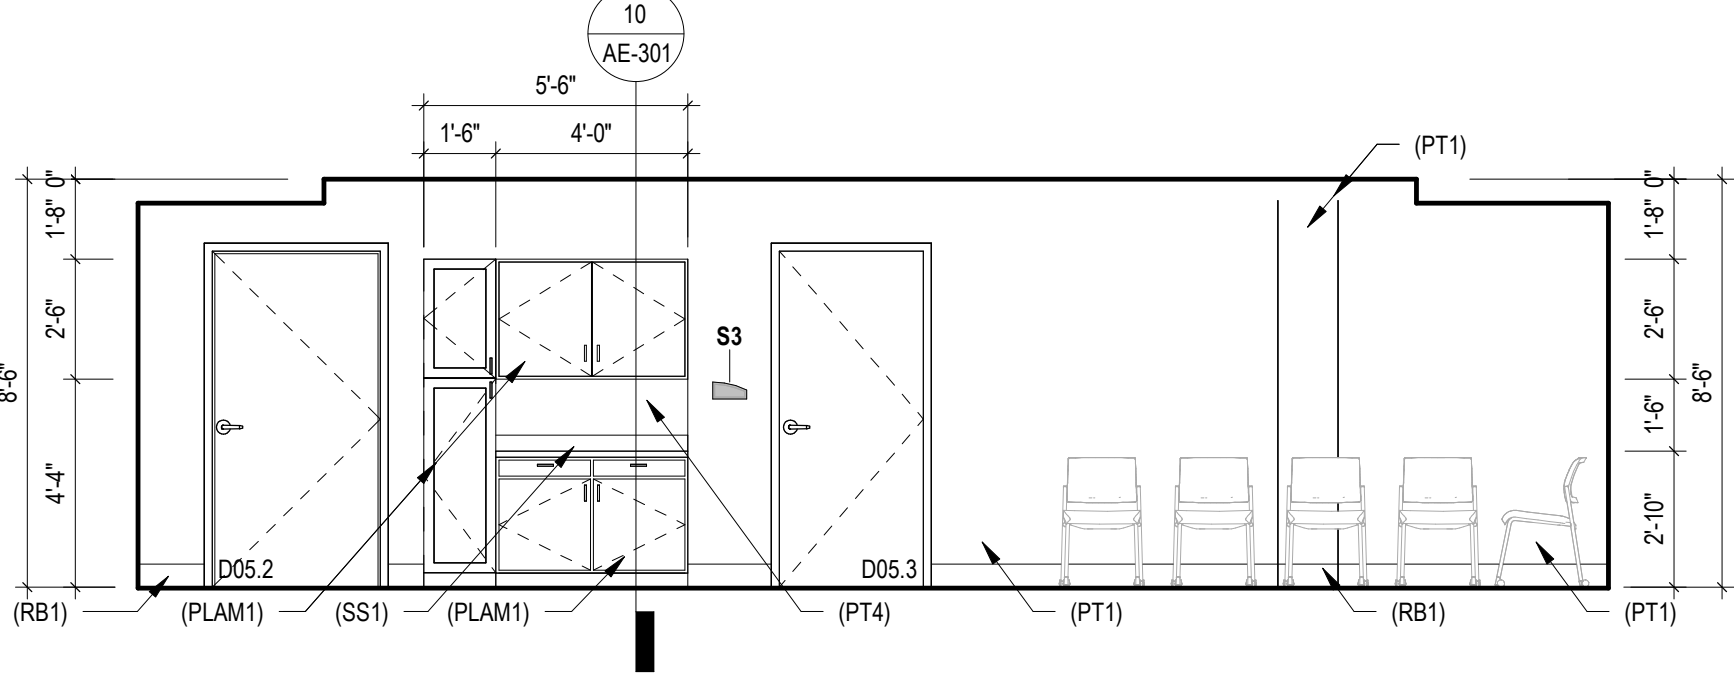

2 ELEVATION - CONFERENCE REFRESHMENTS
1/4" = 1'-0"

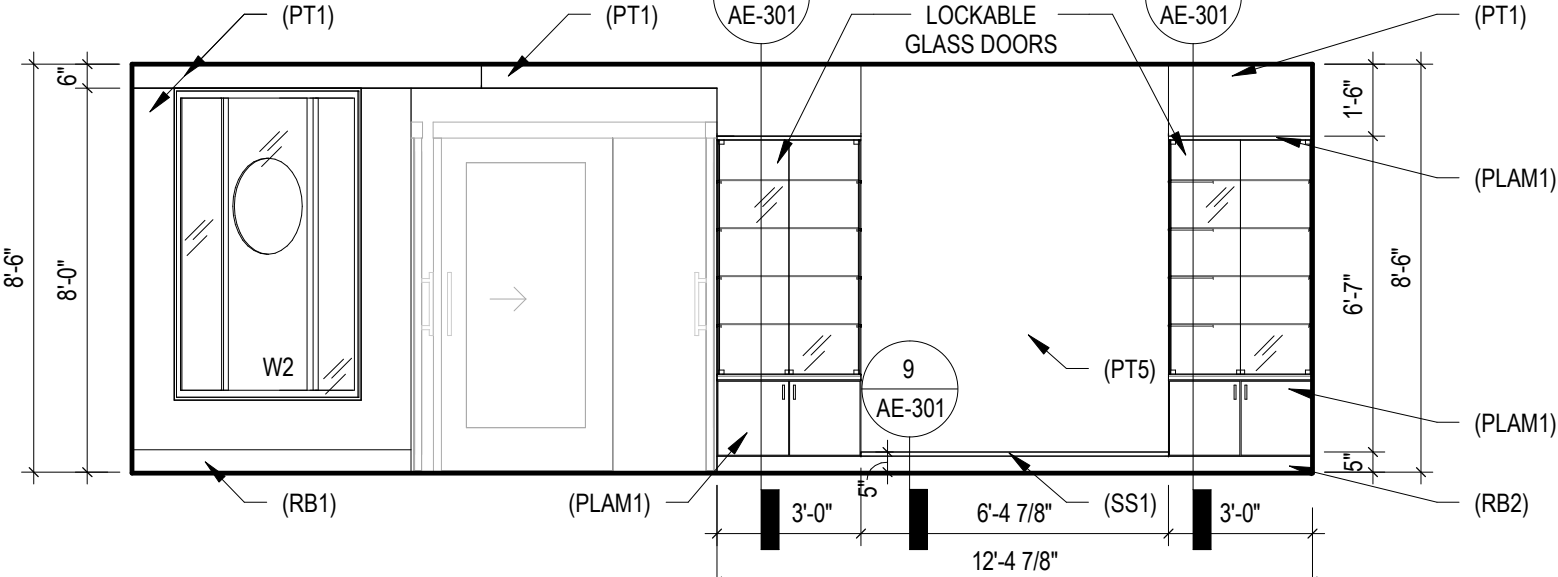

1 ELEVATION - DISPLAY CABINET AND FLAG STAND
1/4" = 1'-0"

No.	REVISION DESCRIPTION	DATE

ARCHITECT / ENGINEER:



SPUR SBBL COLLABORATIVE JV, INC
100 N. STONE AVENUE, STE 1102
TUCSON, AZ 85701
(405) 842-6100

IL ARCH. LICENSE NO.: 001023503 EXP. 11/30/22
IL MECH. ENGR. LICENSE NO.: 062.071715 EXP. 11/30/21
IL ELECT. ENGR. LICENSE NO.: 062.072296 EXP. 11/30/21

MECH / ELEC / PLUMB / TECH ENGINEER
SPUR DESIGN
11020 KING STREET, SUITE 350
OVERLAND PARK, KS 66210
(913) 369-7200

STAMP:



Drawing Title INTERIOR ELEVATIONS
VA Health Care System Approval:

Project Title HINES FINANCE CENTER
Location STATION 201, BLDG 215, STE 200X 1ST AVENUE NORTH 22ND STREET HINES, IL 60141
Date 06/14/2021
Checked TAB
Drawn SNP

Project Number 201VB3032
Drawing Number AE-300
Drawing # 10 OF 29

Veterans
Benefits
Administration




FULLY SPRINKLERED
100% DESIGN


6/10/2021 3:44:44 PM

GENERAL MILLWORK NOTES


1. FIELD VERIFY DIMENSIONS PRIOR TO FABRICATION OF MILLWORK.
2. COORDINATE LOCATION OF RECEPTACLES WITH ELECTRICAL DRAWINGS AND EQUIPMENT LOCATIONS.
3. WHERE FLUR DOWNS ARE CALLED FOR OVER UPPER CABINETS, EXTEND 1" PAST FRONT EDGE OF MILLWORK.
4. NO PLASTIC HARDWARE, BRACKETS OR CLIPS WILL BE ACCEPTED.
5. ALL DRAWERS SHALL BE ON HEAVY DUTY FULL EXTENSION METAL GLIDES WITH SOFT CLOSERS UNLESS NOTED OTHERWISE.
6. USE CONCEALED CABINET HINGES UNLESS NOTED OTHERWISE.
7. MILLWORK SHALL BE PER THE QUALITY AND GRADE CONSTRUCTION STANDARDS AS SPECIFIED IN THE PROJECT MANUAL. STRICT ADHERENCE TO THIS STANDARD SHALL BE ENFORCED. ANY DEVIATIONS FROM THIS BASE STANDARD, IF NOT SPECIFICALLY SHOWN WITHIN THESE DRAWINGS, WILL NOT BE ACCEPTED.
8. ALL SURFACES EXPOSED TO VIEW, INCLUDING THOSE SURFACES EXPOSED TO VIEW WHILE IN A SEATED POSITION, SHALL HAVE A FINISHED SURFACE TO MATCH OTHER ADJACENT FINISHED SURFACES.
9. ALL COUNTERTOPS TO BE CONSTRUCTED OF SOLID SURFACE WITH 1/4" RADIUS QUARTER ROUND EDGE DETAIL UNLESS NOTED OTHERWISE.
10. ALL CABINET INTERIORS TO BE FINISHED WITH MELAMINE COATING.
11. ALL CABINET HARDWARE TO BE BRUSHED NICKEL FINISH.
12. PROVIDE 1"-1 1/2" FILLER PANEL AT UPPER AND LOWER CABINERY WHERE ADJACENT TO WALL. COORDINATE WIDTH OF FILLER PANEL WITH DEPTH OF DOOR HARDWARE SELECTED.

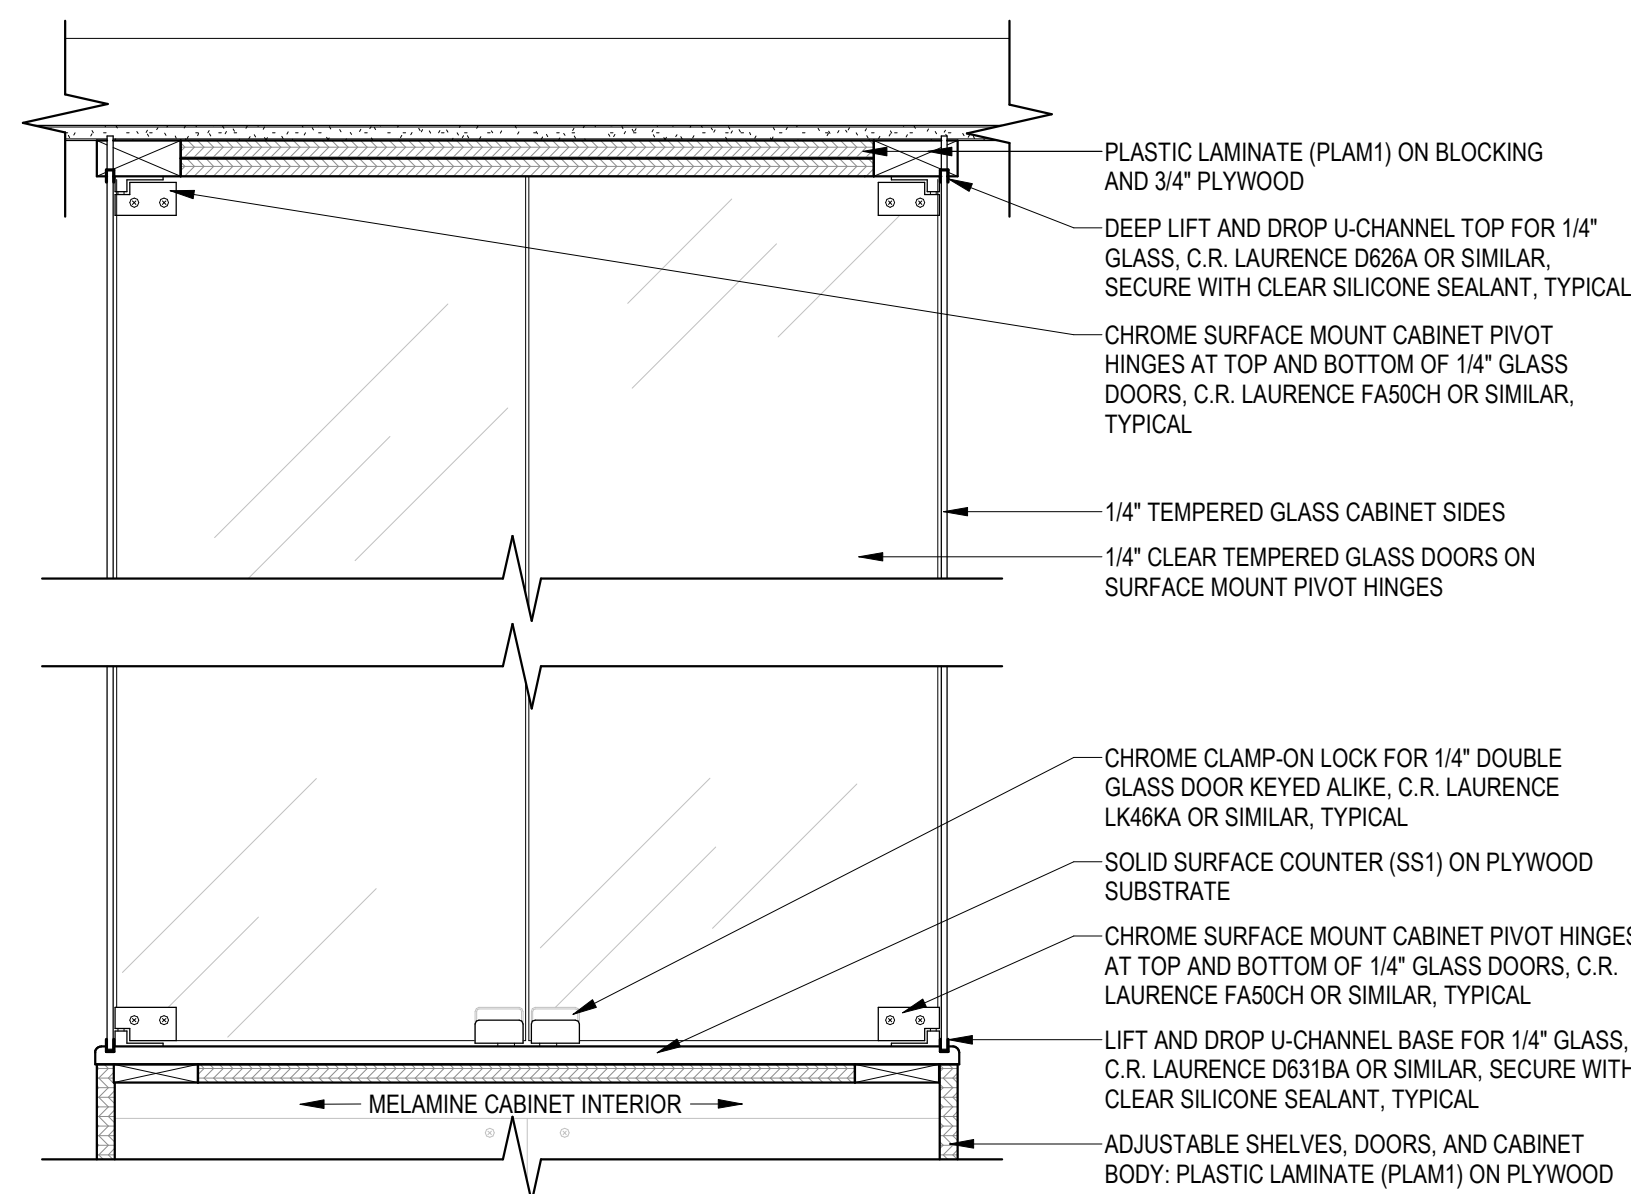


14 MILLWORK SECTION AT DISPLAY CASE DOORS
1 1/2" = 1'-0" 1/2 AE-301

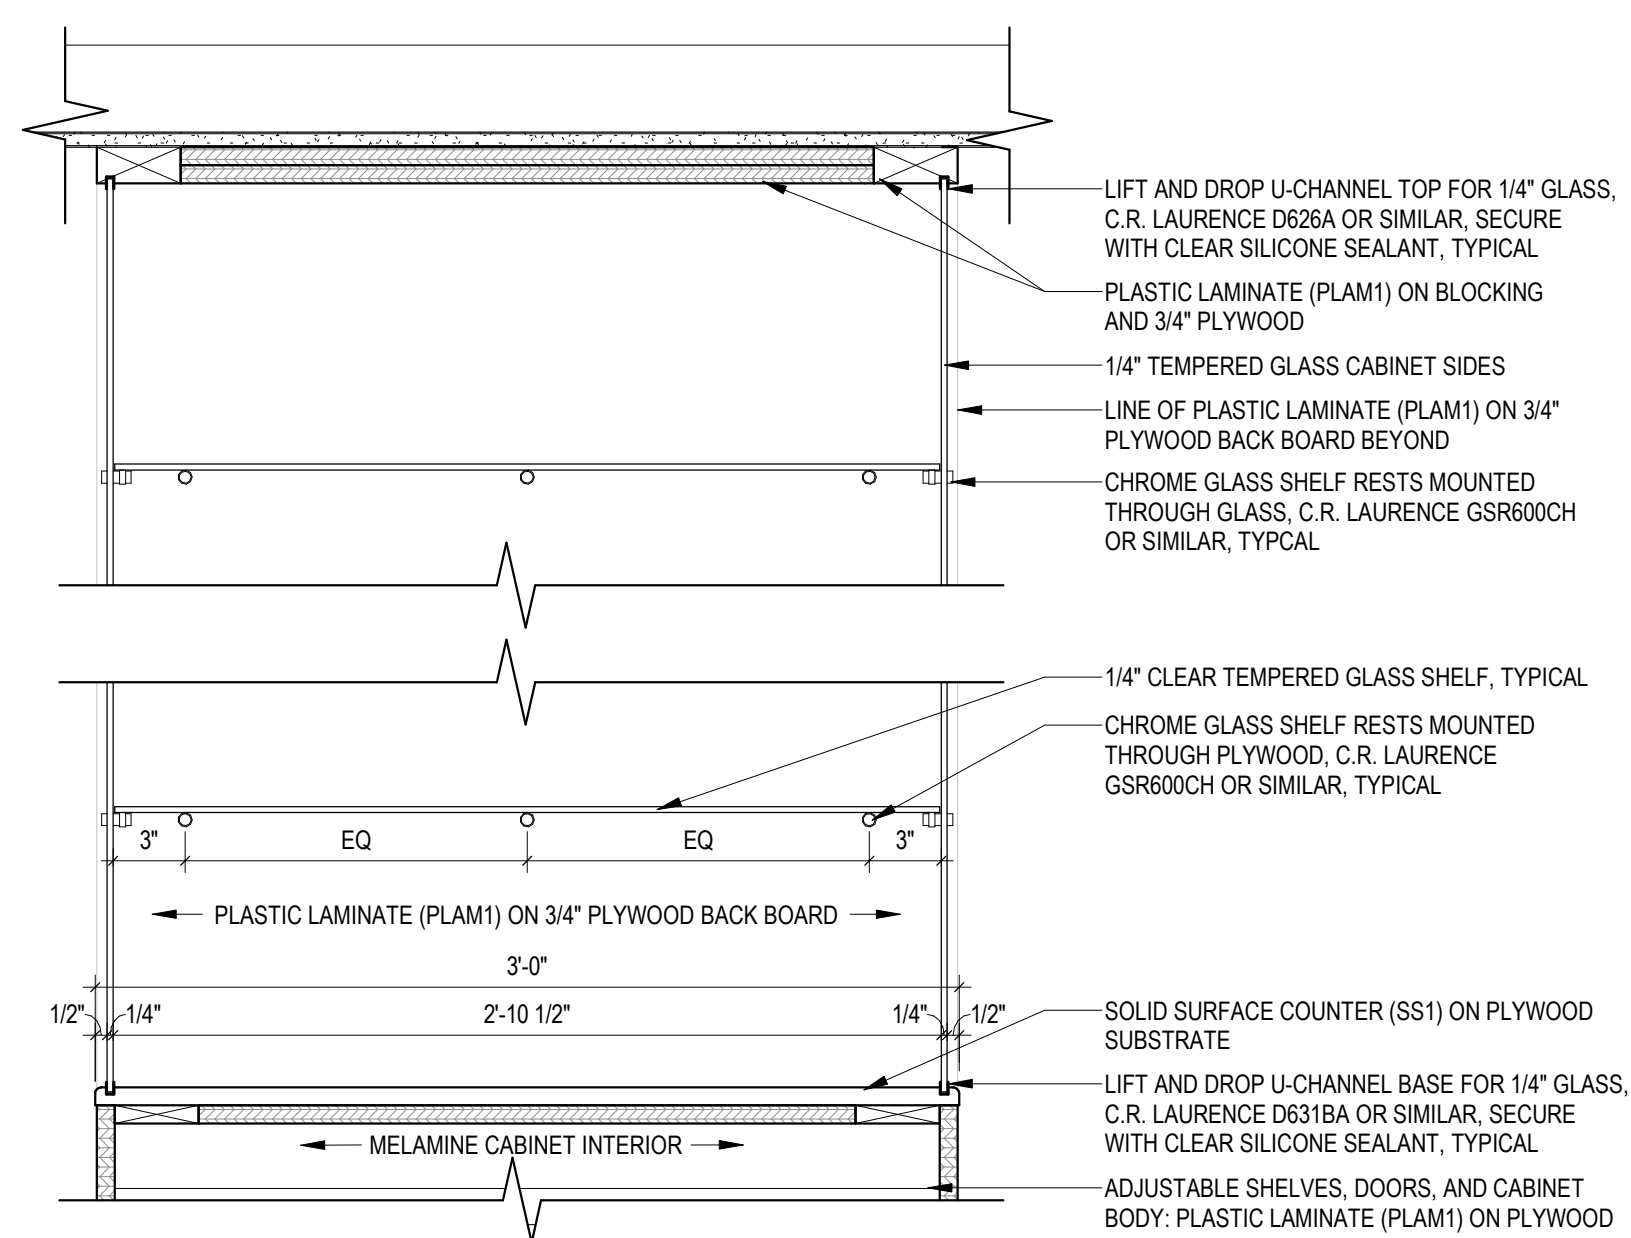


13 MILLWORK SECTION AT DISPLAY CASE SHELVES
1 1/2" = 1'-0" 1/2 AE-301

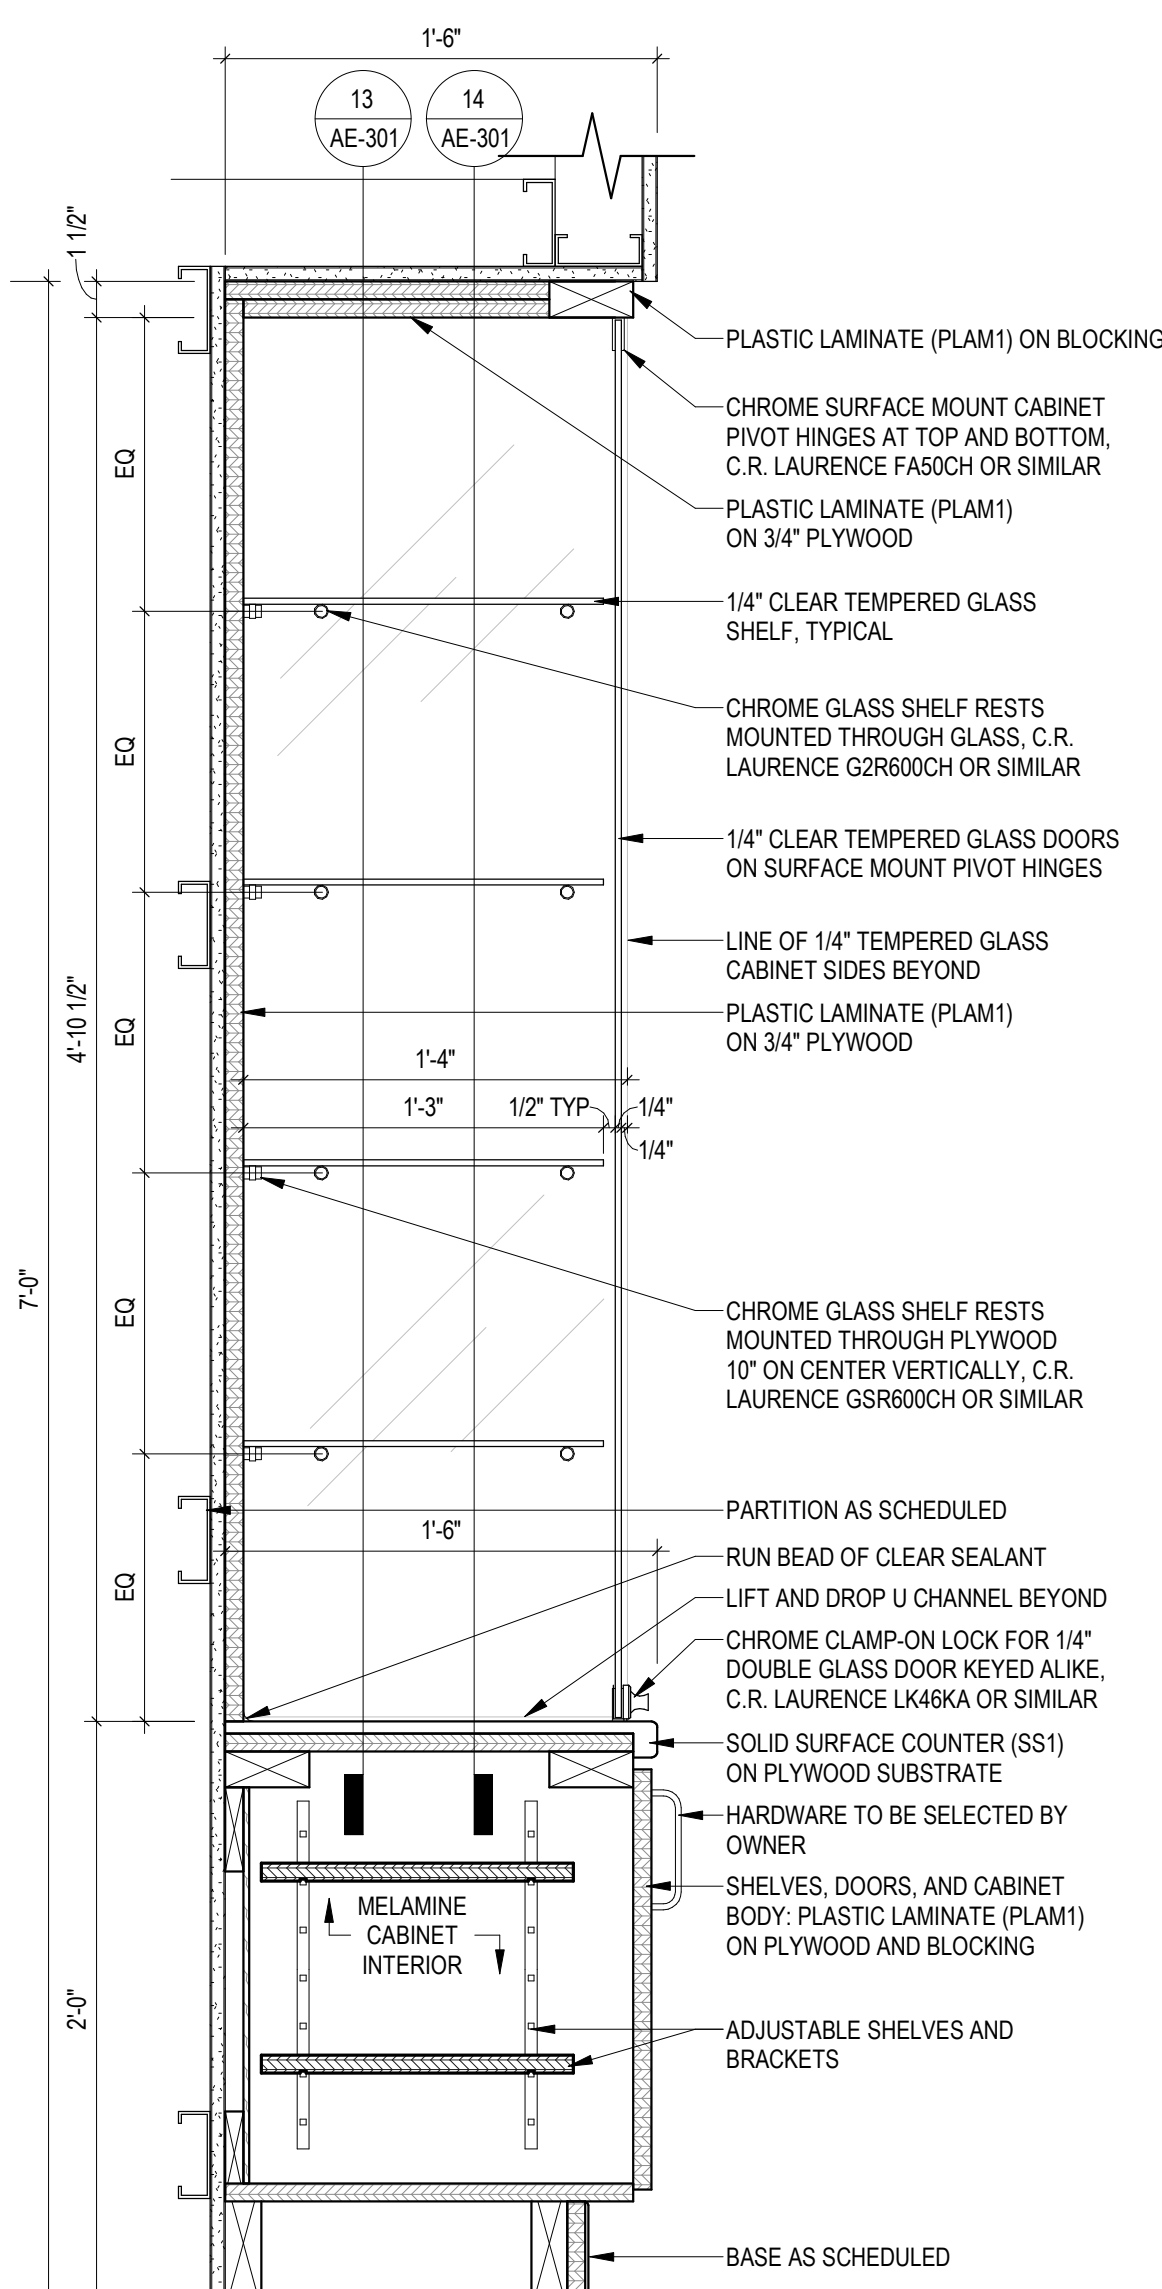


12 MILLWORK SECTION AT DISPLAY CASE
1 1/2" = 1'-0" 1/2 AE-300

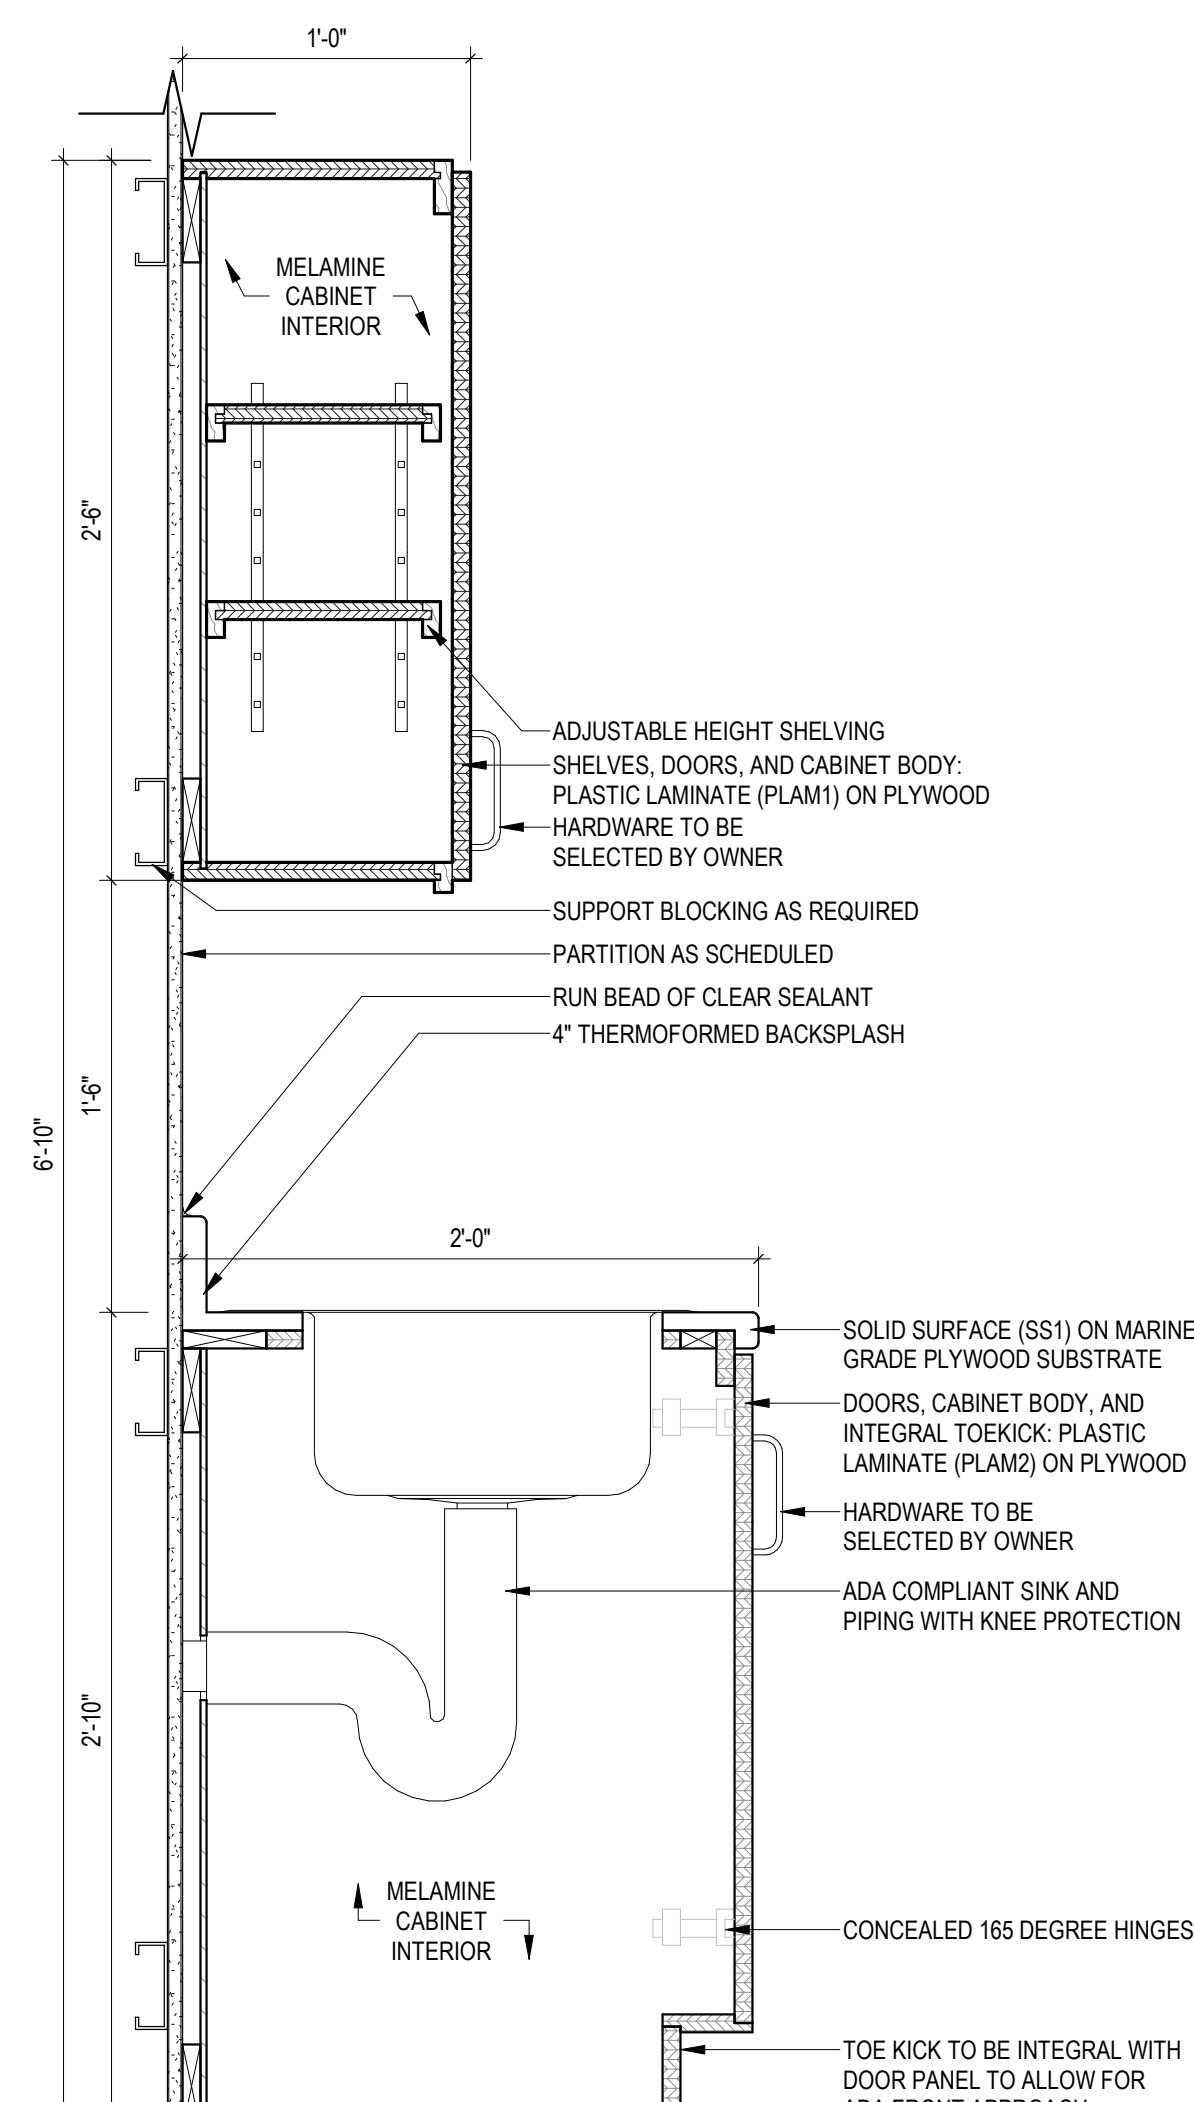


11 MILLWORK SECTION AT SINK
1 1/2" = 1'-0" 6/ AE-300

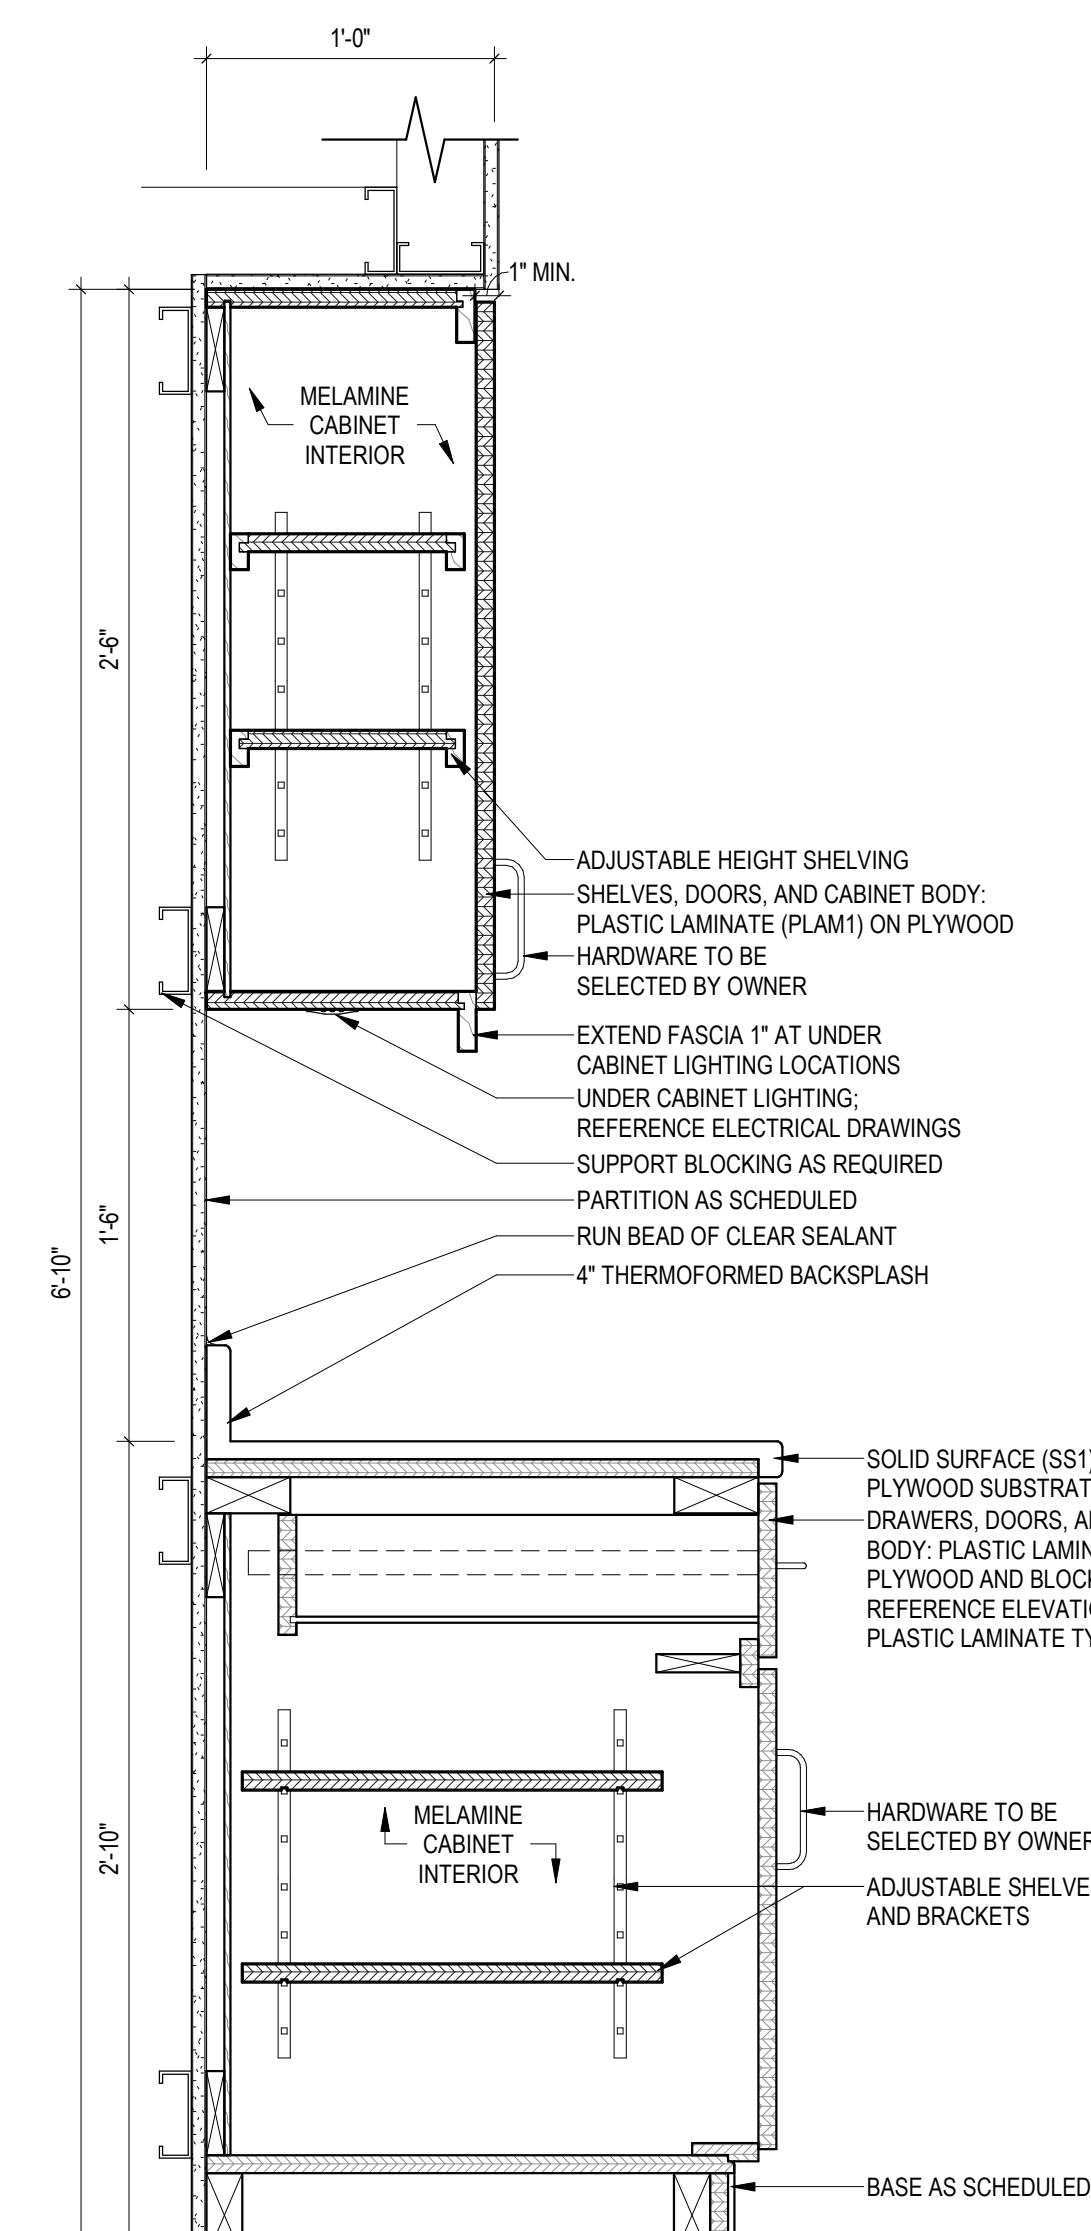


10 MILLWORK SECTION
1 1/2" = 1'-0" 2/ AE-300

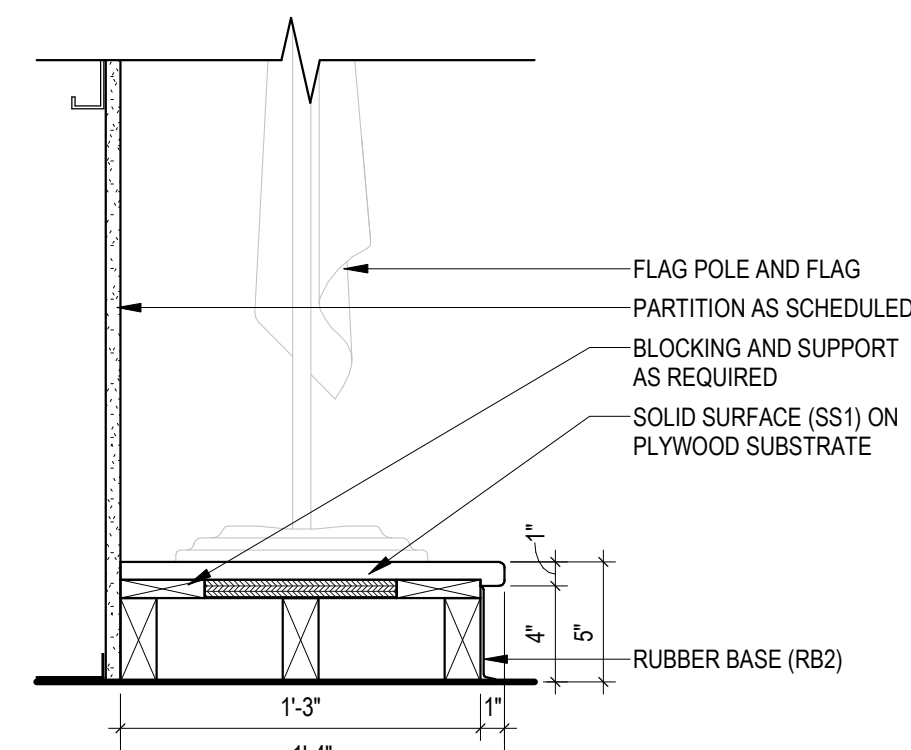


9 MILLWORK SECTION AT FLAG STAGE
1 1/2" = 1'-0" 1/ AE-300

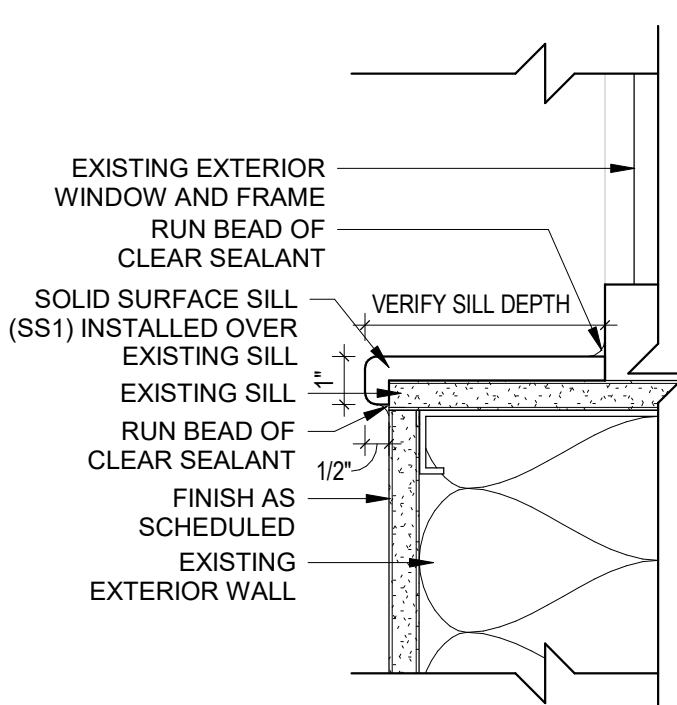


8 WINDOW SILL DETAIL
3\"/>

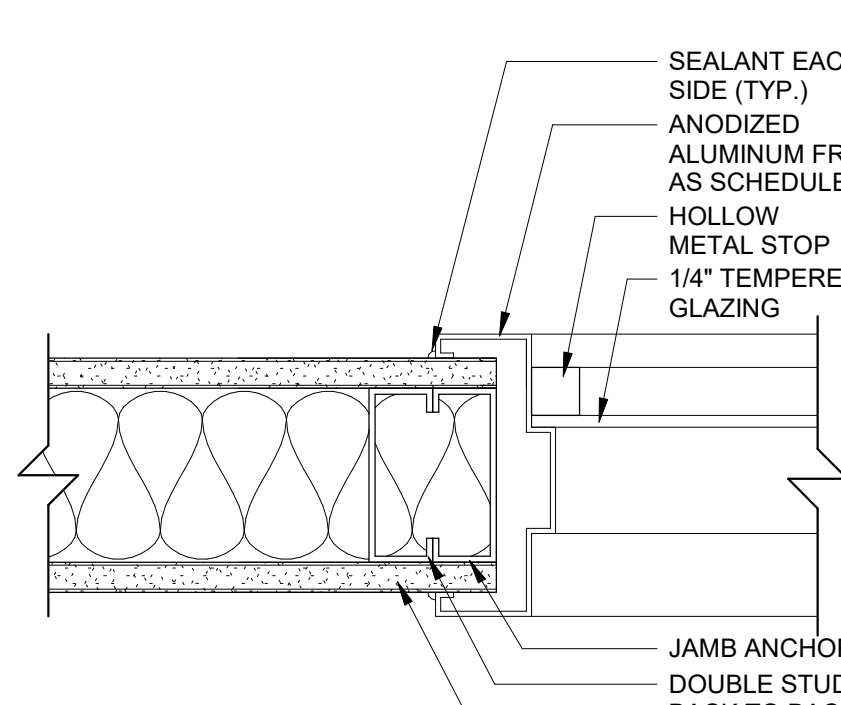


7 WINDOW JAMB DETAIL
3\"/>

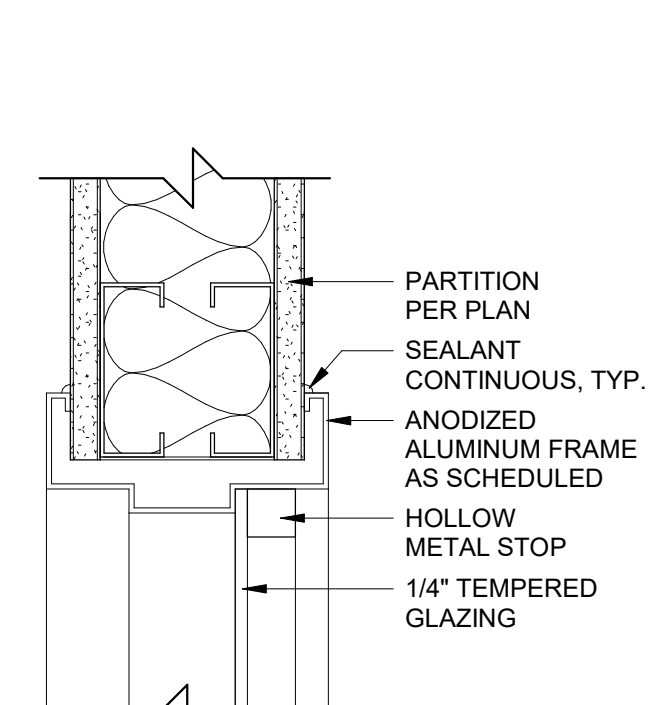


6 WINDOW HEAD DETAIL
3\"/>

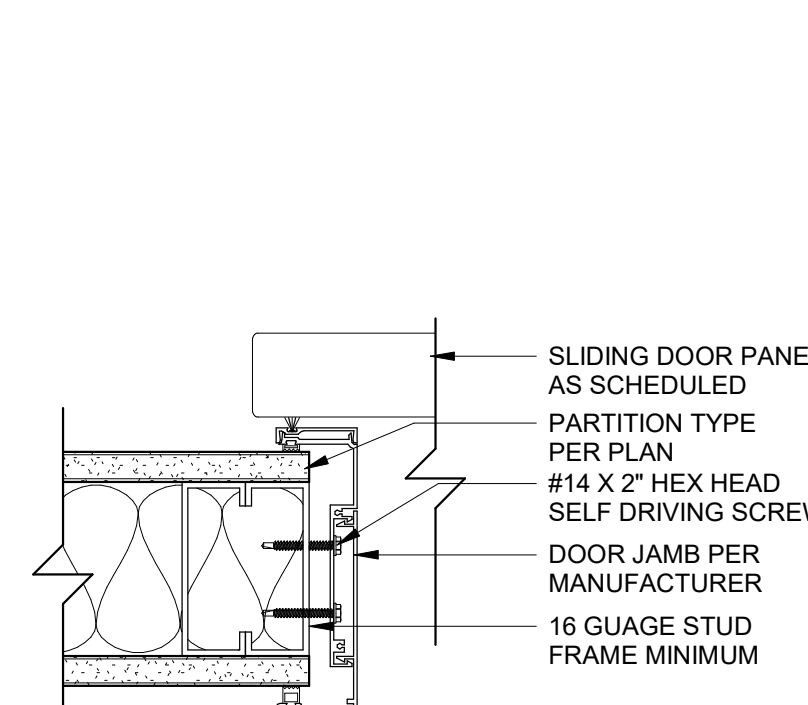


5 DOOR JAMB DETAIL - SLIDING DOOR
3\"/>

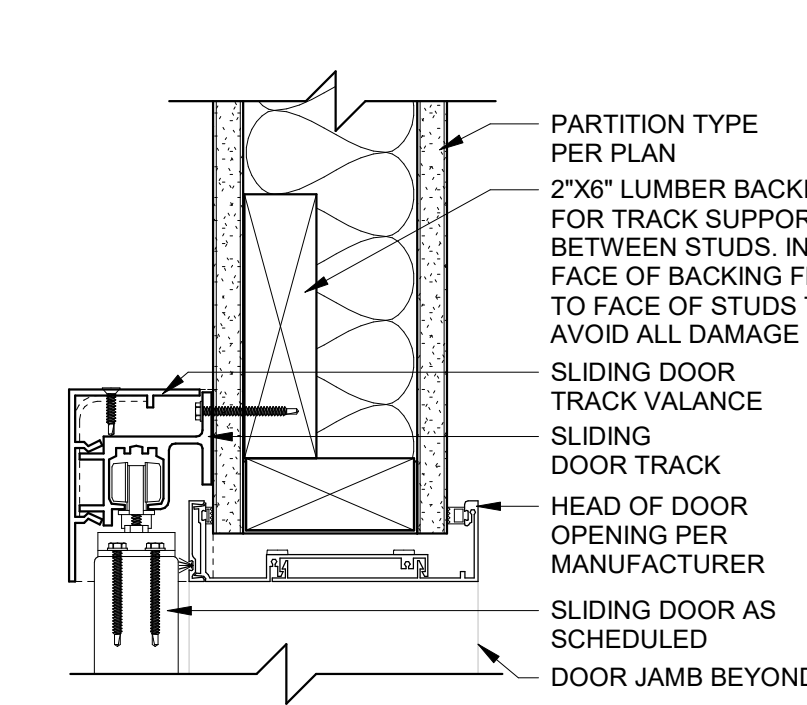


4 DOOR HEAD DETAIL - SLIDING DOOR
3\"/>

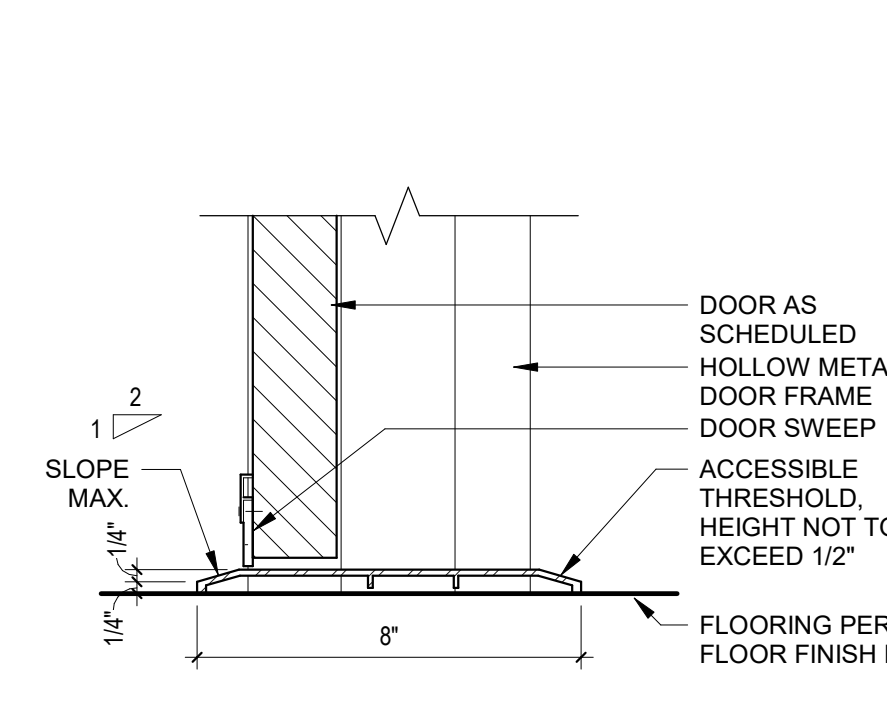

3 DOOR THRESHOLD DETAIL
3\"/>

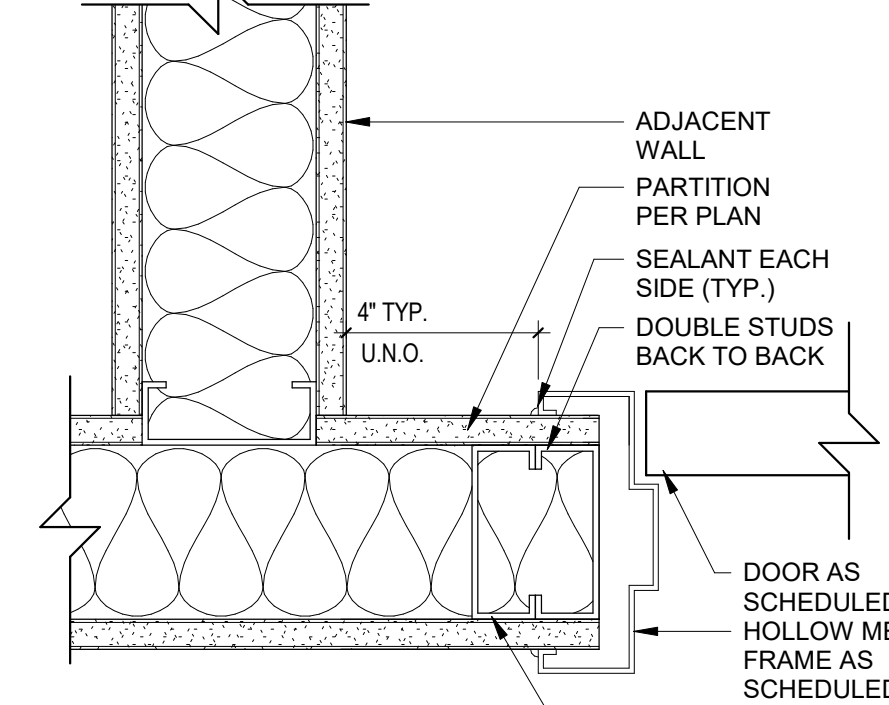

2 DOOR JAMB DETAIL
3\"/>

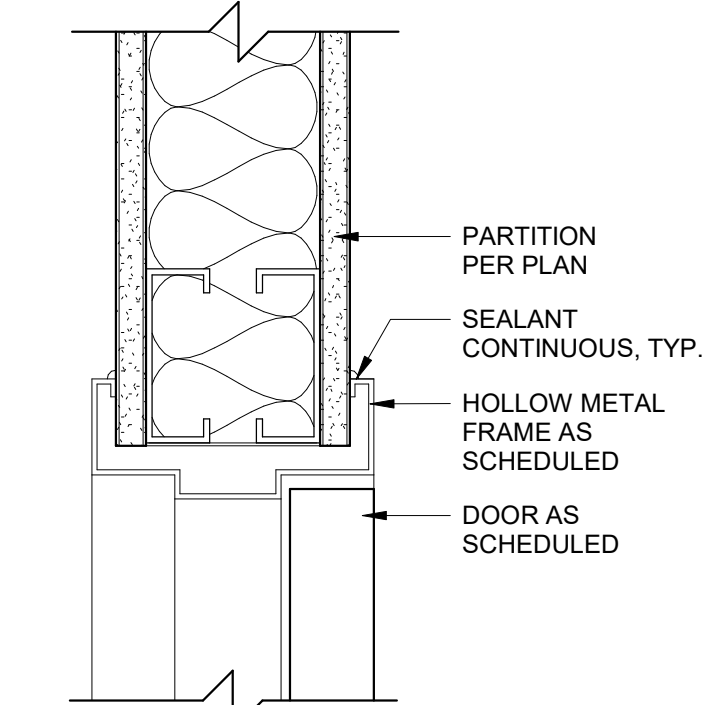

1 DOOR HEAD DETAIL
3\"/>

6/10/2021 3:44:45 PM

No.	REVISION DESCRIPTION	DATE

ARCHITECT / ENGINEER:
SPUR DESIGN

SPUR SBBL COLLABORATIVE JV, INC
100 N. STONE AVENUE, STE 1102
TUCSON, AZ 85701
(405) 842-6100
IL ARCH. LICENSE NO.: 001023503 EXP. 11/30/22
IL MECH. ENGR. LICENSE NO.: 062.071715 EXP. 11/30/21
IL ELEC. ENGR. LICENSE NO.: 062.072296 EXP. 11/30/21

MECH / ELEC / PLUMB / TECH ENGINEER
SPUR DESIGN
10200 KING STREET, SUITE 350
OVERLAND PARK, KS 66210
(913) 369-7200

STAMP:

Drawing Title
ARCHITECTURAL DETAILS

Project Title
HINES FINANCE CENTER

Location STATION 201, BLDG 215, STE 200X
1ST AVENUE NORTH 22ND STREET
HINES, IL 60141

Date 06/14/2021

Checked TAB

Drawn SNP

Project Number
201VB3032

Drawing Number
AE-301

Drawing # 11 OF 29

FULLY SPRINKLERED
100% DESIGN

Veterans Benefits Administration
 U.S. Department of Veterans Affairs

HAZARD CLASSIFICATION LEGEND:

	LIGHT HAZARD (0.10 GPM/FT² OVER 1500 FT² WITH 100 GPM EXTERIOR HOSE DEMAND)
	ORDINARY HAZARD 1 (0.15 GPM/FT² OVER 1500 FT² WITH 250 GPM EXTERIOR HOSE DEMAND)
	OUT OF SCOPE AREA

FIRE PROTECTION GENERAL NOTES:

- A. THE DESIGN AND INSTALLATION OF THE FIRE PROTECTION, FIRE SUPPRESSION SYSTEM MUST BE IN ACCORDANCE WITH U.S. DEPARTMENT OF VETERANS AFFAIRS FIRE PROTECTION DESIGN MANUAL, SEVENTH EDITION, DECEMBER 2015; NFPA 13: STANDARD FOR THE INSTALLATION OF SPRINKLER SYSTEMS, 2019 EDITION; NFPA 14: STANDARD FOR THE INSTALLATION OF STANDPIPE AND HOSE SYSTEMS, 2019 EDITION; IFC, 2018 EDITION, SECOND PRINTING, AND ALL ERRATUM WITH SPECIFIC PROVISIONS IN THE CHICAGO MUNICIPAL BUILDING CODE, TITLE 14F.
- B. THIS INFORMATION HAS BEEN PREPARED TO PROVIDE GUIDANCE FOR BIDDING. THE FIRE PROTECTION CONTRACTOR SHALL BE FULLY RESPONSIBLE FOR PROVIDING A COMPLETE AND FULLY OPERABLE SYSTEM WHICH SHALL BE IN STRICT ACCORDANCE WITH PROJECT SPECIFICATIONS AND APPLICABLE CODES AND STANDARDS. THE WORK THAT IS INDICATED IN THIS DOCUMENT IS AN OVERVIEW OF THE PROJECT. INTENDED TO ESTABLISH THE MINIMUM SCOPE REQUIREMENTS FOR THE PROJECT AS WELL AS THE CONTRACTOR'S RESPONSIBILITIES. THE CONTRACTOR SHALL SUBMIT A COMPLETE SET OF WORKING DRAWINGS, EQUIPMENT, AND CALCULATIONS TO THE OWNER'S REPRESENTATIVE AND AHI FOR REVIEW AND APPROVAL PRIOR TO FABRICATION AND INSTALLATION WITH THEIR ENGINEER'S SEAL.
- C. PRIOR TO BEGINNING ANY CONSTRUCTION, THE CONTRACTOR SHALL BE RESPONSIBLE FOR VERIFICATION OF ALL DIMENSIONS, MEASUREMENTS AND LOCATIONS OF EXISTING FACILITIES, UTILITIES, EQUIPMENT AND OTHER EXISTING CONDITIONS WHICH MAY AFFECT CONSTRUCTION. HOWEVER, IN THE EVENT OF DISCREPANCIES BETWEEN THE DRAWINGS AND ACTUAL FIELD CONDITIONS, CONTACT THE CONTRACTING OFFICE IMMEDIATELY.
- D. SPRINKLER CONTRACTOR SHALL COORDINATE LOCATIONS OF FIRE PROTECTION COMPONENTS INCLUDING PIPING, ALARMS, DRAINS, SPRINKLERS, TEST POINTS, ETC., WITH ALL ARCHITECTURAL, STRUCTURAL, MECHANICAL AND ELECTRICAL COMPONENTS. OBSTRUCTIONS TO SPRINKLER DISCHARGE SHALL BE CONSIDERED DURING INSTALLATION. DO NOT INSTALL SPRINKLER PIPING BELOW EQUIPMENT OR WITHIN CLEARANCE SPACES FOR MECHANICAL AND ELECTRICAL EQUIPMENT. SPRINKLERS SHALL BE INSTALLED UNDER OBSTRUCTIONS IN ACCORDANCE WITH NFPA 13.
- E. THE SPRINKLER SYSTEM MUST BE ZONED BY SMOKE COMPARTMENT. REFER TO THE LIFE SAFETY SHEET FOR LOCATION OF SMOKE COMPARTMENT BOUNDARY.
- F. MATERIALS AND ACCESSORIES NECESSARY MUST BE INSTALLED IN ACCORDANCE WITH THE APPLICABLE NFPA CODES AND STANDARDS, PROJECT SPECIFICATIONS, AND BE UL LISTED OR FM APPROVED FOR FIRE PROTECTION USE, UNLESS NOTED.
- G. ALL VALVES INSIDE TO BE PROVIDED WITH ELECTRONIC TAMPER SWITCHES WIRED TO THE FACU. VALVES IN NORMAL CLOSED POSITION SHALL BE PROVIDED WITH TAMPER TO ACTIVATE IN THREE TURNS OR LESS. ALL VALVES OUTSIDE TO BE SUPERVISED WITH LOCK AND CHAIN.
- H. ALL HANGERS MUST BE PROVIDED AND INSTALLED IN ACCORDANCE WITH NFPA 13 AND PROJECT SPECIFICATIONS. LOCATION AND INSTALLATION OF PIPE SUPPORTS (HANGERS, VERTICAL RESTRAINTS AND GUIDES) SHALL MEET THE REQUIREMENTS OF NFPA 13 AND THE SPECIAL LISTING REQUIREMENTS (IF APPLICABLE) OF THE PIPE AND SUPPORTS.
- I. THE INSPECTOR'S TEST VALVES MUST BE LOCATED NO MORE THAN 7 FEET AFF.
- J. APPLICABLE UL CONSTRUCTION DETAILS AND SYSTEMS SHALL BE USED WHERE FIRE RATED BARRIERS ARE PENETRATED BY SPRINKLER PIPING.
- K. ALL VALVES (DRAINS, INSPECTOR'S TEST, CONTROL) MUST BE IDENTIFIED AS REQUIRED BY NFPA 13.
- L. PIPING MUST BE ARRANGED FOR FLUSHING. READILY REMOVABLE FITTINGS MUST BE PROVIDED AT THE END OF ALL CROSS MAINS.
- M. ALL PENDENT SPRINKLERS MUST BE INSTALLED IN THE CENTER OF THE CEILING TILES.
- N. DRAINS MUST BE LOCATED TO PROVIDE DRAINAGE IN ACCORDANCE WITH NFPA 13. ALL DRAINS AND TEST CONNECTIONS MUST DISCHARGE TO THE EXTERIOR OF THE BUILDING ON TO A SPLASH BLOCK OR PAVEMENT, AND SHALL NOT DISCHARGE ACROSS PATHS OF EGRESS.
- O. ALL SPRINKLER SYSTEM ALARM INITIATING AND SUPERVISORY DEVICES MUST BE CONNECTED TO THE FIRE ALARM SYSTEM.
- P. ADDITIONAL SPRINKLERS MAY BE REQUIRED UNDER DUCT WORK TO PROVIDE ADEQUATE COVERAGE PER NFPA 13.
- Q. A LISTED RELIEF VALVE MUST BE PROVIDED IN ACCORDANCE WITH NFPA 13, SECTION 8.1.2 FOR THE SPRINKLER SYSTEM.
- R. AN AIR VENT MUST BE PROVIDED IN ACCORDANCE WITH NFPA 13, SECTION 8.1.5 AND SECTION 16.7 FOR THE SPRINKLER SYSTEM.
- S. THIS BUILDING WILL HAVE A WET PIPE AUTOMATIC SPRINKLER SYSTEM WHICH WILL REQUIRE ALL AREAS OF THE BUILDING TO BE MAINTAINED ABOVE 40° F.
- T. PROVIDE SPRINKLER PROTECTION WITHIN ALL COMBUSTIBLE CONCEALED SPACES.

KEYNOTES

- F1. CONTRACTOR TO RELOCATE SPRINKLER HEADS AND ASSOCIATED PIPING AS NECESSARY TO MEET NEW HAZARD SPECIFICATIONS, SPACE LAYOUTS, AND SAFETY NEEDS PER NFPA 13 AND BUILDING CODE GUIDELINES.

FULLY SPRINKLERED
100% DESIGN

No.	REVISION DESCRIPTION	DATE

ARCHITECT / ENGINEER:



SPUR SBBL COLLABORATIVE JV, INC
100 N. STONE AVENUE, STE 1102
TUCSON, AZ 85701
(405) 842-6100

IL ARCH. LICENSE NO.: 001023503 EXP. 11/30/22
IL MECH. ENGR. LICENSE NO.: 062.071715 EXP. 11/30/21
IL ELECT. ENGR. LICENSE NO.: 062.072296 EXP. 11/30/21

MECH / ELEC / PLUMB / TECH ENGINEER
SPUR DESIGN
11020 KING STREET, SUITE 350
OVERLAND PARK, KS 66210
(913) 369-7200

STAMP:



Drawing Title
LEVEL 2 - FIRE PROTECTION PLAN

VA Health Care System Approval:

Project Title
HINES FINANCE CENTER

Location **STATION 201, BUILDING 215
1ST AVENUE NORTH 22ND STREET
HINES, IL 60141**

Date
06/14/2021

Checked
JRM

Drawn
RDC

Project Number
201VB3032

Drawing Number
FP-100

Drawing # 12 OF 29


Veterans
Benefits
Administration



5/19/2021 8:32:24 AM

VA FORM 08-6231

- DEMOLITION KEYNOTES
- D1 CONTRACTOR TO VERIFY AND DEMOLISH EXISTING AIR DEVICE AND ASSOCIATED ACCESSORIES.
 - D2 CONTRACTOR TO VERIFY AND DISCONNECT HEAT PUMP. REMOVE AND STORE WITH CORRESPONDING THERMOSTAT IN A SECURE LOCATION TO PREVENT ANY DAMAGE PRIOR TO RE-INSTALLATION OF BOX AND THERMOSTAT.
 - D3 CONTRACTOR TO DEMOLISH EXISTING WATER LOOP AND CONDENSATE DRAIN PIPING BACK TO MAIN BRANCH AND CAP.
 - D4 CONTRACTOR TO VERIFY AND DEMOLISH EXISTING DUCTWORK BACK TO MAIN BRANCH AND CAP.
 - D5 HEAT PUMP TO REMAIN IN EXISTING LOCATION.
 - D6 CONTRACTOR TO DEMOLISH EXISTING DUCTWORK BACK TO HEAT PUMP.
 - D7 CONTRACTOR TO VERIFY AND DEMOLISH DUCTWORK BACK TO HEAT PUMP OR MAIN AND CAP.

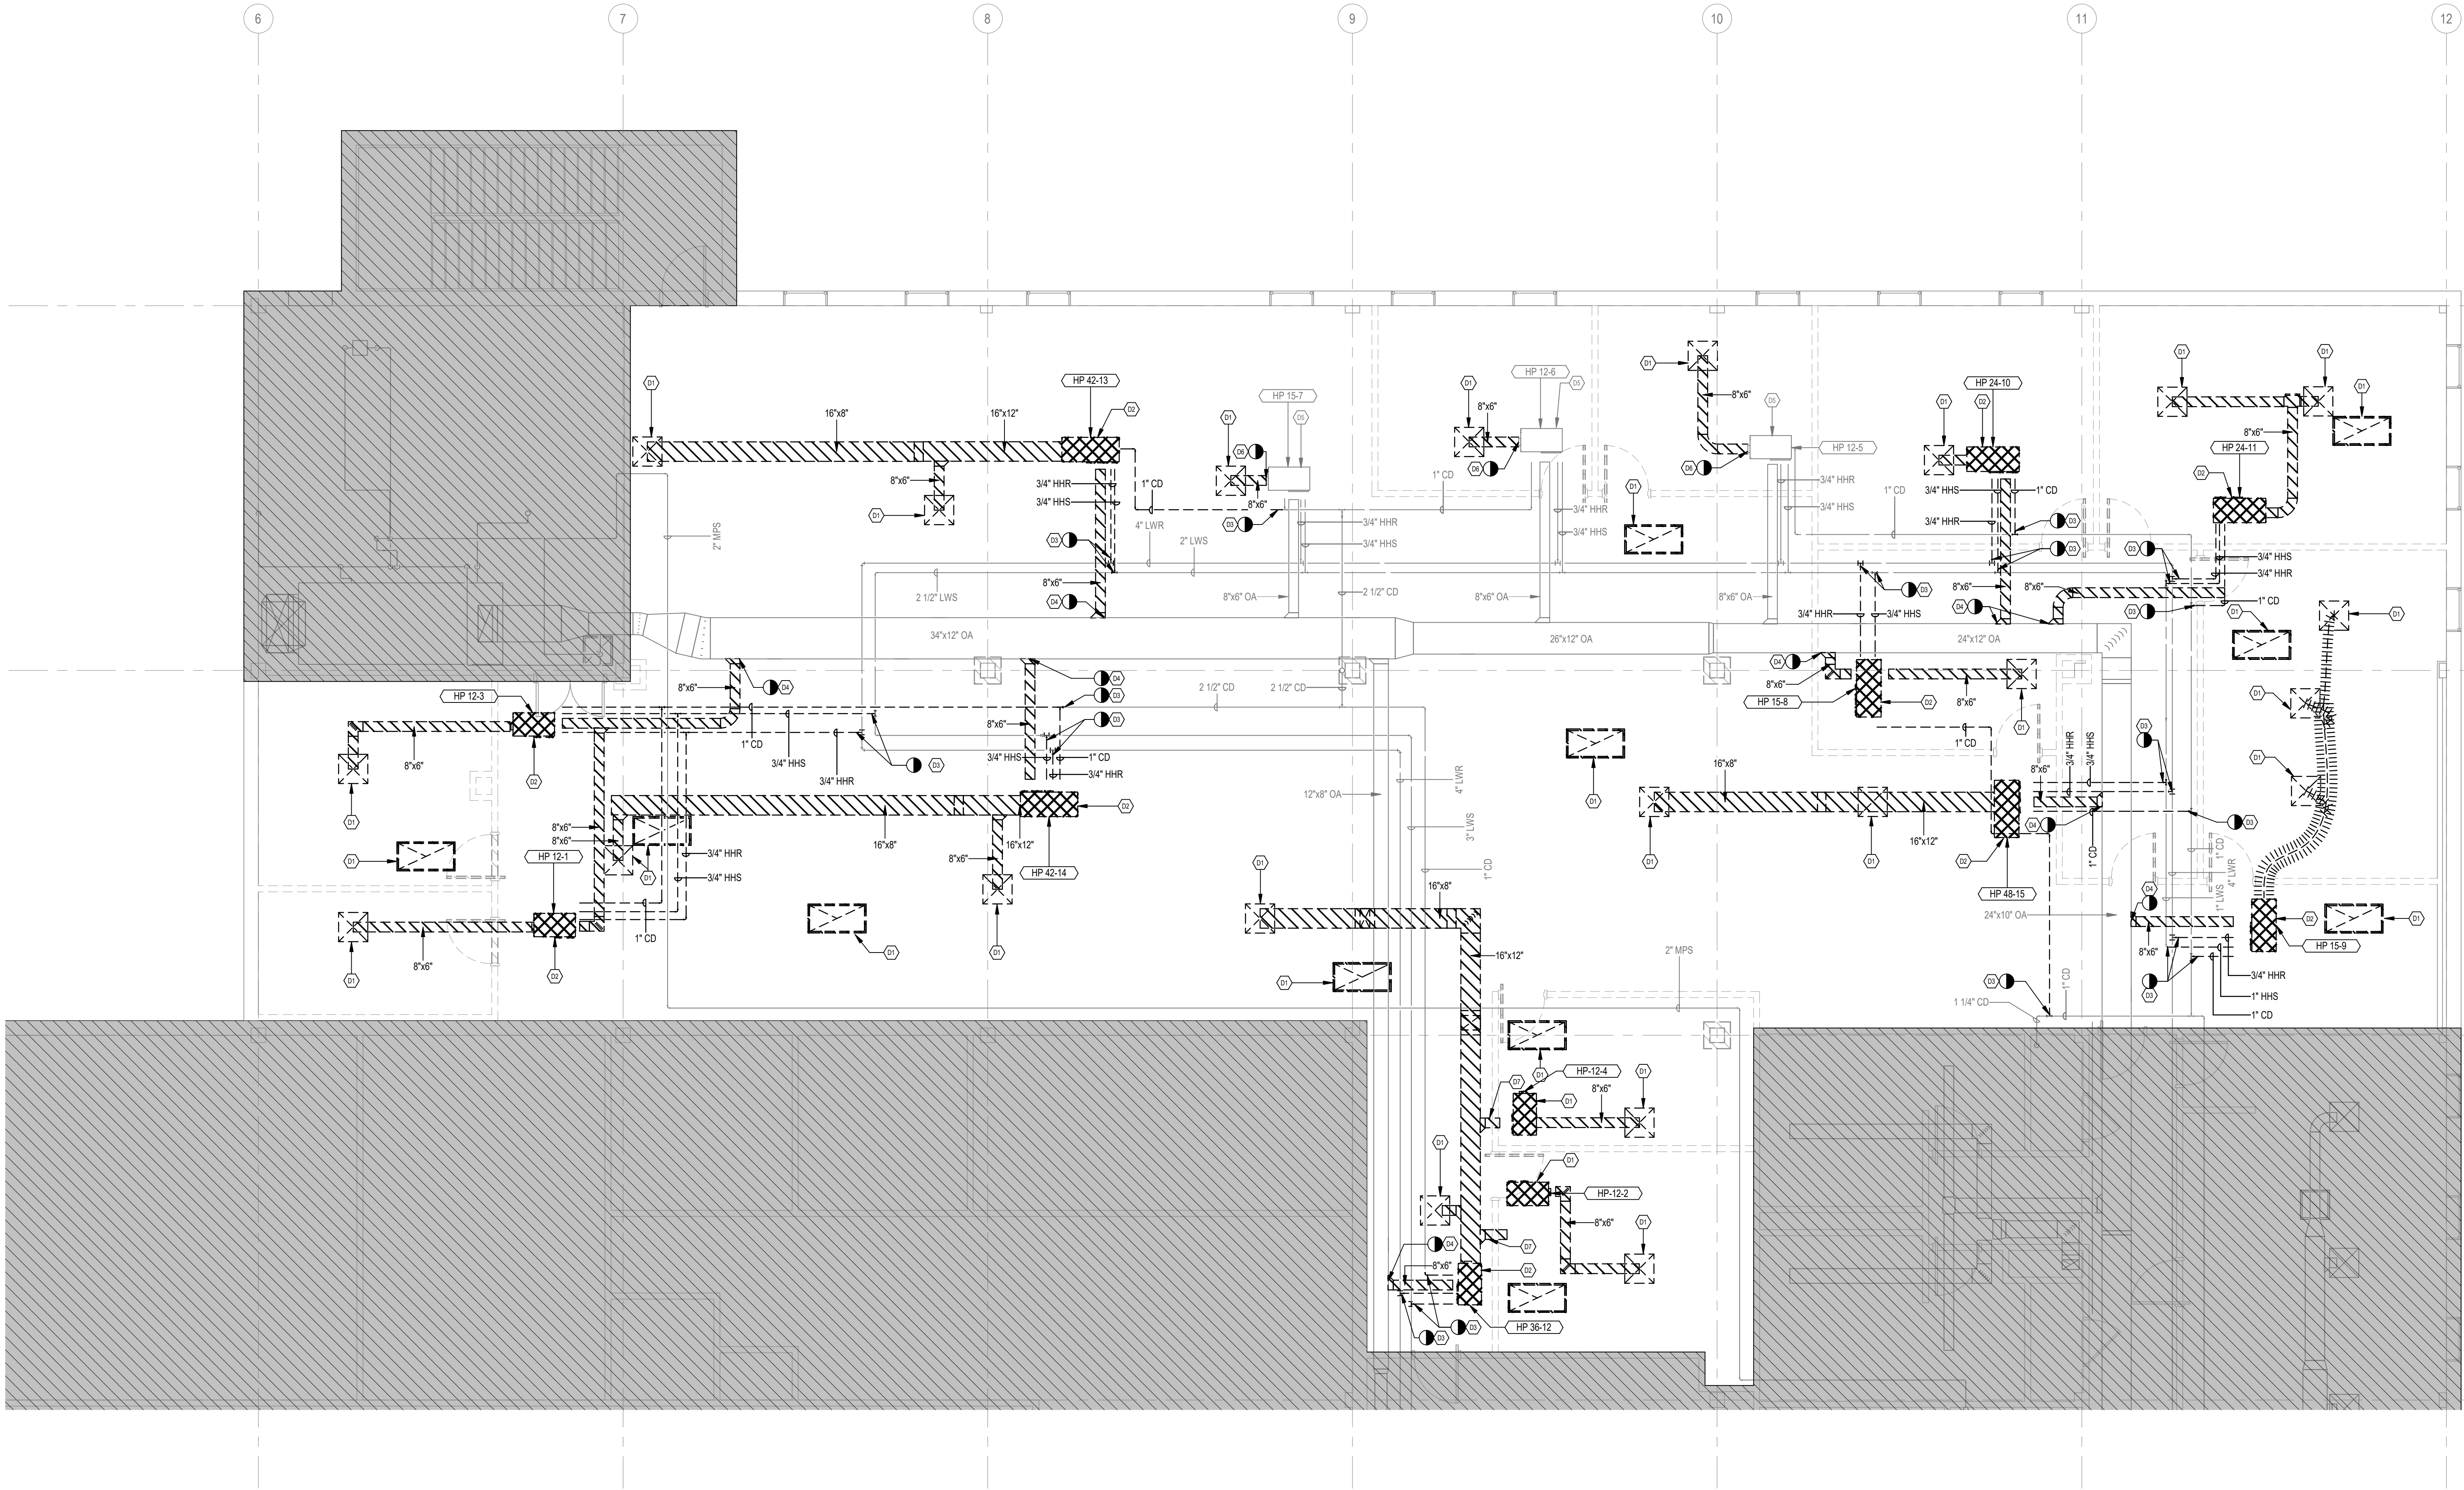

1 LEVEL 2 - MECHANICAL DEMOLITION PLAN
3/16" = 1'-0"

No.	REVISION DESCRIPTION	DATE

ARCHITECT / ENGINEER:



SPUR SBBL COLLABORATIVE JV, INC
100 N. STONE AVENUE, STE 1102
TUCSON, AZ 85701
(405) 842-6100

IL ARCH. LICENSE NO.: 001023503 EXP. 11/30/22
IL MECH. ENGR. LICENSE NO.: 062.071715 EXP. 11/30/21
IL ELECT. ENGR. LICENSE NO.: 062.072296 EXP. 11/30/21

MECH / ELEC / PLUMB / TECH ENGINEER
SPUR DESIGN
11020 KING STREET, SUITE 350
OVERLAND PARK, KS 66210
(913) 369-7200

STAMP:



Drawing Title
LEVEL 2 - MECHANICAL HVAC
DEMOLITION PLAN

VA Health Care System Approval:

Project Title
HINES FINANCE CENTER

Location STATION 201, BUILDING 215
1ST AVENUE NORTH 22ND STREET
HINES, IL 60141

Date
06/14/2021

Checked
JRM

Drawn
RDC

Project Number
201VB3032

Drawing Number
MD-100

Drawing # 14 OF 29

FULLY SPRINKLERED
100% DESIGN


Veterans
Benefits
Administration



5/19/2021 8:32:26 AM

VA FORM 08-6231

KEYNOTES
M1 CONTRACTOR TO RELOCATE THERMOSTAT TO LOCATION SHOWN.

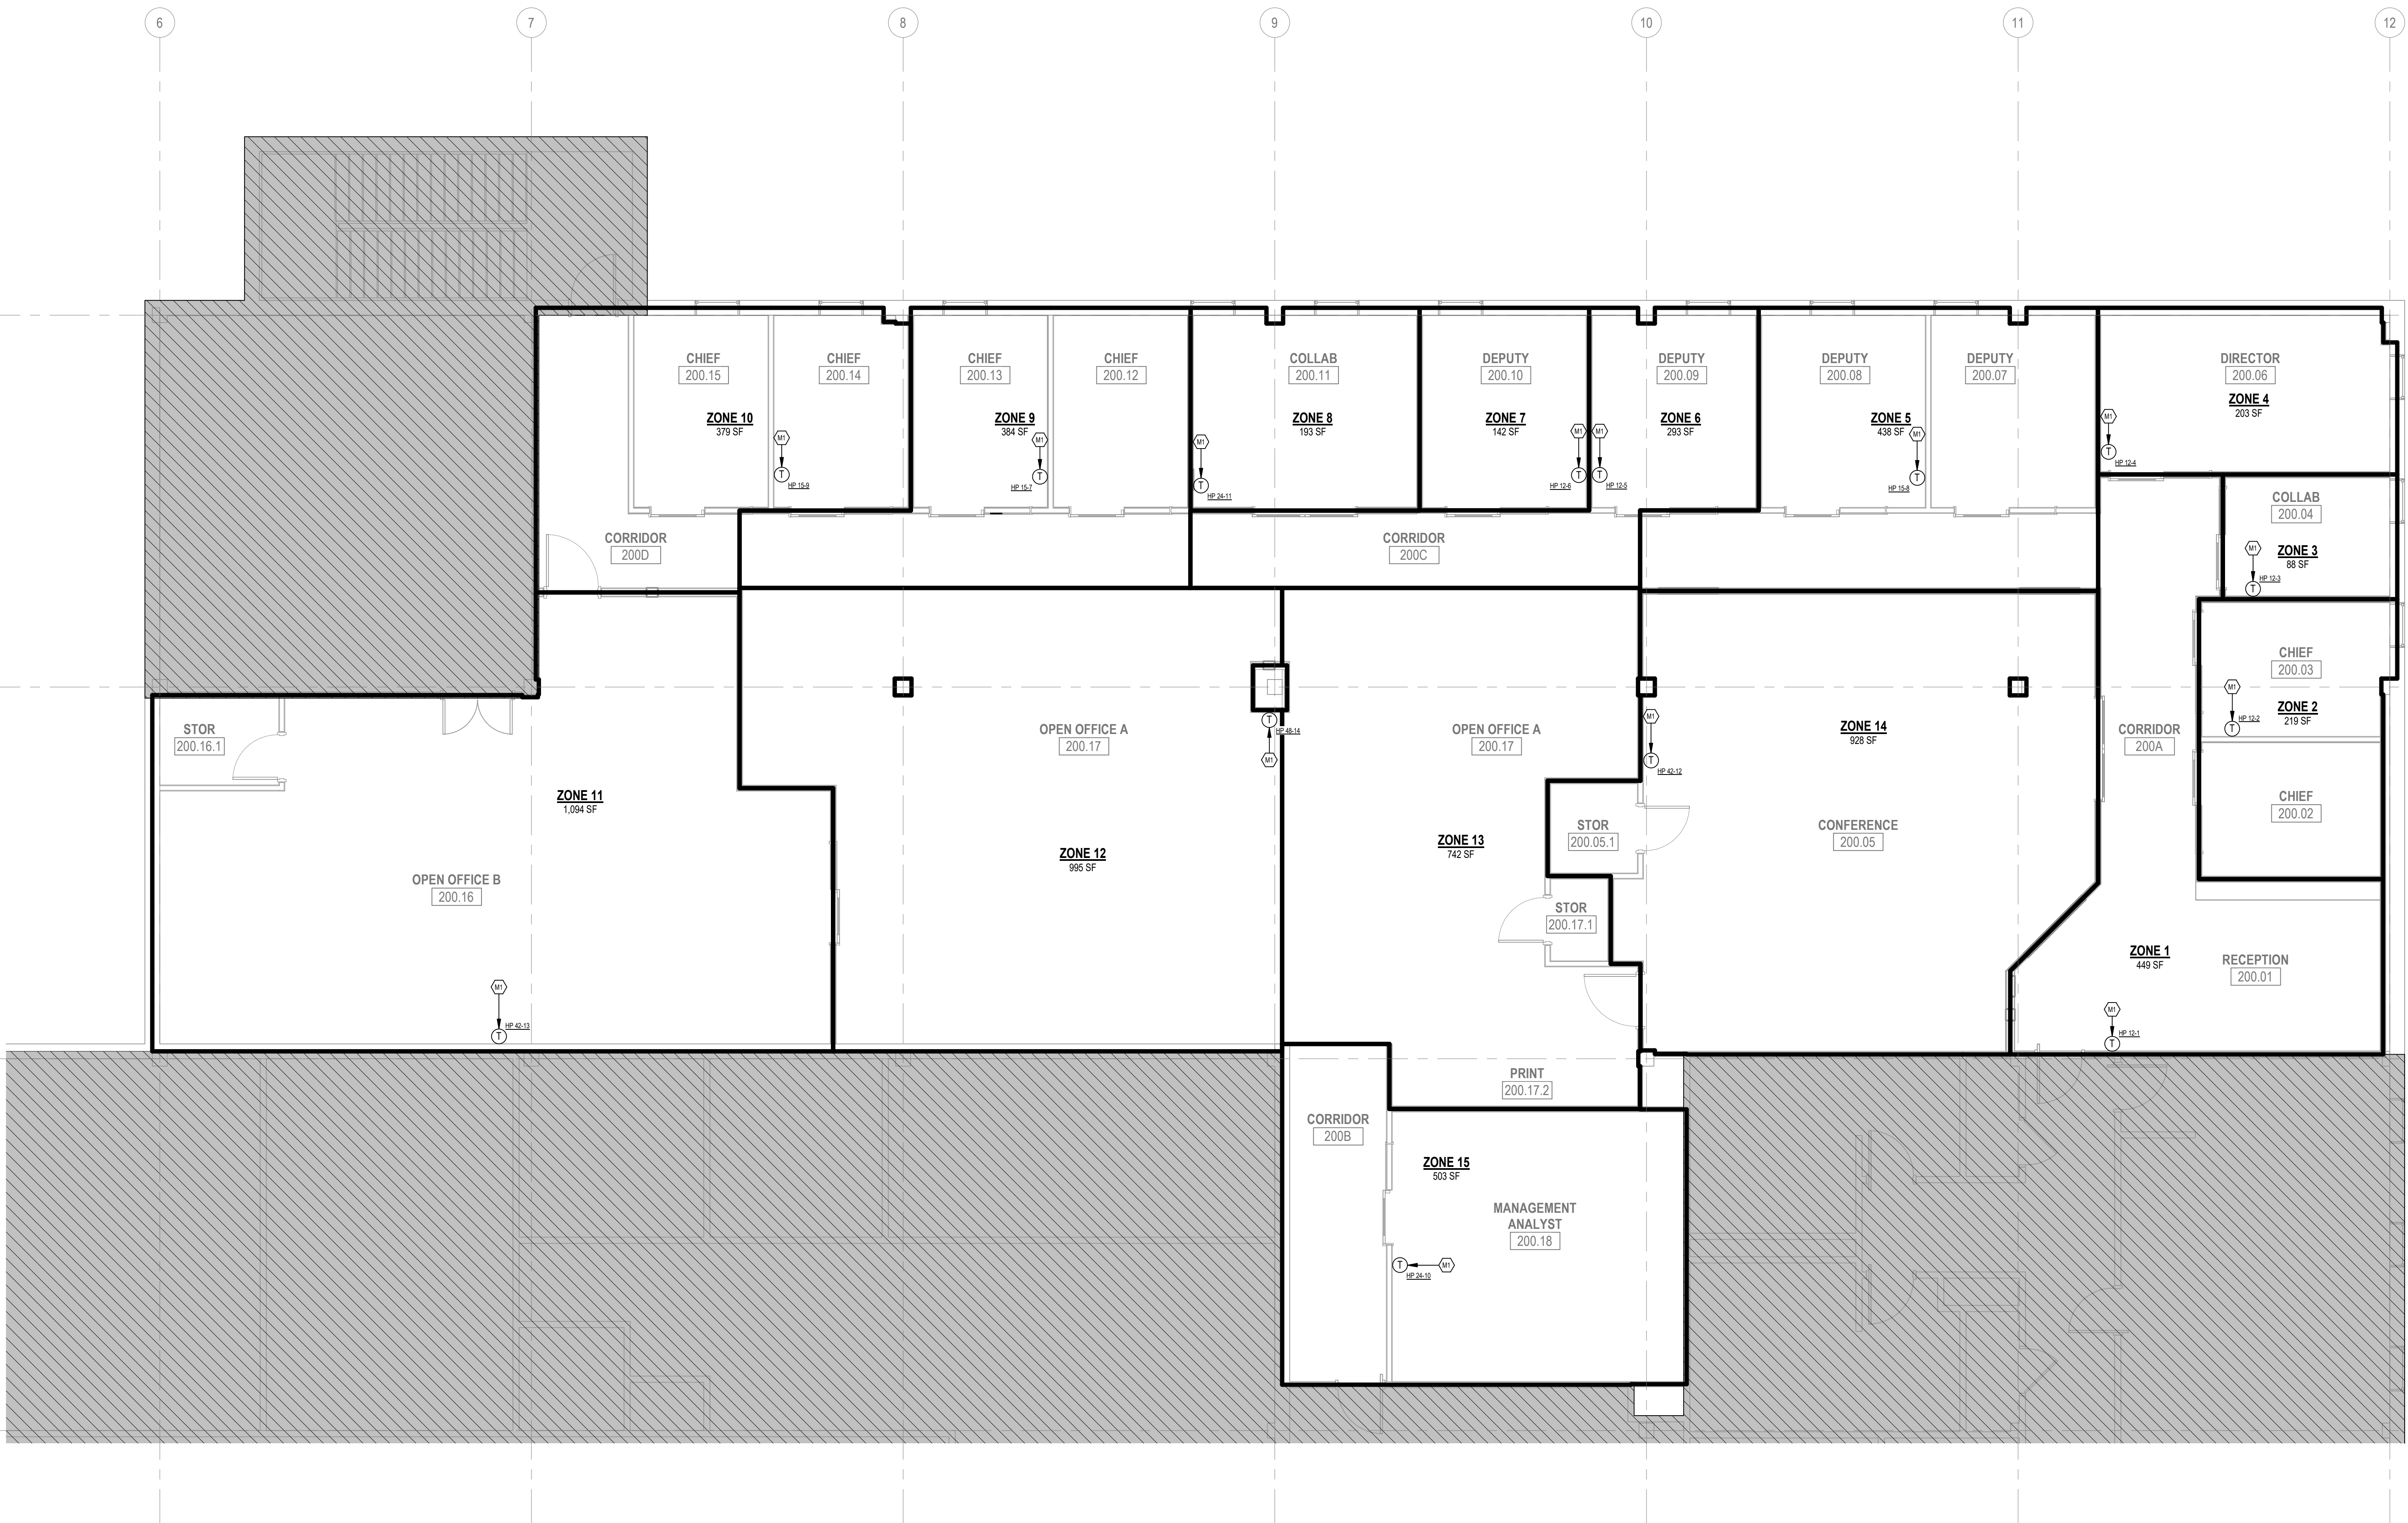

2 LEVEL 2 - MECHANICAL HVAC ZONING PLAN
3/16\"/>

No.	REVISION DESCRIPTION	DATE

ARCHITECT / ENGINEER:



SPUR SBBL COLLABORATIVE JV, INC
100 N. STONE AVENUE, STE 1102
TUCSON, AZ 85701
(405) 842-6100

IL ARCH. LICENSE NO.: 001023503 EXP. 11/30/22
IL MECH. ENGR. LICENSE NO.: 062.071715 EXP. 11/30/21
IL ELECT. ENGR. LICENSE NO.: 062.072296 EXP. 11/30/21

MECH / ELEC / PLUMB / TECH ENGINEER
SPUR DESIGN
11020 KING STREET, SUITE 350
OVERLAND PARK, KS 66210
(913) 369-7200

STAMP:



Drawing Title
LEVEL 2 - MECHANICAL HVAC ZONING PLAN

VA Health Care System Approval:

Project Title
HINES FINANCE CENTER

Location STATION 201, BUILDING 215
1ST AVENUE NORTH 22ND STREET
HINES, IL 60141

Date
06/14/2021

Checked
JRM

Drawn
RDC

Project Number
201VB3032

Drawing Number

MH-100

Drawing # 15 OF 29

FULLY SPRINKLERED
100% DESIGN

Veterans
Benefits
Administration




5/19/2021 8:32:26 AM

EXISTING HEAT PUMP SCHEDULE							
MARK	EQUIPMENT #	MODEL #	HEATING CAPACITY	DESIGN AIRFLOW	OA CFM	VOLTAGE/PHASE	NOTES
HP 12-1	RGSH012EL200CANNZ8N00SSD	190201402	12,000 BTU	205 CFM	50	265/1	LEFT HAND RETURN WITH END DISCHARGE
HP 12-2	RGSH012SR200CANNZ8N00SSD	190201342	12,000 BTU	365 CFM	35	265/1	RIGHT HAND RETURN WITH SIDE DISCHARGE
HP 12-3	RGSH012EL200CANNZ8N00SSD	190201399	12,000 BTU	290 CFM	35	265/1	LEFT HAND RETURN WITH END DISCHARGE
HP 12-4	RGSH012EL200CANNZ8N00SSD	190201386	12,000 BTU	325 CFM	30	265/1	LEFT HAND RETURN WITH END DISCHARGE
HP 12-5	RGSH012EL200CANNZ8N00SSD	190201406	12,000 BTU	460 CFM	25	265/1	LEFT HAND RETURN WITH END DISCHARGE
HP 12-6	RGSH012EL200CANNZ8N00SSD	190201398	12,000 BTU	310 CFM	35	265/1	LEFT HAND RETURN WITH END DISCHARGE
HP 15-7	RGSH015EL200CANNZ8N00SSD	190201449	15,000 BTU	490 CFM	35	265/1	LEFT HAND RETURN WITH END DISCHARGE
HP 15-8	RGSH015EL200CANNZ8N00SSD	190201450	15,000 BTU	620 CFM	50	265/1	LEFT HAND RETURN WITH END DISCHARGE
HP 15-9	RGSH015SL200CANNZ8N00SSD	190201343	15,000 BTU	645 CFM	60	265/1	LEFT HAND RETURN WITH SIDE DISCHARGE
HP 24-10	RGSH24EL200CANNZ8N00SSD	190201442	24,000 BTU	540 CFM	65	265/1	LEFT HAND RETURN WITH END DISCHARGE
HP 24-11	RGSH24EL200CANNZ8N00SSD	190201443	24,000 BTU	680 CFM	55	265/1	LEFT HAND RETURN WITH END DISCHARGE
HP 38-12	RGSH038EL400CANNZ8P00SSD	190201455	36,000 BTU	680 CFM	90	460/3	LEFT HAND RETURN WITH END DISCHARGE
HP 42-13	RGSH42EL400CANNZ8P00SSD	190201329	42,000 BTU	820 CFM	280	460/3	LEFT HAND RETURN WITH END DISCHARGE
HP 42-14	RGSH42EL400CANNZ8P00SSD	190201328	42,000 BTU	960 CFM	110	460/3	LEFT HAND RETURN WITH END DISCHARGE
HP 48-15	RGSH48EL400CANNZ8P00SSD	190201367	48,000 BTU	1275 CFM	135	460/3	LEFT HAND RETURN WITH END DISCHARGE

DIFFUSER, REGISTER, AND GRILLE SCHEDULE								
MARK	BASIS OF DESIGN (MANUFACTURER / MODEL)	MOUNTING	TYPE	FACE SIZE	NECK SIZE	MAX NC	MAX PD (INWC)	NOTES
RETURN								
RG-1	PRICE / 80	CEILING	SQUARE FACE RETURN GRILLE	22"x22"	22"x22"	20	0.08	1-4
SUPPLY								
SD-1	PRICE / SPD	CEILING	SQUARE FACE DIFFUSER W/ ROUND NECK	24"x24"	6"ø	20	0.08	1-5
SD-2	PRICE / SPD	CEILING	SQUARE FACE DIFFUSER W/ ROUND NECK	24"x24"	8"ø	20	0.08	1-5
SD-3	PRICE / SPD	CEILING	SQUARE FACE DIFFUSER W/ ROUND NECK	24"x24"	10"ø	20	0.08	1-5
SD-4	PRICE / SPD	CEILING	SQUARE FACE DIFFUSER W/ ROUND NECK	24"x24"	12"ø	20	0.08	1-5
1. ALL ALUMINUM CONSTRUCTION. 2. ARCHITECT TO SPECIFY FINISH. 3. FRAME TYPE TO MATCH CEILING CONSTRUCTION. COORDINATE WITH ARCHITECTURAL REFLECTED CEILING PLAN. 4. BRANCH DUCT SIZE TO BE SAME AS NECK SIZE UNLESS OTHERWISE SHOWN ON DRAWINGS. 5. PROVIDE PLENUM FOR DUCT CONNECTION.								

- KEYNOTES
- M2 CONTRACTOR TO ROUTE DUCTWORK AND CONNECT TO EXISTING HEAT PUMP.
- M3 CONTRACTOR TO ROUTE DUCTWORK AND CONNECT TO SUPPLY AIR MAIN BRANCH.
- M7 HEAT PUMP TO RETURN MIXTURE OF OA FROM UNCONNECTED OUTSIDE AIR DUCT AND RETURN AIR FROM ABOVE-CEILING PLENUM SPACE.

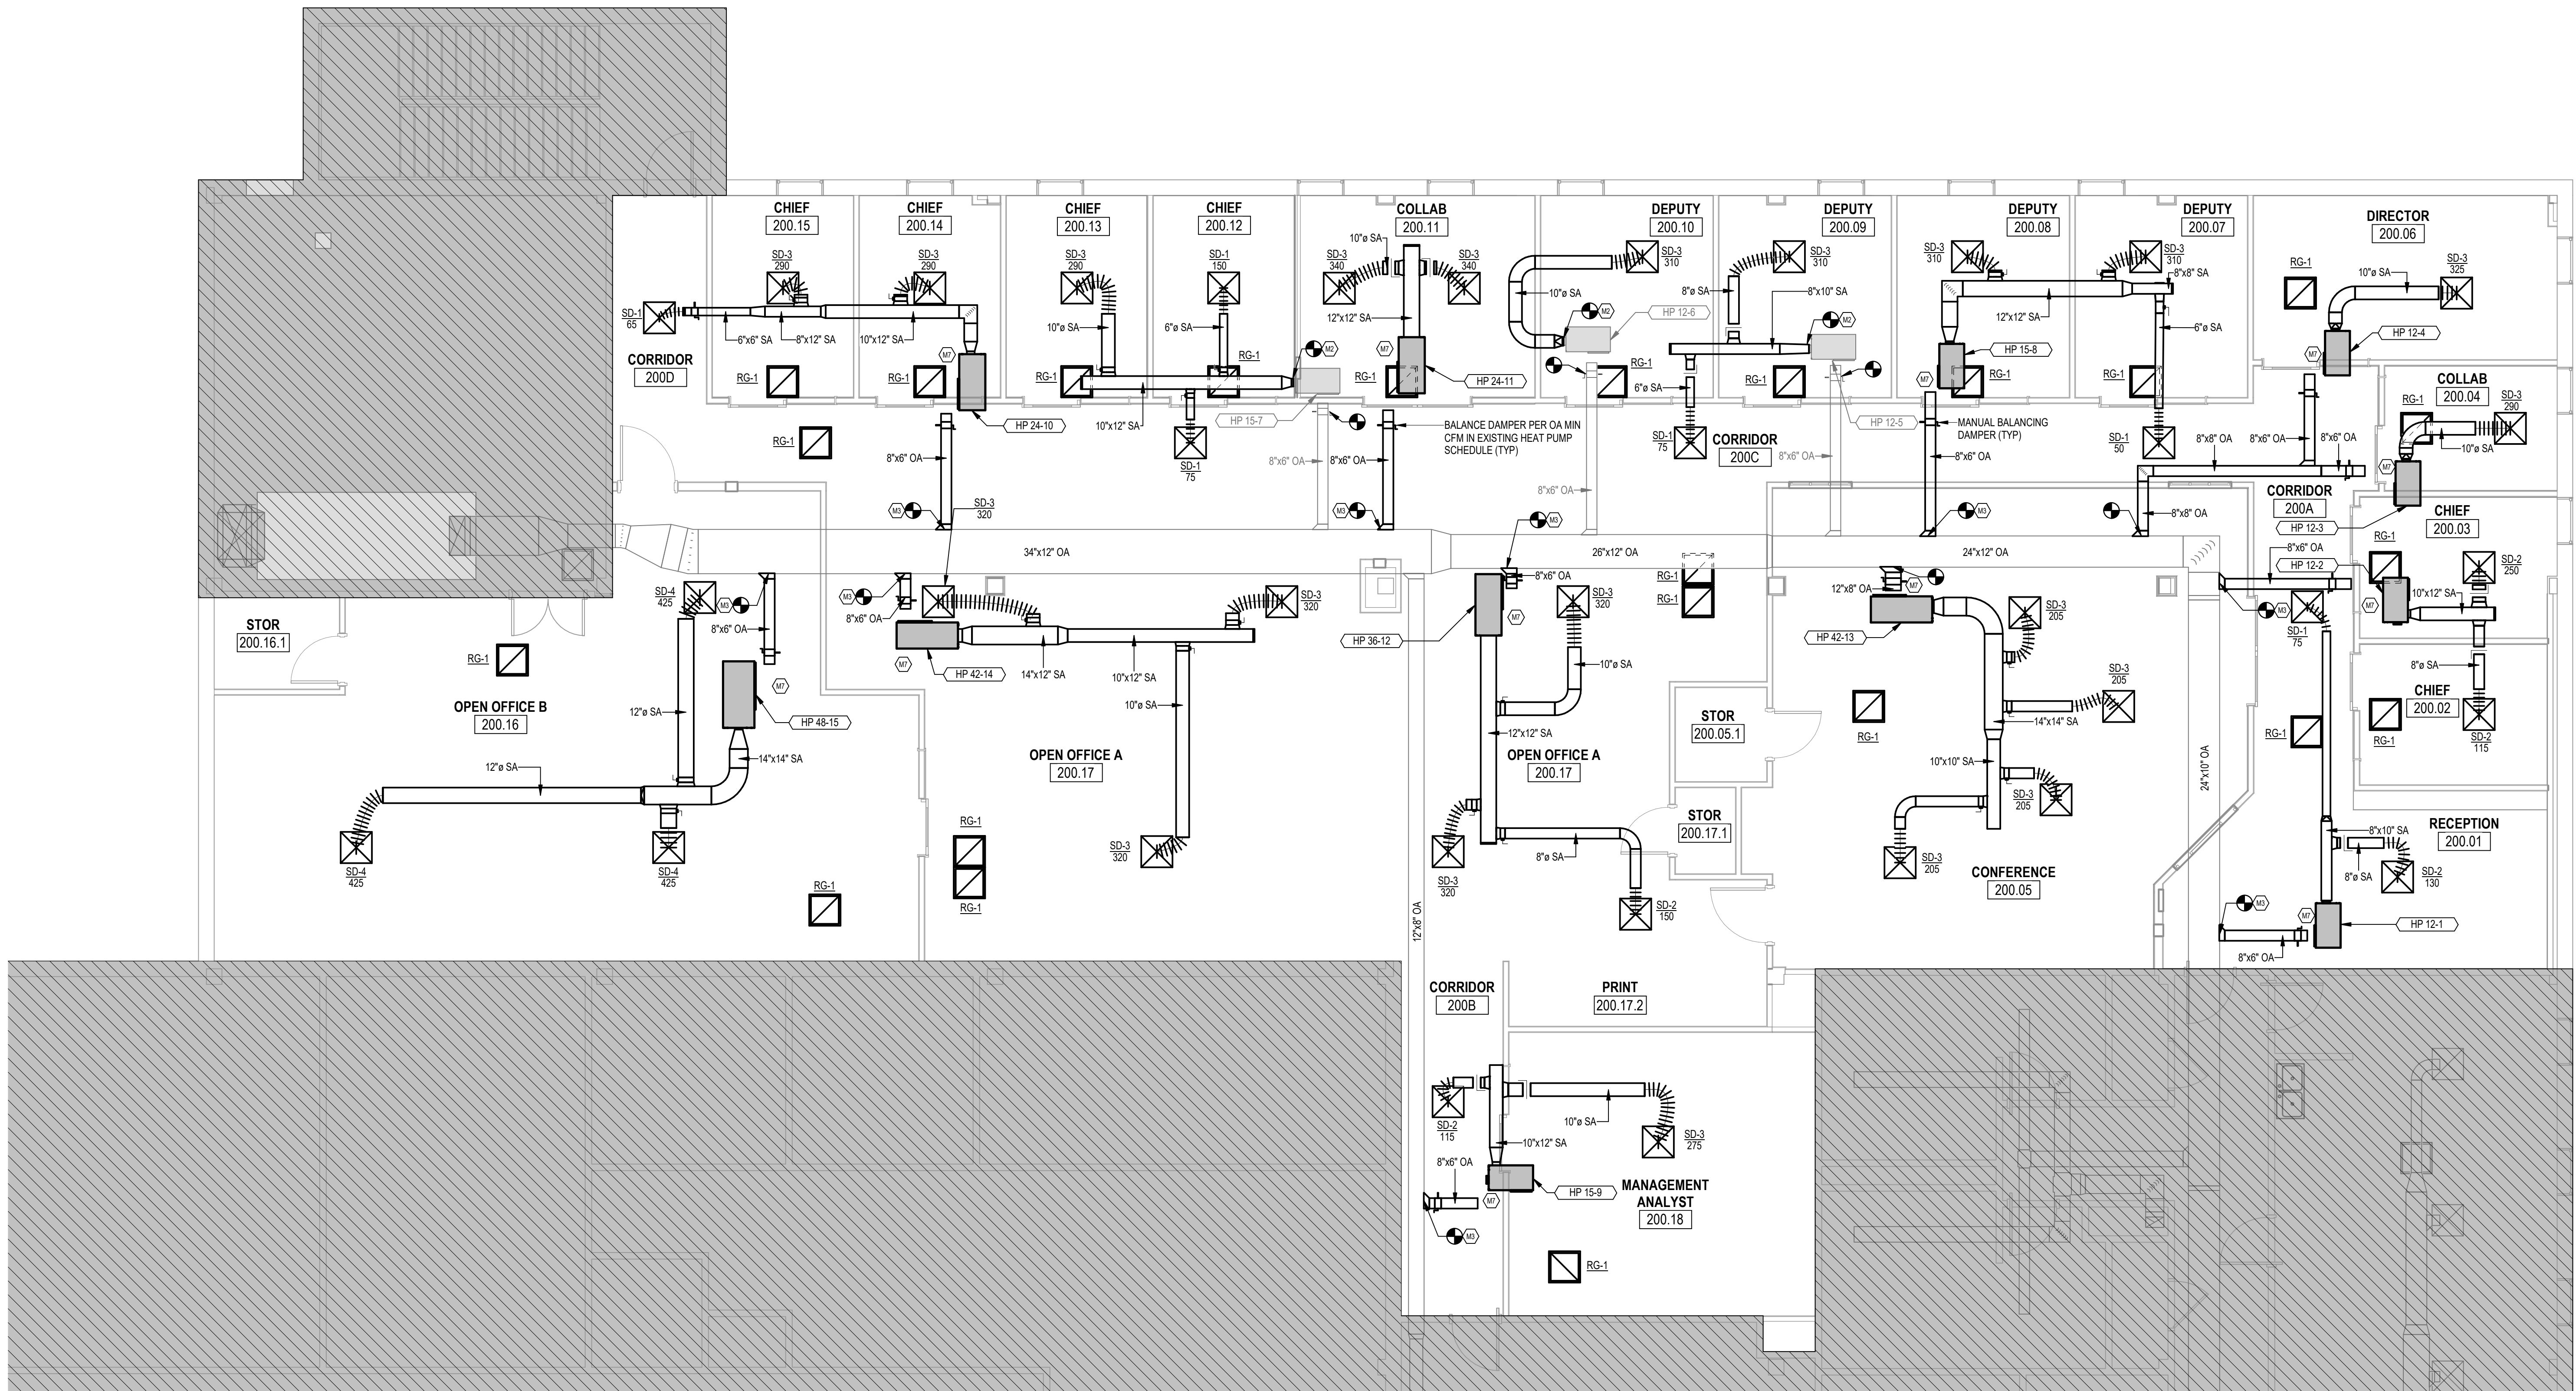

1 LEVEL 2 - MECHANICAL HVAC DUCT PLAN
3/16" = 1'-0"

No.	REVISION DESCRIPTION	DATE

ARCHITECT / ENGINEER:



SPUR SBBL COLLABORATIVE JV, INC
100 N. STONE AVENUE, STE 1102
TUCSON, AZ 85701
(405) 842-6100

IL ARCH. LICENSE NO.: 001023503 EXP. 11/30/22
IL MECH. ENGR. LICENSE NO.: 062.071715 EXP. 11/30/21
IL ELECT. ENGR. LICENSE NO.: 062.072296 EXP. 11/30/21

MECH / ELEC / PLUMB / TECH ENGINEER
SPUR DESIGN
10200 KING STREET, SUITE 350
OVERLAND PARK, KS 66210
(913) 369-7200

STAMP:



Drawing Title
LEVEL 2 - MECHANICAL HVAC DUCT
PLAN AND SCHEDULES

VA Health Care System Approval:

Project Title
HINES FINANCE CENTER

Location
STATION 201, BUILDING 215
1ST AVENUE NORTH 22ND STREET
HINES, IL 60141

Date
06/14/2021

Checked
JRM

Drawn
RDC

Project Number
201VB3032

Drawing Number
MH-101

Drawing # 16 OF 29


FULLY SPRINKLERED
100% DESIGN

Veterans
Benefits
Administration



5/19/2021 3:25:55 PM

KEYNOTES
M5 CONTRACTOR TO CONNECT NEW WATER LOOP SUPPLY AND RETURN PIPING TO EXISTING MAIN IN LOCATION SHOWN.
M6 CONTRACTOR TO CONNECT NEW CONDENSATE DRAIN PIPING BACK TO EXISTING MAIN IN LOCATION SHOWN.

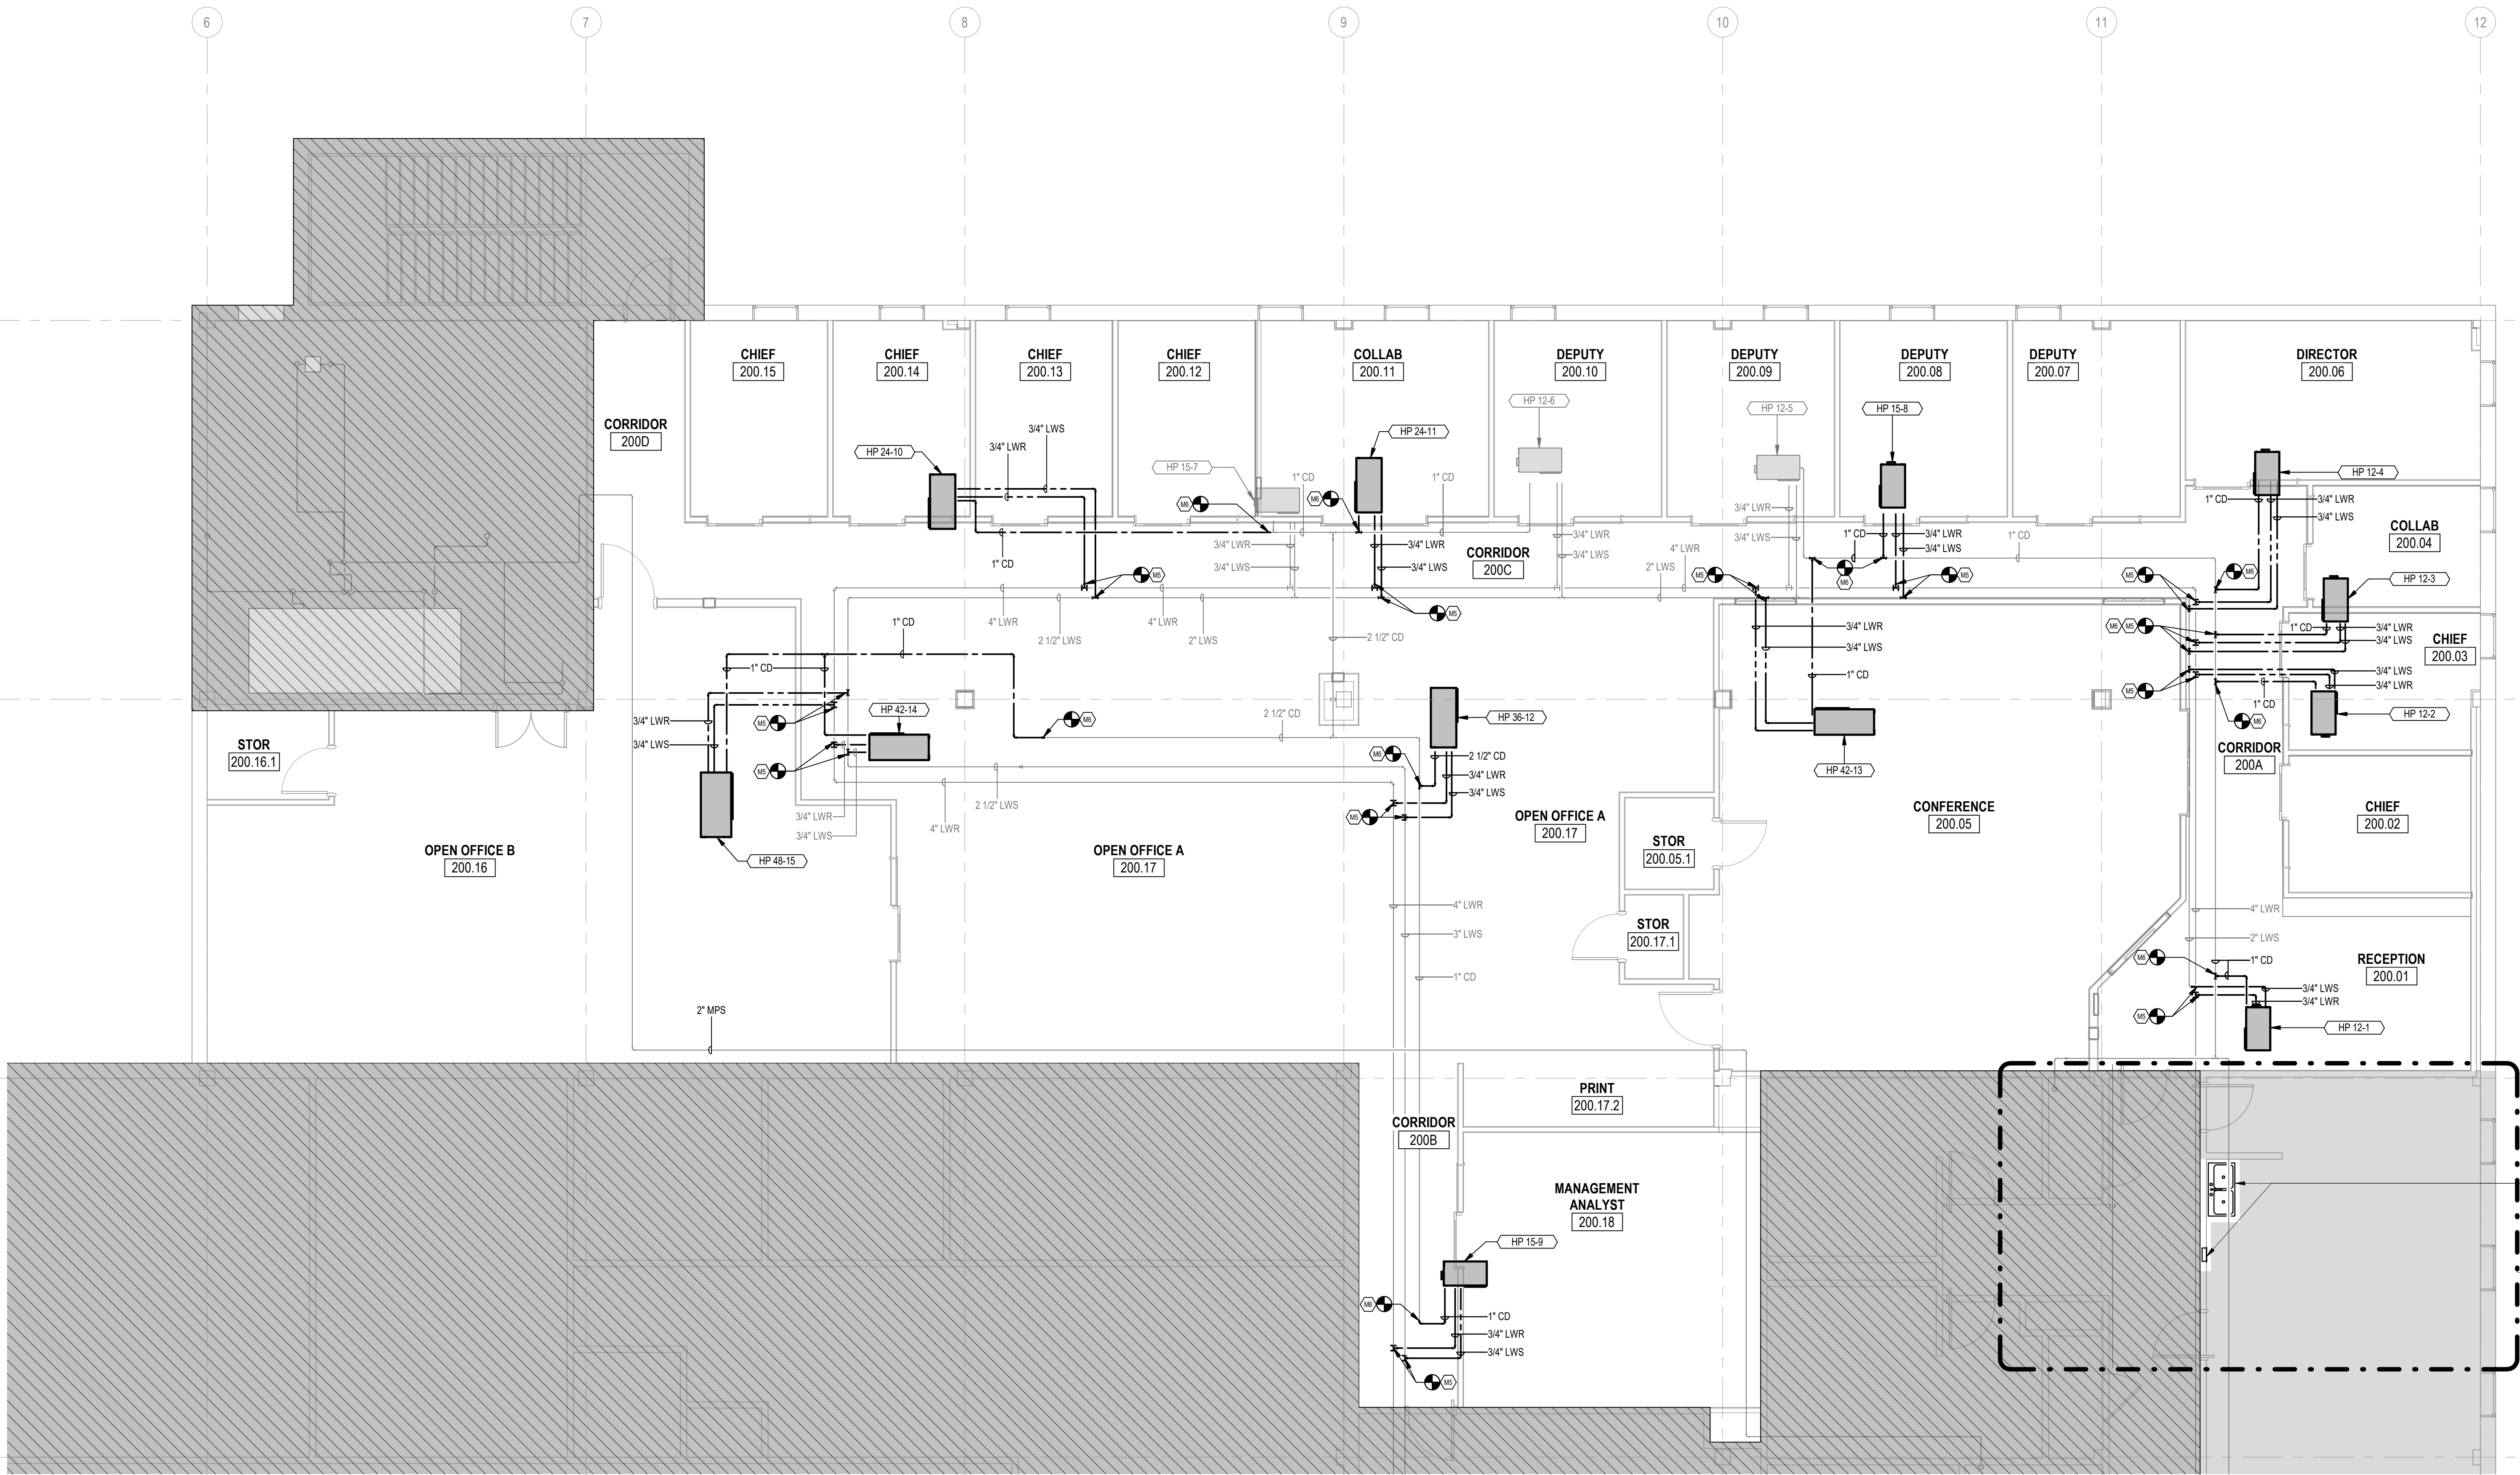

1 MECHANICAL HVAC PIPING PLAN
3/16" = 1'-0"

No.	REVISION DESCRIPTION	DATE

ARCHITECT / ENGINEER:



SPUR SBBL COLLABORATIVE JV, INC
100 N. STONE AVENUE, STE 1102
TUCSON, AZ 85701
(405) 842-6100

IL ARCH. LICENSE NO.: 001023503 EXP. 11/30/22
IL MECH. ENGR. LICENSE NO.: 062.071715 EXP. 11/30/21
IL ELECT. ENGR. LICENSE NO.: 062.072296 EXP. 11/30/21

MECH / ELEC / PLUMB / TECH ENGINEER
SPUR DESIGN
11020 KING STREET, SUITE 350
OVERLAND PARK, KS 66210
(913) 369-7200

STAMP:



Drawing Title
LEVEL 2 - MECHANICAL HVAC PIPING PLAN

VA Health Care System Approval:

Project Title
HINES FINANCE CENTER

Location
STATION 201, BUILDING 215
1ST AVENUE NORTH 22ND STREET
HINES, IL 60141

Date
06/14/2021

Checked
JRM

Drawn
RDC

Project Number
201VB3032

Drawing Number
MH-102

Drawing # 17 OF 29


FULLY SPRINKLERED
100% DESIGN

Veterans
Benefits
Administration



5/19/2021 8:32:31 AM


NOT TO SCALE

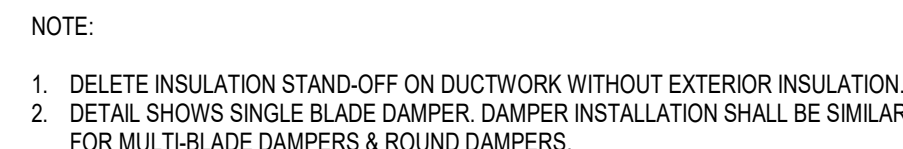


NOT TO SCALE




FLEXIE

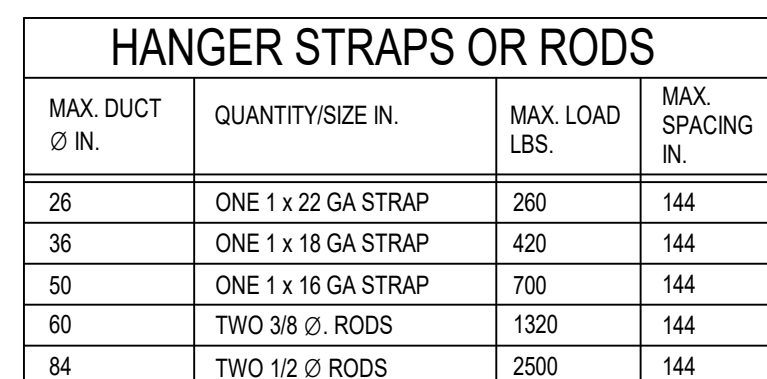



NOT TO SCALE

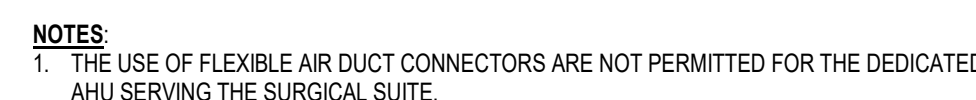


NOT TO SCALE

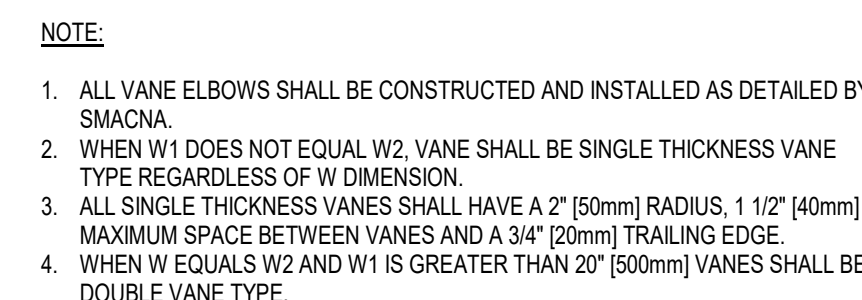


NOT TO SCALE

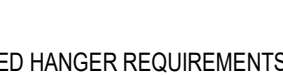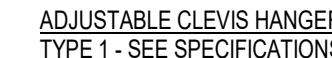

PIPE R

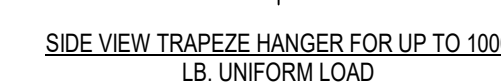


NOTE: FOR TRAPEZE HANGER TAKE SPACING OF SMALLEST SIZE ON TRAPEZE

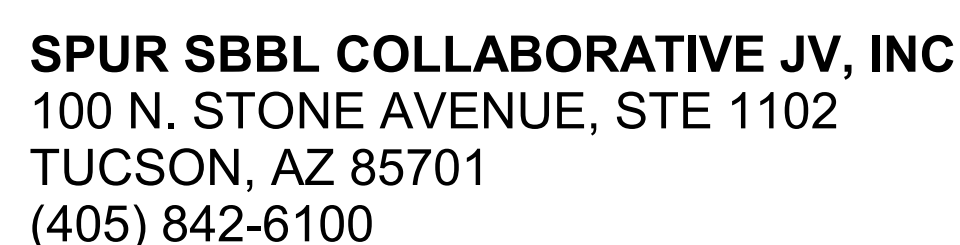ARCHITECT / ENGINEER:

IL ARCH. LICENSE NO.: 001023503	EXP. 11/30/22
IL MECH. ENGR. LICENSE NO.: 062.071715	EXP. 11/30/21
IL ELEC. ENGR. LICENSE NO.: 062.072296	EXP. 11/30/21

MECH / ELEC / PLUMB / TECH ENGINEER
SPUR DESIGN
11020 KING STREET, SUITE 350
OVERLAND PARK, KS 66210
(913) 369-7200

STAMP:

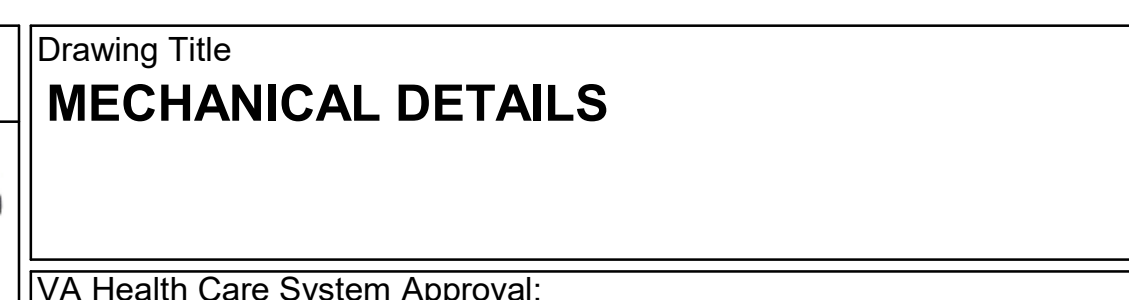

Project Title	HINES FINANCE CENTER
---------------	-----------------------------

Location	STATION 201, BUILDING 215 1ST AVENUE NORTH 22ND STREET HINES, IL 60141
----------	--

Checked IRM	Drawn BDC
----------------	--------------

Project Number	201VB3032
----------------	-----------

Drawing Number

MH-200

Drawing # 18 OF 29

Veterans
Benefits
Administration



PROJECT DESIGN CONDITIONS									
CLIMATE CONDITIONS									
WEATHER STATION		2021 ASHRAE CLIMATE DATA / 725340							
ASHRAE CLIMATE ZONE		Zone 5							
HEATING 99.6% (F DB)		0.5 F (99.6% F DB)							
HUMIDIFICATION 99.6% (DP / HR / MCB)		-9.1 F / 3.4 / 3.0 F							
COOLING 0.4% (DB / MCB)		91.9 FDB / 74.7 FWB							
DEHUMIDIFICATION 0.4% (DP / HR / ..)		74.9 FDB / 133.6 / 94.0 FWB							
MAX. AMBIENT DB TEMP (50 YRS)		107.7 F							
MIN. AMBIENT DB TEMP (50 YRS)		-22.3 F							
BUILDING OPERATING HOURS (VERIFY...)									
MONDAY - FRIDAY		7:30 A.M. - 6:00 P.M.							
SATURDAY		7:30 A.M. - 6:00 P.M.							
SUNDAY		7:30 A.M. - 6:00 P.M.							
NOTES:									
1. ZONE LEVEL OCCUPANCY HOUR SCHEDULE SHALL BE PER BUILDING OPERATING HOURS UNLESS OTHERWISE SCHEDULED.									
2. ZONE LEVEL SET POINT CONDITIONS SHALL BE AS SCHEDULED UNLESS OTHERWISE SCHEDULED OR NOTED FOR ROOM SPECIFIC SPACE CONDITIONS.									
3. DIVISION 23 CONTRACTOR TO PROVIDE ROOM AIR BALANCE WHERE POSSIBLE. AIR BALANCE SHALL BE NEUTRAL FOR NON-CRITICAL SPACES NOT SHOWN IN SCHEDULE.									
4. CONTRACTOR TO VERIFY WITH SITE EXACT BUILDING OPERATING HOURS.									
OFFICE SPACE									
ROOM NAME	OCC °F Db (COOLING)	UNOCC °F Db (COOLING)	OCC °F Db (HEATING)	UNOCC °F Db (HEATING)	MAX. %RH	MIN. %RH	MAX. NOISE LEVEL NC	ROOM AIR BALANCE (o) (+) (-) (+ +)	NOTES
CHIEF OFFICE	75	78	70	68	60%	30%	35	(o)	1-3
RECEPTION	75	78	70	68	60%	30%	35	(o)	1-3
DEPUTY OFFICE	75	78	70	68	60%	30%	35	(o)	1-3
DIRECTOR OFFICE	75	78	70	68	60%	30%	35	(o)	1-3
CONFERENCE ROOM	75	78	70	68	60%	30%	35	(+)	1-3
COLLABORATIVE ROOM	75	78	70	68	60%	30%	40	(o)	1-3

POINTS LIST - STANDARD TRENDING INTERVALS			
POINT NAME	TREND INTERVAL	OPERATIONAL TREND DURATION	TESTING TREND DURATION
AI	15 MIN.	24 HOURS	3 DAYS
BO	CHANGE OF VALUE	24 HOURS	3 DAYS
AO	15 MIN.	24 HOURS	3 DAYS
BO	CHANGE OF VALUE	24 HOURS	3 DAYS
CALC	1 HOUR	30 DAYS	N/A
NOTES: 1. SEE EQUIPMENT POINT LISTS FOR EQUIPMENT SPECIFIC TRENDING REQUIREMENTS.			

SEQUENCE OF OPERATIONS HEAT PUMP TERMINAL UNIT (HP)

GENERAL DESCRIPTION

Each heat pump terminal unit shall be directly controlled by a BACnet compatible dedicated stand-alone unitary direct digital controller (DDC controller). Controller shall be wired to a wall unit (sensor) in its specific controlled zone. Sensor shall be wall plate. Wall unit shall contain precalibrated electronic sensor (1/3 F., 2 C.) providing controller with current zone temperature status. The controller shall directly control heat pump fan, compressor, and reversing valve as required to maintain zone temperature setpoints. Temperature setpoints shall be adjustable at operator's terminal. Individual heat pump out-of-normal conditions available at the controller shall be displayed as alarms at the operator's terminal. BACnet Alarms shall be generated by the system LSI (global controller) unit.

OPERATING MODES

OCCUPIED MODE

Fan shall run continuously or cycles with compressor. Fan may also be set to run continuously in cooling, but cycle in heating. Operator may select fan operation on a zone-by-zone basis. Heat pump controller logic shall cycle compressor and reversing valve to maintain heating and cooling setpoints.

UNOCCUPIED MODE

Cycle fan with compressor to maintain unoccupied space temperature as required for energy conservation. All heat pump control algorithms shall be kept in non-volatile EEPROM at the controller. Controller logic, working in conjunction with wall sensor, shall maintain heat pump operation, independent of other control equipment.

Standard factory logic control sequences shall be supplied for loading into controller EEPROM. Logic sequences shall be field modifiable to provide any necessary site customizations. Factory control programs shall be proportional plus integral type, maintaining maximum accuracy and stability. Controller shall be programmable, either locally or over the BACnet network. Controller communicates on an MS/TP LAN, utilizing standard BACnet protocol. (See P.I.C.S. below) Proprietary chip sets, such as LONworks's Neuron, shall not be permitted. Gateways that convert standard BACnet communication protocols to proprietary communication systems shall not be permitted.

Controller factory logic sequences shall vary the compressor duty time, within an adjustable cycle.

Discharge air temperature sensor shall be provided down stream of each heat pump. Sensor shall provide functional, test, and alarm monitoring of the heat pump operation.

Automatic heat pump alarm shall be displayed at operator's terminal if discharge temperature fails to rise above adjustable high limit alarm setpoint(s). Also display alarm at operator's terminal if discharge temperature fails to go below adjustable low alarm setpoint(s) when heat pump is cooling. Provide delay time before alarm is generated.

Operator shall be able to set a test mode automatically running the heat pump through one heating and one cooling cycle. Out of normal condition(s) shall be displayed at the operator's terminal if heat pump operation is unsatisfactory.

Provide internal safety timers to allow a minimum ON and OFF time for compressors and fan. Compressor to be on only when fan is ON. Turn off compressor if an operational alarm is detected.

Heat pump units with economizer shall have economizer controlled from the same unitary controller driving the heat pump. Provide minimum setpoints for minimum economizer damper position, and outside air lockout temperature. Provide display at operator terminal for economizer commanded position.


Economizer shall never close to less than minimum position when in the occupied mode. It shall close completely if the zone is in unoccupied mode. The economizer shall be used as the first stage of cooling. Economizer shall be driven to minimum position if the outside air temperature goes above the lockout temperature setpoint.

Provide condensate out-of-normal condition for each heat pump when condensate pans fills to unacceptable levels. Display condition at operator's terminal. Operator may select shutdown of cooling only, or entire heat pump. Operator shall have option to set either for each individual zone.

System shall monitor hydronic loop water temperature and loop flow. If the water temperature goes above or below adjustable operational limits, or if loop flow is interrupted, all heat pump operation shall be suspended.

Status (LED) indication shall be provided on each terminal unit controller for communication activity, and (optionally) for each digital output. It shall be possible by viewing LED to determine if communication status has been established with global controller. It shall also be possible to tell if unit controller is powered. Each digital output currently turned on, will be indicated by its own LED indicator.

If unitary controller binary outputs are unused in a specific application, they shall be available to accommodate other system operations, such as control a hydronic water valve at the heat pump.

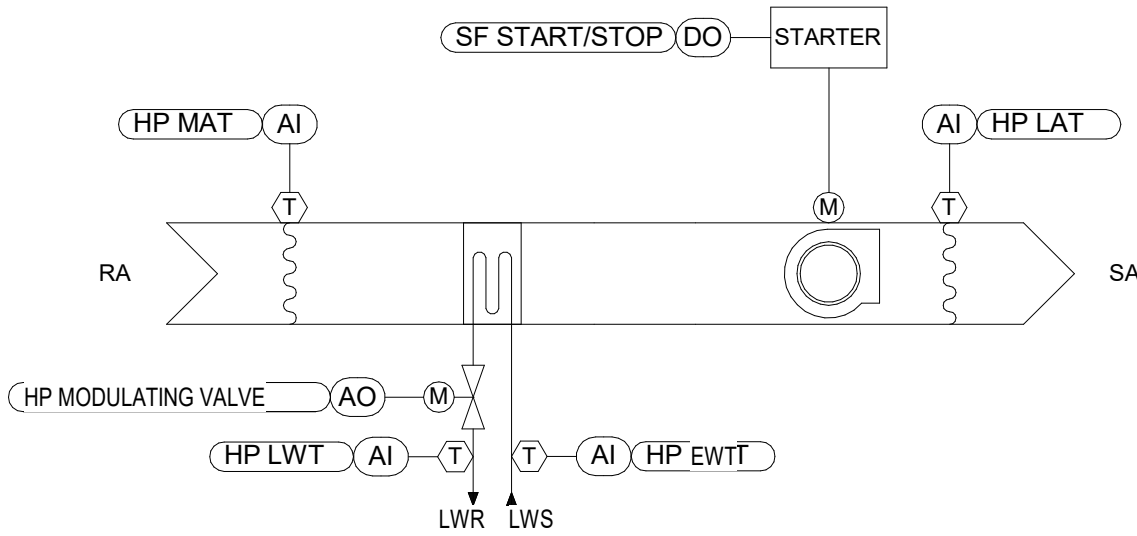

MECHANICAL CONTROLS LEGEND		
ABBREVIATIONS		
A ACC AIR COOLED CHILLER AF AFTER FILTER AFCV AIRFLOW CONTROL VALVE AFS AIRFLOW STATION AHU AIR HANDLING UNIT AI ANALOG INPUT AO ANALOG OUTPUT ATU AIR TERMINAL UNIT AV ANALOG VIRTUAL	I IFB INTEGRAL FACE AND BYPASS IRH INSIDE RELATIVE HUMIDITY L LAT LEAVING AIR TEMPERATURE M MAT MIXED AIR TEMPERATURE MOA MINIMUM OUTSIDE AIR N N.C. NORMALLY CLOSED NG NATURAL GAS N.O. NORMALLY OPEN O OA OUTSIDE AIR P PF PREFILTER PHC PREHEAT COIL R CHW CHILLED WATER RA RETURN AIR RF RETURN FAN RHC REHEAT COIL RE RETURN/EXHAUST S SA SUPPLY AIR SCR SILICON CONTROLLED RECTIFIER SD SMOKE DAMPER SF SUPPLY FAN SOV SHUT OFF VALVE SP SUMP PUMP T TCV TEMPERATURE CONTROL VALVE U UV ULTRAVIOLET V VAV VARIABLE AIR-VOLUME VFD VARIABLE FREQUENCY DRIVE	SENSORS & DEVICES DUCTWORK AFS AIRFLOW STATION AIRFLOW SENSOR SMOKE DETECTOR TEMPERATURE SENSOR FREEZE/STAT HUMIDITY SENSOR ENTHALPY SENSOR DAMPER POSITION INDICATOR DIFFERENTIAL PRESSURE SENSOR RETURN/EXHAUST AIR DUCT STATIC PRESSURE SENSOR SUPPLY AIR DUCT STATIC PRESSURE SENSOR
SYMBOLS		
EQUIPMENT		
CHILLED WATER COIL DIRECT EXPANSION COIL HEATING WATER COIL HOT WATER INTEGRAL FACE AND BYPASS COIL ELECTRIC HEATING COIL GAS FURNACE HUMIDIFIER DISPERSION GRID MODULATING OPPOSED BLADE DAMPER MODULATING PARALLEL BLADE DAMPER SMOKE DAMPER BACKDRAFT DAMPER VAV ATU MODULATING DAMPER	2-POSITION OPPOSED BLADE DAMPER 2-POSITION PARALLEL BLADE DAMPER FILTER BLOWER FAN PLENUM FAN PUMP CURRENT TRANSMITTER POINT TYPE POINT NAME	TEMPERATURE SENSOR DIFFERENTIAL PRESSURE SENSOR FLOW METER AQUASTAT THREE-WAY MODULATING CONTROL VALVE TWO-WAY MODULATING CONTROL VALVE
ZONE		
		ZONE TEMPERATURE SENSOR ZONE HUMIDITY SENSOR POSITIVE SPACE DIFFERENTIAL PRESSURE SENSOR NEGATIVE SPACE DIFFERENTIAL PRESSURE SENSOR

FULLY SPRINKLERED
100% DESIGN



No.	REVISION DESCRIPTION	DATE	ARCHITECT / ENGINEER:		STAMP:	Drawing Title	Project Title	Project Number	Veterans Benefits Administration	
			SPUR DESIGN		J. ROSS MYLES 062-071715 6/14/2021 OF ILLINOIS	MECHANICAL CONTROLS	HINES FINANCE CENTER	201VB3032	VA	
			SPUR SBBL COLLABORATIVE JV, INC 100 N. STONE AVENUE, STE 1102 TUCSON, AZ 85701 (405) 842-6100			VA Health Care System Approval:	STATION 201, BUILDING 215 1ST AVENUE NORTH 22ND STREET HINES, IL 60141	Drawing Number MH-300	U.S. Department of Veterans Affairs	
			MECH / ELEC / PLUMB / TECH ENGINEER SPUR DESIGN 11020 KING STREET, SUITE 350 OVERLAND PARK, KS 66210 (913) 369-7200				Date 06/14/2021	Checked JRM	Drawn RDC	Drawing # 19 OF 29
			IL ARCH. LICENSE NO.: 001023503 IL MECH. ENGR. LICENSE NO.: 062.071715 IL ELECT. ENGR. LICENSE NO.: 062.072296							
			EXP. 11/30/22 EXP. 11/30/21 EXP. 11/30/21							

5/19/2021 8:32:33 AM

VA FORM 08-6231

PLUMBING FIXTURE SCHEDULE									
MARK	FIXTURE	BASIS OF DESIGN		PIPING ROUGH-IN			DESCRIPTION		
		MANUFACTURER	MODEL	WASTE (IN)	CW (IN)	HW (IN)			
P-1	LUSTERTONE STAINLESS STEEL 33" X 19-1/2" X 7-5/8" EQUAL DOUBLE BOWL TOP MOUNT SINK	ELKAY	LR3319	3-1/2"	1-1/2"	1-1/2"	14" X 14" X 7-1/2" BOWL DIMENSIONS. PROVIDE WITH SINGLE FAUCET, P-TRAP, DRAIN, TAILPIECE, BOTTOM GRID, AND STOPS.		
P-2	LOW LEAD, QTR TURN VALVE BOX	IPS CORPORATION	MIB3AS	-	1/2"	-			

- KEYNOTES
- P1 CONTRACTOR TO INSTALL NEW TWO BASIN SINK AND ASSOCIATED DOMESTIC, SANITARY, AND VENT PIPING IN THE LOCATION SHOWN. ROUTE AND CONNECT TO NEAREST PIPING MAINS IN LOCATIONS SHOWN. EXISTING SANITARY PIPING MAIN IS LOCATED UNDER FLOOR IN APPROXIMATE LOCATION SHOWN. EXISTING DOMESTIC WATER AND VENT PIPING MAINS ARE LOCATED NEAR RESTROOM. VERIFY EXISTING PIPE LOCATIONS AND CAPACITIES PRIOR TO PROJECT START.
- P2 CONTRACTOR TO PROVIDE VALVE BOX FOR REFRIGERATOR. ROUTE 1/2" COPPER PIPING FROM VALVE BOX TO NEW DOMESTIC COLD WATER CONNECTION IN THE LOCATION SHOWN.

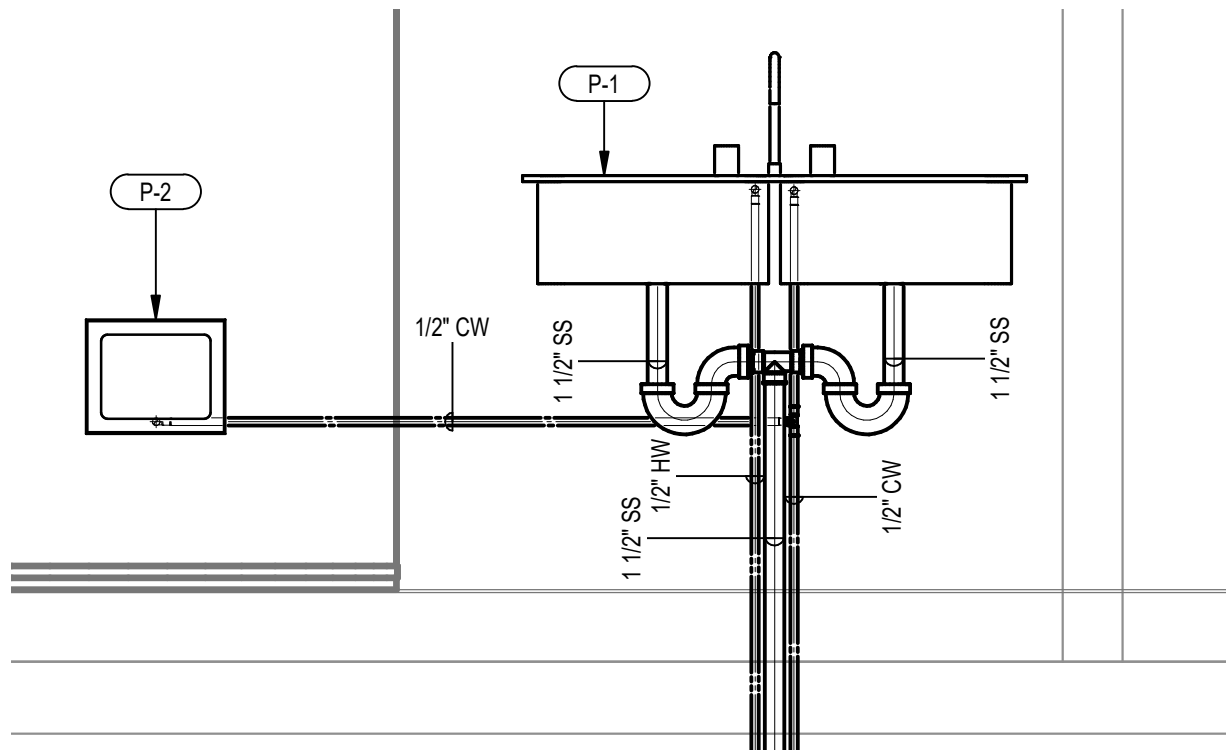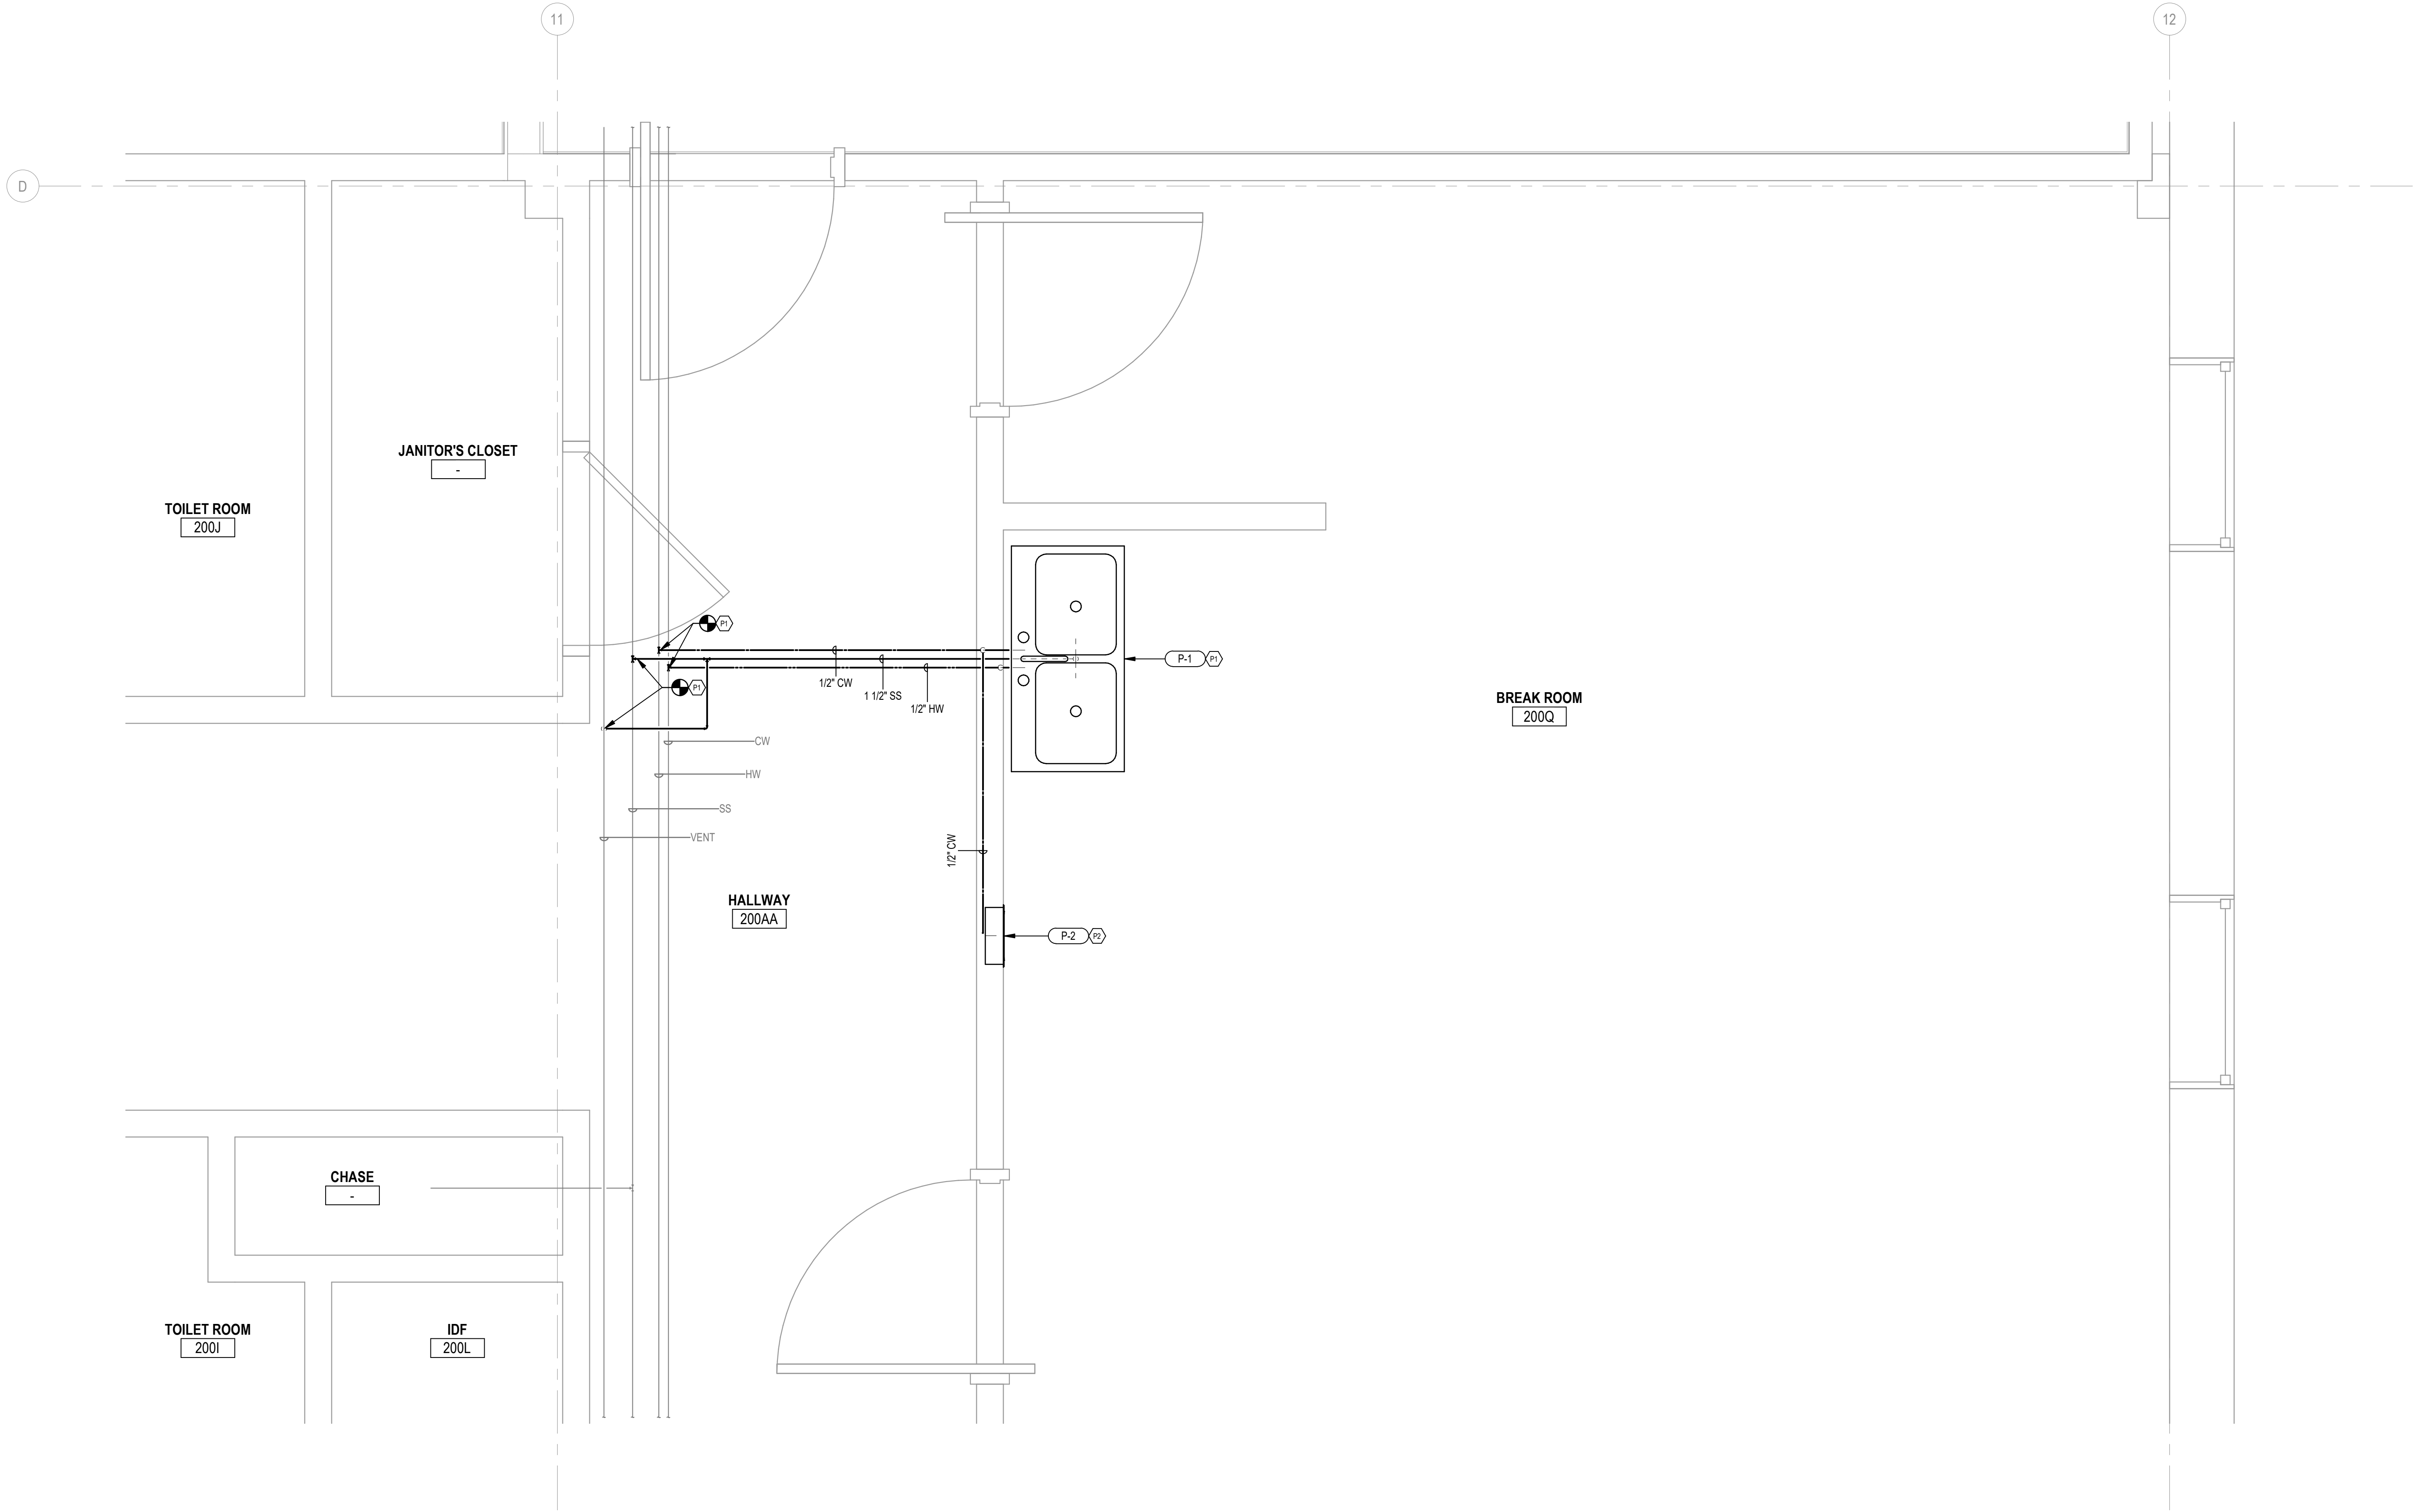

1 BREAK ROOM PLUMBING ENLARGED PLAN
3/4" = 1'-0"

2 BREAK ROOM PIPING DETAIL
NOT TO SCALE

No.	REVISION DESCRIPTION	DATE	ARCHITECT / ENGINEER:	MECH / ELEC / PLUMB / TECH ENGINEER	STAMP:	Drawing Title	Project Title	Project Number	Veterans Benefits Administration	
			SPUR DESIGN	SPUR SBBL COLLABORATIVE JV, INC 100 N. STONE AVENUE, STE 1102 TUCSON, AZ 85701 (405) 842-6100 IL ARCH. LICENSE NO.: 001023503 EXP. 11/30/22 IL MECH. ENGR. LICENSE NO.: 062.071715 EXP. 11/30/21 IL ELEC. ENGR. LICENSE NO.: 062.072296 EXP. 11/30/21		LEVEL 2 - BREAK ROOM PLUMBING ENLARGED PLAN	HINES FINANCE CENTER	201VB3032		
						VA Health Care System Approval:	Location	Drawing Number	P-100	
							STATION 201, BUILDING 215 1ST AVENUE NORTH 22ND STREET HINES, IL 60141			
							Date	Checked	Drawn	Drawing # 20 OF 29
							06/14/2021	JRM	RDC	

FULLY SPRINKLERED
100% DESIGN

5/19/2021 8:32:37 AM

VA FORM 08-6231

- GENERAL NOTES
- A. DISCONNECT AND REMOVE ALL CEILING MOUNTED FIRE ALARM DEVICES AND SECURITY DOOR HARDWARE WITHIN THE AREA OF WORK.
- B. DISCONNECT AND REMOVE ALL POWER RECEPTACLES AND DEVICES WITHIN THE AREA OF SCOPE, UNLESS SHOWN AS EXISTING TO REMAIN. REMOVE ALL ASSOCIATED CONDUITS, JUNCTION BOXES, AND CONDUCTORS BACK TO FEEDER BRANCH PANEL.
- C. DISCONNECT AND REMOVE ALL DATA OUTLETS, ASSOCIATED CONDUITS, CABLES AND CABLE TRAYS, WITHIN THE AREA OF WORK, BACK TO SERVER RACK IN TWL ROOM 1-115A.
- D. DISCONNECT, REMOVE, AND PRESERVE ALL INTERCOM SPEAKERS AND CEILING MOUNTED FIRE ALARM DEVICES WITHIN THE AREA OF SCOPE FOR REUSE IN NEW CONSTRUCTION.
- E. ALL LOCATIONS ARE APPROXIMATE FIELD VERIFY EXACT COUNTS AND LOCATIONS PRIOR TO DEMOLITION.
- F. ALL JUNCTION BOX LOCATIONS ARE APPROXIMATE. CONTRACTOR TO FIELD VERIFY POTENTIAL FOR REUSE OF HARDWARE AND RACEWAYS. REUSE HARDWARE AND RACEWAYS WHERE POSSIBLE AND ABANDON AND PATCH THE WALLS IN ALL LOCATIONS REUSE IS NOT FEASIBLE.
- G. DISCONNECT AND REMOVE ALL POWER, LIGHTING, DATA, AND LOW VOLTAGE CONDUIT, CABLES, DEVICES, AND RACEWAYS ABOVE CEILING NO LONGER IN USE.
- H. DISCONNECT AND REMOVE ALL POWER, DATA DEVICES, AND CABLES IN RAISED FLOORING. REMOVE ALL ASSOCIATED CONDUIT, JUNCTION BOXES, AND CONDUCTORS BACK TO FEEDER BRANCH PANEL OR NETWORK SWITCH.
- I. SHADED AREAS ARE OUT OF PROJECT SCOPE.
- H. EXISTING CIRCUITS IN OUT OF SCOPE AREAS MAY BE CONNECTED TO DEVICES BEING DEMOLISHED IN AREA OF SCOPE. IF AN OUT OF SCOPE AREA CIRCUIT IS CONNECTED TO A PARTIAL CIRCUIT BEING DEMOLISHED, NOTIFY COR PRIOR TO DISREUTION OR DOWNTIME.

- ELECTRICAL KEYNOTES
- 1 NUMBER AND LOCATION OF DEVICES ON THIS WALL ARE APPROXIMATED BECAUSE OF BUILT-IN FURNITURE SYSTEMS. FIELD VERIFY AND REMOVE ALL POWER AND DATA DEVICES ON THIS WALL.
- 2 APPROXIMATE LOCATION OF EXISTING SERVER RACK. DISCONNECT AND REMOVE ALL COPPER CATEGORY 5 AND CATEGORY 5E PATCH CABLES AND CABLE RUNS TO AREA OF SCOPE.
- 3 ONLY WORK IN THIS ROOM IS TO DEMOLISH THIS DUPLEX RECEPTACLE. REMOVE DEVICE, CONDUCTOR AND ASSOCIATED RACEWAY BACK TO NEAREST JUNCTION BOX.
- 12 DISCONNECT AND PRESERVE ELECTRICAL DISCONNECT DEVICE AND REMOVE CONDUCTORS FEEDING EXISTING HEAT PUMP. REMOVE CONDUCTOR AND RACEWAY BACK TO NEAREST JUNCTION BOX. SEE PANEL SCHEDULE FOR BEST ESTIMATE OF CIRCUITRY BASED ON LIMITED HISTORICAL INFORMATION. TYPICAL.
- 15 APPROXIMATE LOCATION OF EXISTING CAMERA. DISCONNECT AND PRESERVE FOR REINSTALLATION IN NEW CEILING. PRESERVE AND EXTEND EXISTING CABLE CONNECTION TO NEW LOCATION SHOWN ON SHEET 'E103'.

1 LEVEL 2 - ELECTRICAL POWER DEMOLITION PLAN
3/16" = 1'-0"

No.	REVISION DESCRIPTION	DATE

ARCHITECT / ENGINEER:




SPUR SBBL COLLABORATIVE JV, INC
100 N. STONE AVENUE, STE 1102
TUCSON, AZ 85701
(405) 842-6100

IL ARCH. LICENSE NO.: 001023503 EXP. 11/30/22
IL MECH. ENGR. LICENSE NO.: 062.071715 EXP. 11/30/21
IL ELECT. ENGR. LICENSE NO.: 062.072296 EXP. 11/30/21

MECH / ELEC / PLUMB / TECH ENGINEER
SPUR DESIGN
11020 KING STREET, SUITE 350
OVERLAND PARK, KS 66210
(405) 842-6100

STAMP:

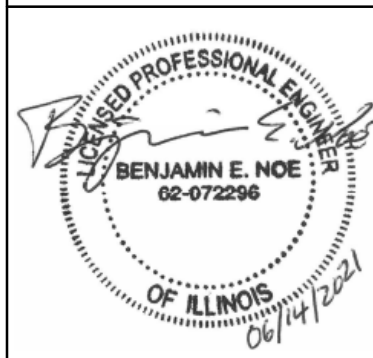

Drawing Title
LEVEL 2 - ELECTRICAL POWER
DEMOLITION PLAN

VA Health Care System Approval:

Project Title
HINES FINANCE CENTER

Location STATION 201, BLDG 215, STE 200X
1ST AVENUE NORTH 22ND STREET
HINES, IL 60141

Date
06/14/2021

Checked
BN

Drawn
BP

Project Number
201VB3032

Drawing Number

EPD-101

Drawing # 22 OF 29

FULLY SPRINKLERED
100% DESIGN

Veterans
Benefits
Administration



5/18/2021 2:17:24 PM

- GENERAL NOTES
- A. DISCONNECT AND REMOVE ALL LIGHT FIXTURES WITHIN THE AREA OF SCOPE AND RETURN TO OWNER'S STOCK REMOVE CONDUIT AND FEEDERS BACK TO NEAREST JUNCTION BOX AND VERIFY CIRCUIT LABELING OR LABEL WITH FEEDER CIRCUITS.
 - B. DISCONNECT AND REMOVE DAYLIGHT SENSORS AND PRESERVE FOR REUSE.
 - C. ALL LOCATIONS ARE APPROXIMATE FIELD VERIFY EXACT COUNTS AND LOCATIONS PRIOR TO DEMOLITION.
 - D. DISCONNECT AND REMOVE ALL POWER, LIGHTING, DATA, AND LOW VOLTAGE CONDUIT, CABLING, DEVICES, AND RACEWAYS ABOVE CEILING NO LONGER IN USE.
 - E. STORE AND PRESERVE ALL REMOVED LIGHT FIXTURES AND LIGHTING CONTROL DEVICES FOR INSTALLATION IN NEW GRID CEILING AND WALLS.
 - F. SHADED AREAS ARE OUT OF PROJECT SCOPE.
 - G. ALL CEILINGS WITHIN PROJECT SCOPE AREA ARE BEING DEMOLISHED.
 - H. EXISTING CIRCUITS IN OUT OF SCOPE AREAS MAY BE CONNECTED TO DEVICES BEING DEMOLISHED IN AREA OF SCOPE. IF AN OUT OF SCOPE AREA CIRCUIT IS CONNECTED TO A PARTIAL CIRCUIT BEING DEMOLISHED, NOTIFY COR PRIOR TO DISRUPTION OR DOWNTIME.
 - I. EXISTING FIXTURES ARE CONTROLLED BY A LUTRON QUANTUM SYSTEM. DISCONNECT AND PRESERVE ALL LUTRON SYSTEM AND RELATED PRODUCTS FOR REUSE OR RETURN TO OWNER'S STOCK.

1 LEVEL 2 - ELECTRICAL LIGHTING DEMOLITION PLAN
3/16" = 1'-0"

No.	REVISION DESCRIPTION	DATE

ARCHITECT / ENGINEER:




SPUR SBBL COLLABORATIVE JV, INC
100 N. STONE AVENUE, STE 1102
TUCSON, AZ 85701
(405) 842-6100

IL ARCH. LICENSE NO.: 001023503 EXP. 11/30/22
IL MECH. ENGR. LICENSE NO.: 062.071715 EXP. 11/30/21
IL ELECT. ENGR. LICENSE NO.: 062.072296 EXP. 11/30/21

MECH / ELEC / PLUMB / TECH ENGINEER
SPUR DESIGN
11020 KING STREET, SUITE 350
OVERLAND PARK, KS 66210
(405) 842-6100

STAMP:

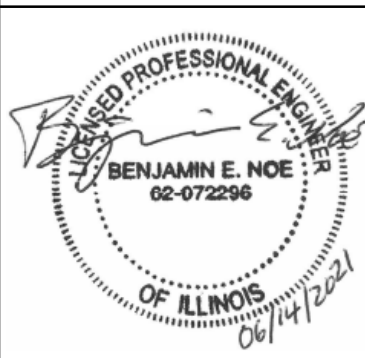

Drawing Title
LEVEL 2 - ELECTRICAL LIGHTING
DEMOLITION PLAN

VA Health Care System Approval:

Project Title
HINES FINANCE CENTER

Location STATION 201, BLDG 215, STE 200X
1ST AVENUE NORTH 22ND STREET
HINES, IL 60141

Date
06/14/2021

Checked
BN

Drawn
BP

Project Number
201VB3032

Drawing Number

EPD-102

Drawing # 23 OF 29

FULLY SPRINKLERED
100% DESIGN

Veterans
Benefits
Administration




- GENERAL NOTES
- A. CONTRACTOR IS RESPONSIBLE FOR VERIFYING AND CONNECTING ALL NEW AND EXISTING RECONNECTED LOADS IN A BALANCED MANNER.
- B. ALL FLOOR MOUNTED DEVICES SHALL BE FED THROUGH POKE THROUGHS IN THE NEW RAISED FLOORING. PROVIDE ALL NECESSARY HARDWARE FOR A COMPLETE AND WORKING SYSTEM.
- C. JUNCTION BOXES UNDER WORKSTATIONS CONNECT DIRECTLY TO POWER HARNESSES BUILT IN TO PREMANUFACTURED FURNITURE. CONNECTIONS AND LOCATIONS SHOWN ARE BASED ON HERMAN MILLER PREFABRICATED FURNITURE AS SHOWN IN ARCHITECTURAL DRAWINGS AND BASED ON A DESIGN STANDARD OF FOUR (4) DUPLEX RECEPTACLES PER BASIC WORKSTATION. INDIVIDUAL OFFICE WORKSTATIONS ARE CIRCUITED FOR SIX (6) DUPLEX RECEPTACLES. AND THE DIRECTOR'S OFFICE IS CIRCUITED FOR EIGHT (8) DUPLEX RECEPTACLES. COORDINATE EXACT REQUIREMENTS AND LOCATIONS WITH FINAL FURNITURE SELECTIONS PRIOR TO ROUGH-IN.
- D. REUSE AND INSTALL EXISTING PRESERVED DISCONNECTING DEVICES FOR RELOCATED HEAT-PUMPS. HEAT PUMPS WILL RECONNECT TO THEIR ORIGINAL CIRCUITS. COORDINATION INFORMATION IS AVAILABLE ON THE NEW PANEL SCHEDULE BASED ON LIMITED HISTORICAL INFORMATION OBTAINED. CIRCUIT TRACING IS NECESSARY FOR REFEED ACCURACY.

- ELECTRICAL KEYNOTES
- 4 PROVIDE AND INSTALL DUPLEX RECEPTACLE FOR OWNER PROVIDED WALL MOUNTED SMARTBOARD.
- 5 PROVIDE AND INSTALL POKE-THROUGH IN RAISED FLOORING FOR CONNECTION TO POWERED PREMANUFACTURED CONFERENCE ROOM TABLE. COORDINATE EXACT REQUIREMENTS AND LOCATIONS WITH SELECTED FURNITURE PRIOR TO ROUGH-IN. TYPICAL.
- 6 PROVIDE AND INSTALL FLOORBOX ACCOMMODATING (2) QUAD RECEPTACLES AND DATA REQUIREMENTS ON SHEET EP-103 INDICATED BY NOTE 'B'. MAKE CONNECTION TO INTEGRATED POWER OUTLETS WITHIN NEW COLAB ROOM TABLE. COORDINATE EXACT REQUIREMENTS WITH FINAL FURNITURE SELECTIONS PRIOR TO ROUGH-IN. TYPICAL.
- 14 EXISTING RELOCATED HEAT PUMP IS SINGLE PHASE 277V. ORIGINAL NAME AND CIRCUITRY UNKNOWN DUE TO LIMITED HISTORICAL INFORMATION. PREVIOUSLY CONNECTED TO A CIRCUIT ON PANEL '2XDP'. REINSTALL PRESERVED EXISTING DISCONNECTING DEVICE AND RECONNECT TO SAME CIRCUIT FROM PREVIOUS LOCATION. TYPICAL.

1 LEVEL 2 - ELECTRICAL POWER PLAN
3/16" = 1'-0"

No.	REVISION DESCRIPTION	DATE

ARCHITECT / ENGINEER:

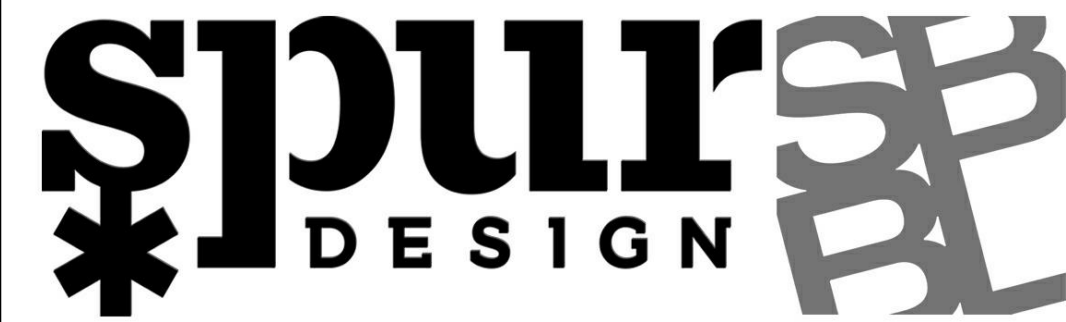

SPUR SBBL COLLABORATIVE JV, INC
100 N. STONE AVENUE, STE 1102
TUCSON, AZ 85701
(405) 842-6100

IL ARCH. LICENSE NO.: 001023503 EXP. 11/30/22
IL MECH. ENGR. LICENSE NO.: 062.071715 EXP. 11/30/21
IL ELECT. ENGR. LICENSE NO.: 062.072296 EXP. 11/30/21

MECH / ELEC / PLUMB / TECH ENGINEER
SPUR DESIGN
11020 KING STREET, SUITE 350
OVERLAND PARK, KS 66210
(405) 842-6100

STAMP:



Drawing Title
LEVEL 2 - ELECTRICAL POWER PLAN

VA Health Care System Approval:

Project Title
HINES FINANCE CENTER

Location STATION 201, BLDG 215, STE 200X
1ST AVENUE NORTH 22ND STREET
HINES, IL 60141

Date
06/14/2021

Checked
BN

Drawn
BP

Project Number
201VB3032

Drawing Number

EP-101

Drawing # 24 OF 29

FULLY SPRINKLERED
100% DESIGN

Veterans
Benefits
Administration



5/18/2021 2:17:15 PM

VA FORM 08-6231

- GENERAL NOTES
- A. SHADED AREAS INDICATE OUT OF PROJECT SCOPE.
- B. NEW FIXTURES WALL CONTROLS AND SENSORS TO TIE INTO THE EXISTING LUTRON QUANTUM SYSTEM. LUTRON SOFTWARE UPDATE MAY BE REQUIRED TO SUPPORT THE NEW HARDWARE INSTALLED.

- ELECTRICAL KEYNOTES
- 13 REUSE DAYLIGHT SENSORS AVAILABLE FROM DEMOLITION. COORDINATE ZONING AND WIRING REQUIREMENTS WITH LUTRON SHOP DRAWINGS PRIOR TO ROUGH-IN.



1 LEVEL 2 - ELECTRICAL LIGHTING PLAN
3/16\"/>

No.	REVISION DESCRIPTION	DATE

ARCHITECT / ENGINEER:
SPUR DESIGN

SPUR SBBL COLLABORATIVE JV, INC
100 N. STONE AVENUE, STE 1102
TUCSON, AZ 85701
(405) 842-6100
MECH / ELEC / PLUMB / TECH ENGINEER
SPUR DESIGN
11020 KING STREET, SUITE 350
OVERLAND PARK, KS 66210
(405) 842-6100
IL ARCH REG. NO. 001023503, EXP. 11/30/2022
IL ENGR REG. NO. 062.071715, EXP. 11/30/2021

STAMP:

Drawing Title
LEVEL 2 - ELECTRICAL LIGHTING PLAN
VA Health Care System Approval:

Project Title
HINES FINANCE CENTER
Location STATION 201, BLDG 215, STE 200X
1ST AVENUE NORTH 22ND STREET
HINES, IL 60141
Date 06/14/2021
Checked BN
Drawn BP

Project Number
201VB3032
Drawing Number
EP-102
Drawing # 25 OF 29

Veterans Benefits Administration
VA U.S. Department of Veterans Affairs

- GENERAL NOTES
- A. ALL LOCATIONS ARE APPROXIMATE FIELD VERIFY EXACT COUNTS AND LOCATIONS PRIOR TO DEMOLITION.
- B. ALL JUNCTION BOX LOCATIONS ARE APPROXIMATE. CONTRACTOR TO FIELD VERIFY POTENTIAL FOR REUSE OF HARDWARE AND RACEWAYS. REUSE HARDWARE AND RACEWAYS WHERE POSSIBLE AND ABANDON AND PATCH THE WALLS IN ALL LOCATIONS REUSE IS NOT FEASIBLE.
- C. SHADED AREAS INDICATE OUT OF PROJECT SCOPE.
- D. JUNCTION BOXES UNDER WORKSTATIONS CONNECT DIRECTLY TO DATA HARNESES BUILT IN TO PREMANUFACTURED FURNITURE. CONNECTIONS AND LOCATIONS SHOWN ARE BASED ON HERMAN MILLER PREFABRICATED FURNITURE AS SHOWN IN ARCHITECTURAL DRAWINGS AND BASED ON A DESIGN STANDARD OF (2) TWO DATA DROPS AND (1) ONE PHONE DROP IN A SINGLE FACEPLATE PER BASIC WORKSTATION.
- E. INDIVIDUAL OFFICE WORKSTATIONS ARE WIRED FOR (3) THREE DATA DROPS AND (1) ONE PHONE DROP IN A SINGLE FACEPLATE. AND THE DIRECTOR'S OFFICE IS WIRED FOR (3) THREE DATA DROPS AND (1) ONE PHONE DROP IN A SINGLE FACEPLATE. COORDINATE EXACT REQUIREMENTS AND LOCATIONS WITH FINAL FURNITURE SELECTIONS PRIOR TO ROUGH-IN.
- F. INSTALLATION OF NEW CONTROLS SHALL MAINTAIN EXISTING DOOR ACCESS CONTROLS CONFIGURATION AND TIE SEAMLESSLY INTO THE EXISTING BUILDING SECURITY SYSTEM. DEVICE TERMINATION PANELS ARE LOCATED IN THE IDF ROOM 200L.


- FIRE ALARM GENERAL NOTES
- A. PROVIDE FIRE ALARM SYSTEM DESIGN, INSTALLATION, AND MATERIALS IN ACCORDANCE WITH NFPA 70, NFPA 72, AND TITLE 14F CHICAGO FIRE PREVENTION CODE. SYSTEM SHALL ALSO COMPLY WITH ALL APPLICABLE BUILDING CODES, FIRE CODES, AS WELL AS, THE REQUIREMENTS OF THE AUTHORITY HAVING JURISDICTION AND INSURANCE CARRIER. VERIFY ALL REQUIREMENTS PRIOR TO BID.
- B. INFORMATION SHOWN ON CONTRACT DOCUMENTS IS GENERAL INFORMATION AND FOR BID PURPOSES ONLY. PERFORM REQUIRED CALCULATIONS AND COORDINATE WITH OTHER TRADES. REFER TO THE SPECIFICATIONS FOR ADDITIONAL INFORMATION.
- C. PROVIDE ALL EQUIPMENT AND LABOR REQUIRED FOR A COMPLETE AND OPERATIONAL FIRE ALARM SYSTEM.
- D. COORDINATE THE FIRE ALARM CONTROL PANEL AND REMOTE ANNUNCIATOR PANEL WITH THE FIRE DEPARTMENT AND AUTHORITY HAVING JURISDICTION PRIOR TO INSTALLATION.
- E. COORDINATE NOTIFICATION DEVICE PLACEMENT WITH FURNISHING, CABINETS, AND EQUIPMENT SO THAT DEVICES ARE NOT COVERED OR OBSTRUCTED FROM VIEW.
- F. FORWARD COMPLETED FIRE ALARM CERTIFICATE OF COMPLETION TO THE OWNER.

- ELECTRICAL KEYNOTES
8. PROVIDE AND INSTALL (2) DATA DROPS AND (1) PHONE DROP CABLEING WITHIN FLOOR BOX UNDER COLLAB TABLE. MAKE CONNECTION TO INTEGRATED DATA OUTLETS WITHIN NEW COLLAB ROOM TABLE. COORDINATE EXACT REQUIREMENTS WITH FINAL FURNITURE SELECTIONS PRIOR TO ROUGH-IN. TYPICAL.
9. APPROXIMATE LOCATION OF EXISTING SERVER RACK. RUN ALL NEW CATEGORY 6A CABLEING FOR NEW DATA AND PHONE DROPS TO THIS LOCATION. REPLACE ALL CATEGORY 5 AND CATEGORY 5E PATCH CABLEING WITH CATEGORY 6A PATCH CABLES.
10. PROVIDE AND INSTALL POKE-THROUGH IN RAISED FLOORING FOR CONNECTION TO DATA HARNESS IN PREMANUFACTURED CONFERENCE ROOM TABLE. PROVIDE AND INSTALL (3) DATA DROPS AND (1) PHONE DROP CABLEING TO EACH CONFERENCE TABLE POKE THROUGH LOCATION. COORDINATE EXACT REQUIREMENTS AND LOCATIONS WITH SELECTED FURNITURE PRIOR TO ROUGH-IN. TYPICAL.
17. INSTALL PRESERVED EXISTING CAMERA AND RECONNECT EXTENDED EXISTING CABLES FED FROM EXISTING BUILDING SECURITY SYSTEM.
18. APPROXIMATE LOCATION OF EXISTING ELECTRONIC LOCK AND CARD READER TO REMAIN. CONNECT TO NEW MOTION DETECTOR ADJACENT TO DOOR TO MAINTAIN EXISTING SECURITY SETUP. TYPICAL.

SYSTEM OUTPUTS	SYSTEM INPUTS							
	A	B	C	D	E	F	G	H
REPORT TO FIRE ALARM STATION	•	•	•	•	•	•	•	•
SIGNAL SUPERVISING STATION	•	•	•	•	•	•	•	•
ACTIVATE AUDIBLE NOTIFICATION	•	•	•	•	•	•	•	•
RELEASE ASSOCIATED DOOR HOLDERS	•	•	•	•	•	•	•	•
INITIATE ELEVATOR RECALL	•	•	•	•	•	•	•	•
CLOSE ASSOCIATED SMOKE DAMPER	•	•	•	•	•	•	•	•
SHUT-DOWN ASSOCIATED HANDLING EQUIPMENT	•	•	•	•	•	•	•	•

NOTE:
SEQUENCE OF OPERATIONS INDICATED IS SCHEMATIC.
MODIFY TO SUIT CONDITIONS AND MEET APPLICABLE
CODE REQUIREMENTS.

3 SEQUENCE OF OPERATIONS NOT TO SCALE

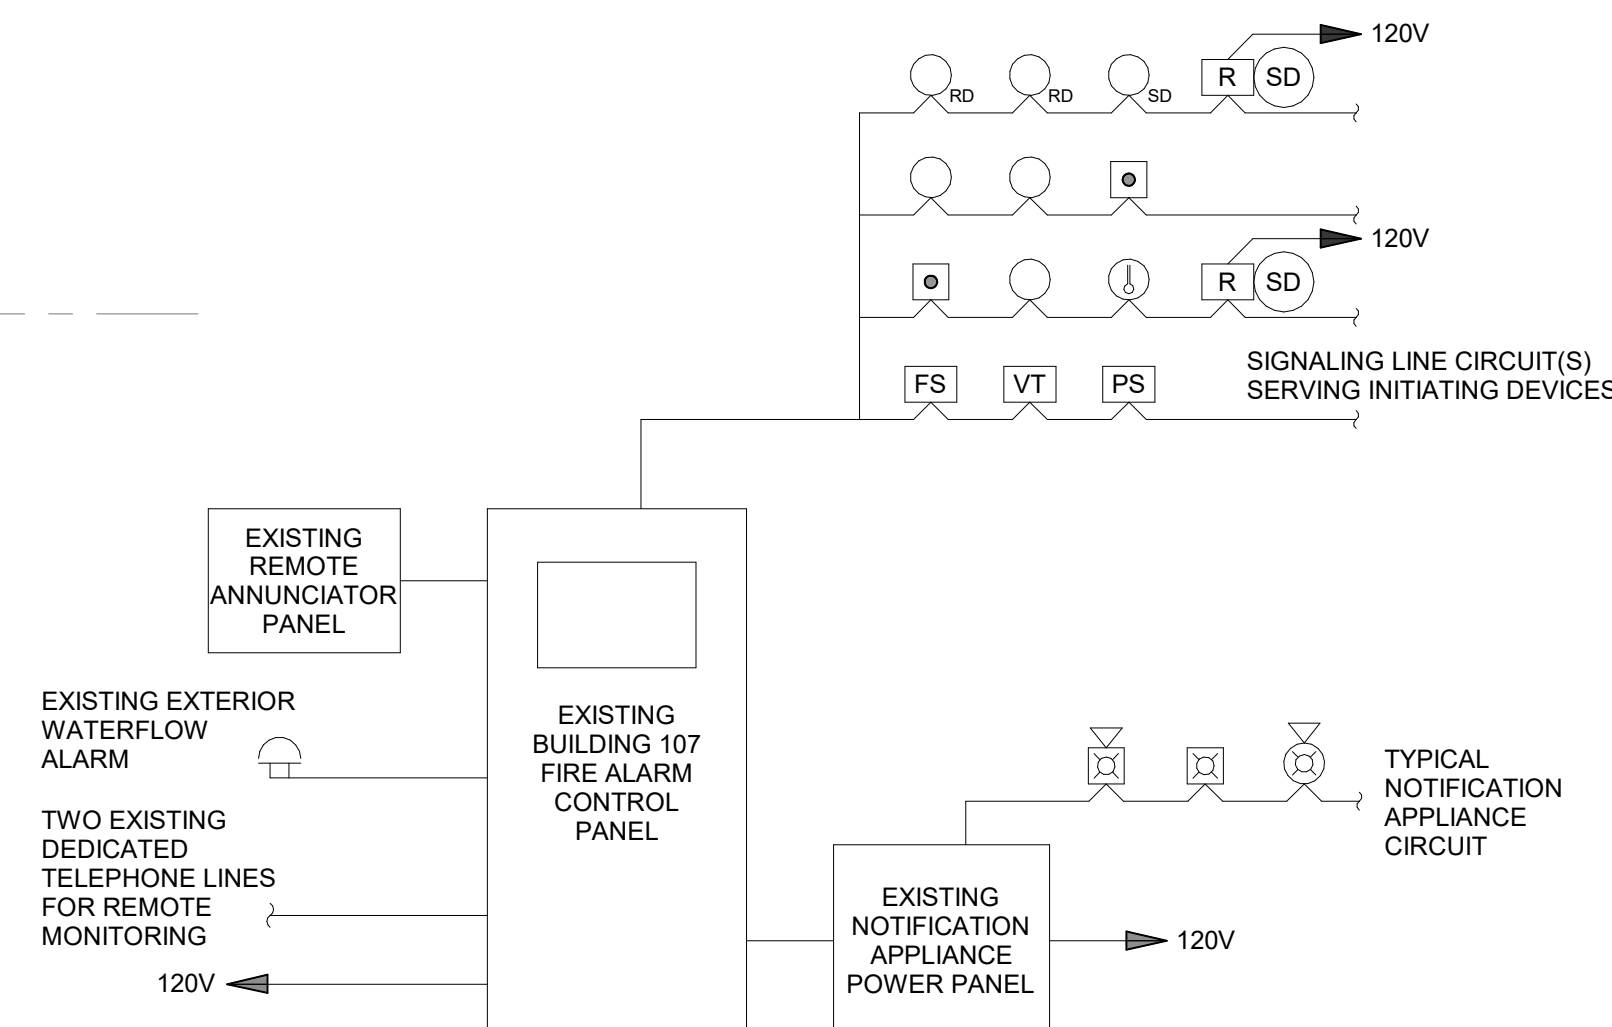

NOTES:
RISER DIAGRAM IS SCHEMATIC IN NATURE. NOT ALL DEVICES ARE SHOWN.
REFER TO PLANS FOR EQUIPMENT QUANTITIES AND LOCATIONS.
REFER TO PLANS AND SPECIFICATIONS FOR ADDITIONAL INFORMATION.

2 ADDRESSABLE, NON-VOICE FIRE ALARM SYSTEM RISER DIAGRAM NOT TO SCALE


FULLY SPRINKLERED
100% DESIGN

Veterans
Benefits
Administration



No.	REVISION DESCRIPTION	DATE

ARCHITECT / ENGINEER:

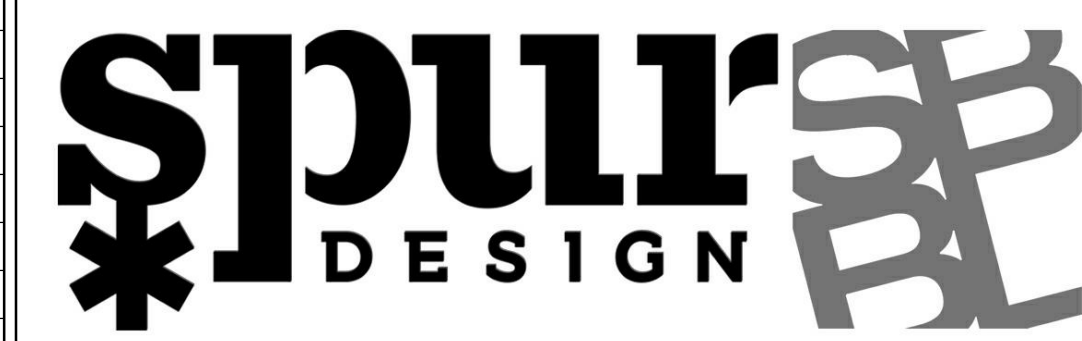

SPUR SBBL COLLABORATIVE JV, INC
100 N. STONE AVENUE, STE 1102
TUCSON, AZ 85701
(405) 842-6100

IL ARCH REG. NO. 001023503, EXP. 11/30/2022
IL ENGR REG. NO. 062.071715, EXP. 11/30/2021

MECH / ELEC / PLUMB / TECH ENGINEER
SPUR DESIGN
11020 KING STREET, SUITE 350
OVERLAND PARK, KS 66210
(405) 842-6100

STAMP:



Drawing Title
**LEVEL 2 - ELECTRICAL DATA AND
SECURITY PLAN**

VA Health Care System Approval:

Project Title
HINES FINANCE CENTER

Location
STATION 201, BLDG 215, STE 200X
1ST AVENUE NORTH 22ND STREET
HINES, IL 60141

Date
06/14/2021

Checked
BN

Drawn
BP

Project Number
201VB3032

Drawing Number
EP-103

Drawing # 26 OF 29

6/16/2021 12:05:35 PM

VA FORM 08-6231

NOTES: NEW FIXTURES WALL CONTROLS AND SENSORS TO TIE INTO THE EXISTING LUTRON QUANTUM SYSTEM. LUTRON SOFTWARE UPDATE MAY BE REQUIRED TO SUPPORT THE NEW HARDWARE INSTALLED.												
TYPE	BASIS OF DESIGN: MANUFACTURER AND MODEL	MOUNTING	LAMP			BALLAST/DRIVER				DESCRIPTION	NOTE	
			TYPE	LUMENS	COLOR TEMP	TYPE	VOLTAG E	INPUT WATTS	INPUT VA			
B1	WILLIAMS AT3 SERIES: AT3-2 24-30/840-D-CP-LDE1-UNV	LAY-IN GRID CEILING	INTEGRAL WHITE LED	3000 lm	4000 K	STANDARD ELECTRONIC LED DRIVER	277 V	29 W	32 VA	2'X2' LAY-IN LED TROFFER, DIRECT/INDIRECT LUMINAIRE WITH METAL PERFORATED BASKET, 80CRI, IC RATED, PAINT AFTER FABRICATION		
B1E	WILLIAMS AT3 SERIES: AT3-2 24-30/840-D-EM10W-CP-LDE1-UNV	LAY-IN GRID CEILING	INTEGRAL WHITE LED	3000 lm	4000 K	STANDARD ELECTRONIC LED DRIVER	277 V	29 W	32 VA	SAME AS TYPE 'B1', EXCEPT PROVIDED WITH 90-MINUTE BATTERY BACKUP.		
CV	WILLIAMS CX SERIES: CX-CX-CC-L840-25-D-LDE1-UNV	COVE MOUNTED	INTEGRAL WHITE LED	2400 lm	4000 K	DIMMING ELECTRONIC LED DRIVER	277 V	14 W	17 VA	CONTINUOUS COVE LIGHT. COORDINATE EXACT LOCATION AND LENGTH OF FIXTURE TO PROVIDE CONTINUOUS RUNS. 4' LENGTH SHOWN FOR LOAD CALCULATION ONLY.		
D1	WILLIAMS 6DS SERIES: 6DS-L20/840-CP-DIMLDE1-UNV-RW-OF-WH-MWT-N1	GYP. BOARD CEILING	INTEGRAL WHITE LED	2000 lm	4000 K	STANDARD ELECTRONIC LED DRIVER	277 V	23 W	26 VA	6" SQUARE LED ADJUSTABLE DOWNLIGHT.		
D1E	WILLIAMS 6DS SERIES: 6DS-L20/840-CP-EM10W-DIMLDE1-UNV-RW-OF-WH-MWT-N1	LAY-IN GRID/ GYP. BOARD CEILING	INTEGRAL WHITE LED	2000 lm	4000 K	STANDARD ELECTRONIC LED DRIVER	277 V	23 W	26 VA	SAME AS TYPE 'D1', EXCEPT PROVIDED WITH 90-MINUTE BATTERY BACKUP.		
D2	WILLIAMS 2AS SERIES: 2AS-L7840-CP-VRF/DBLDE1-UNV-FN-ZF-WH-PD-N1	GYP. BOARD CEILING	INTEGRAL WHITE LED	2000 lm	4000 K	STANDARD ELECTRONIC LED DRIVER	277 V	11 W	12 VA	6" SQUARE LED ADJUSTABLE DOWNLIGHT.		
U4	WILLIAMS 1SF 4x24/835-AF12125-WHITE-DRV-UNV	UNDERCABINET	INTEGRAL WHITE LED	2400 lm	4000 K	STANDARD ELECTRONIC LED DRIVER	277 V	21 W	23 VA	4' UNDERCABINET LED LIGHT FIXTURE. SURFACE MOUNT UNDERCABINET OUT OF VIEW.		
X1E	WILLIAMS EXIT/CA SERIES: EXIT/CA-R-AF-BA-EM-SOT	UNIVERSAL TOP/END MOUNT	LED	0 lm	0 K	STANDARD EXIT SIGN LED DRIVER	277 V	4 W	4 VA	UNIVERSAL MOUNT. SINGLE/DOUBLE FACE EXIT SIGN WITH RED LETTERING BRUSHED ALUMINUM HOUSING. SELF DIAGNOSTICS AND CONNECTED TO LIFE SAFETY BRANCH CIRCUIT.		



OCCUPANCY SENSOR AND SWITCH SCHEDULE						
SYMBOL TYPE	BASIS OF DESIGN: MANUFACTURER AND MODEL	VOLTAGE	COVERAGE	ON MODE	TIME DELAY	DESCRIPTION
Ⓟ _{VS}	WATTSTOPPER: LMD-100-W	24V DC INPUT	MINIMUM 28°, 360 DEGREE RADIAL COVERAGE AT 9' MOUNTING HEIGHT	MANUAL	20 MINUTES	CEILING MOUNTED, DUAL TECHNOLOGY DIGITAL OCCUPANCY SENSOR COMPATIBLE WITH DIGITAL ROOM CONTROLLER WITH CATSE NETWORKING.
Ⓟ _{OS}	WATTSTOPPER: LMD-100-W	24V DC INPUT	MINIMUM 28°, 360 DEGREE RADIAL COVERAGE AT 9' MOUNTING HEIGHT	AUTO	20 MINUTES	CEILING MOUNTED, DUAL TECHNOLOGY DIGITAL OCCUPANCY SENSOR COMPATIBLE WITH DIGITAL ROOM CONTROLLER WITH CATSE NETWORKING.
L _V S	WATTSTOPPER: LMSW-101-W	24V DC INPUT	N/A	MANUAL	N/A	LOW VOLTAGE, 1-BUTTON DIGITAL LIGHT SWITCH COMPATIBLE WITH DIGITAL ROOM CONTROLLER WITH CATSE NETWORKING.
OS S	WATTSTOPPER: DW-100-W	120/277V	N/A	AUTO	10 MINUTES	LINE VOLTAGE, 1-BUTTON DUAL TECHNOLOGY OCCUPANCY SENSING LIGHT SWITCH.
L _V S	WATTSTOPPER: LMDM-110-W	24V DC INPUT	N/A	MANUAL	N/A	LOW VOLTAGE, 1-BUTTON, DIMMING, DIGITAL LIGHT SWITCH COMPATIBLE WITH DIGITAL ROOM CONTROLLER WITH CATSE NETWORKING.
VSD S	WATTSTOPPER: DW-311-W	120/277V	N/A	MANUAL	10 MINUTES	LINE VOLTAGE, 2-BUTTON, 0-10V DIMMING, DUAL TECHNOLOGY OCCUPANCY SENSING, LIGHT SWITCH
PP ₁	WATTSTOPPER: LMR-211	120/277V	N/A	N/A	N/A	1 RELAY DIGITAL ROOM CONTROLLER, 0-10V DIMMING, COMPATIBLE WITH CATSE NETWORK DEVICES
PP ₂	WATTSTOPPER: LMR-212	120/277V	N/A	N/A	N/A	2 RELAY DIGITAL ROOM CONTROLLER, 0-10V DIMMING, COMPATIBLE WITH CATSE NETWORK DEVICES

GENERAL NOTES:

- SENSOR LAYOUT BASED ON COVERAGE PATTERNS OF MANUFACTURERS INDICATED ABOVE. ADJUSTS QUANTITIES AND LOCATIONS FOR ALTERNATE MANUFACTURERS.
- PROVIDE ALL SENSORS FROM SAME MANUFACTURER.
- VERIFY COLOR(S) FOR WALL SWITCHES WITH ARCHITECT.
- ALL SENSORS SHALL HAVE AN ADJUSTABLE TIME DELAY RANGE OF 30 SECONDS TO 30 MINUTES, UNLESS NOTED OTHERWISE.
- DO NOT INSTALL LINE VOLTAGE SENSORS ON GFCI PROTECTED CIRCUITS.

NOTES:

- WALL SWITCH SENSOR REQUIRES NEUTRAL CONDUCTOR FOR OPERATION

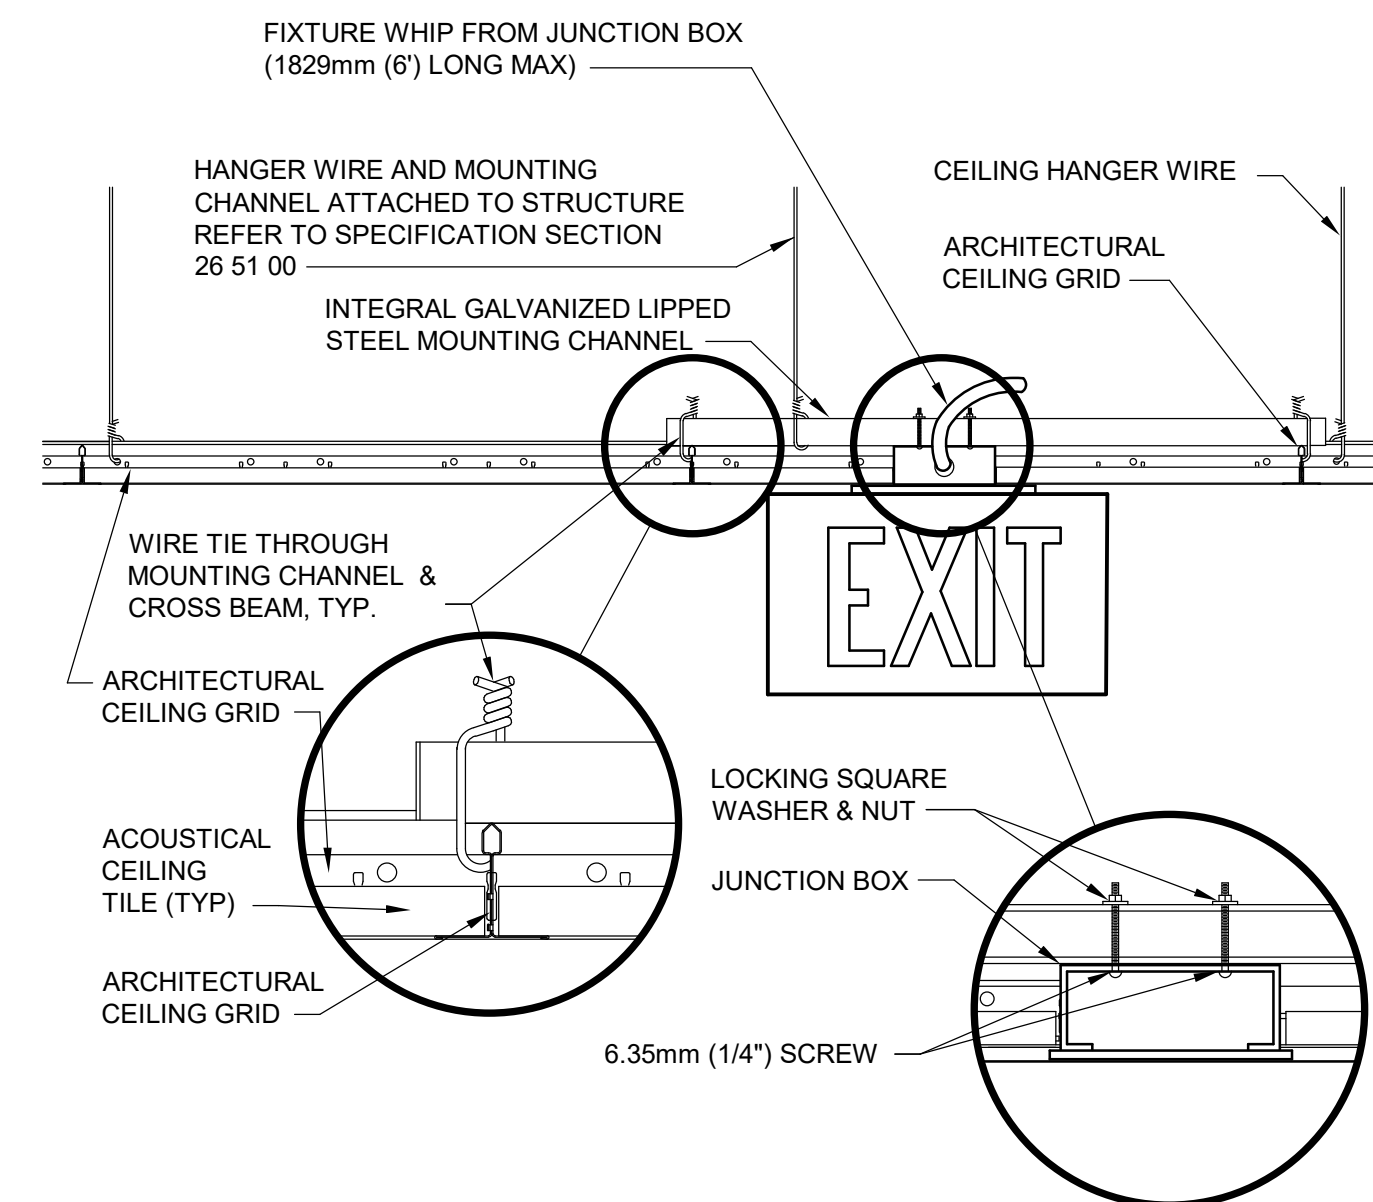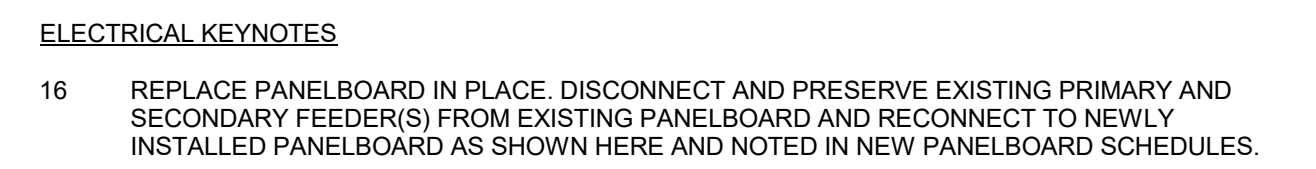


GENERAL NOTE

1. INSTALL IN ACCORDANCE WITH MANUFACTURER'S MOUNTING INSTRUCTIONS AND USING THE RECOMMENDED MOUNTING HARDWARE.


EXIT SIGN MOUNTING - LAY-IN CEILING

NOT TO SCALE

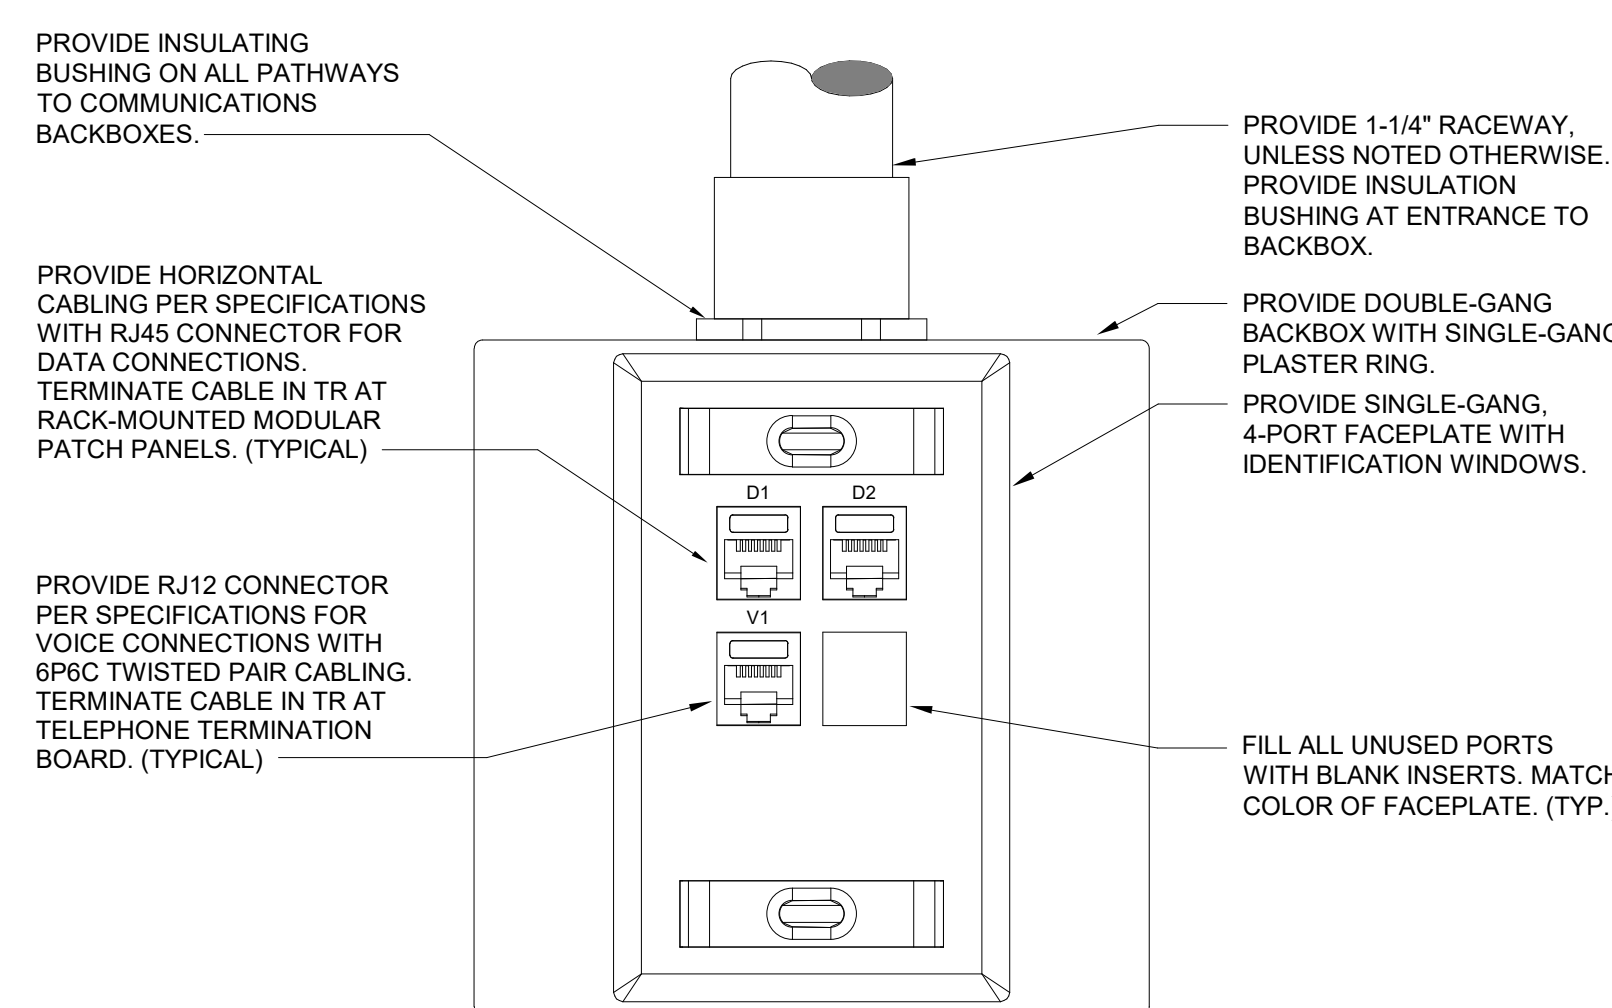

NOTE

NOTE:
PERMANENTLY LABEL ALL WALL JACKS IN THE FOLLOWING MANNER: BUILDING-FLOOR-JACK NUMBER-ROOM NUMBER OF CLOSET. EXAMPLE: 1-1-33-148B (BUILDING 1, FLOOR 1, JACK 33, CLOSET ROOM NUMBER 148B). JACK NUMBER INDICATES THE PUNCH DOWN POSITION OF THE CLOSET CONNECTION. ALL JACKS ON THE SAME PLAT SHALL HAVE THE SAME NUMBER WHERE POSSIBLE. LABEL ALL JACKS IN ACCORDANCE WITH JCM VAMP IRM-70.

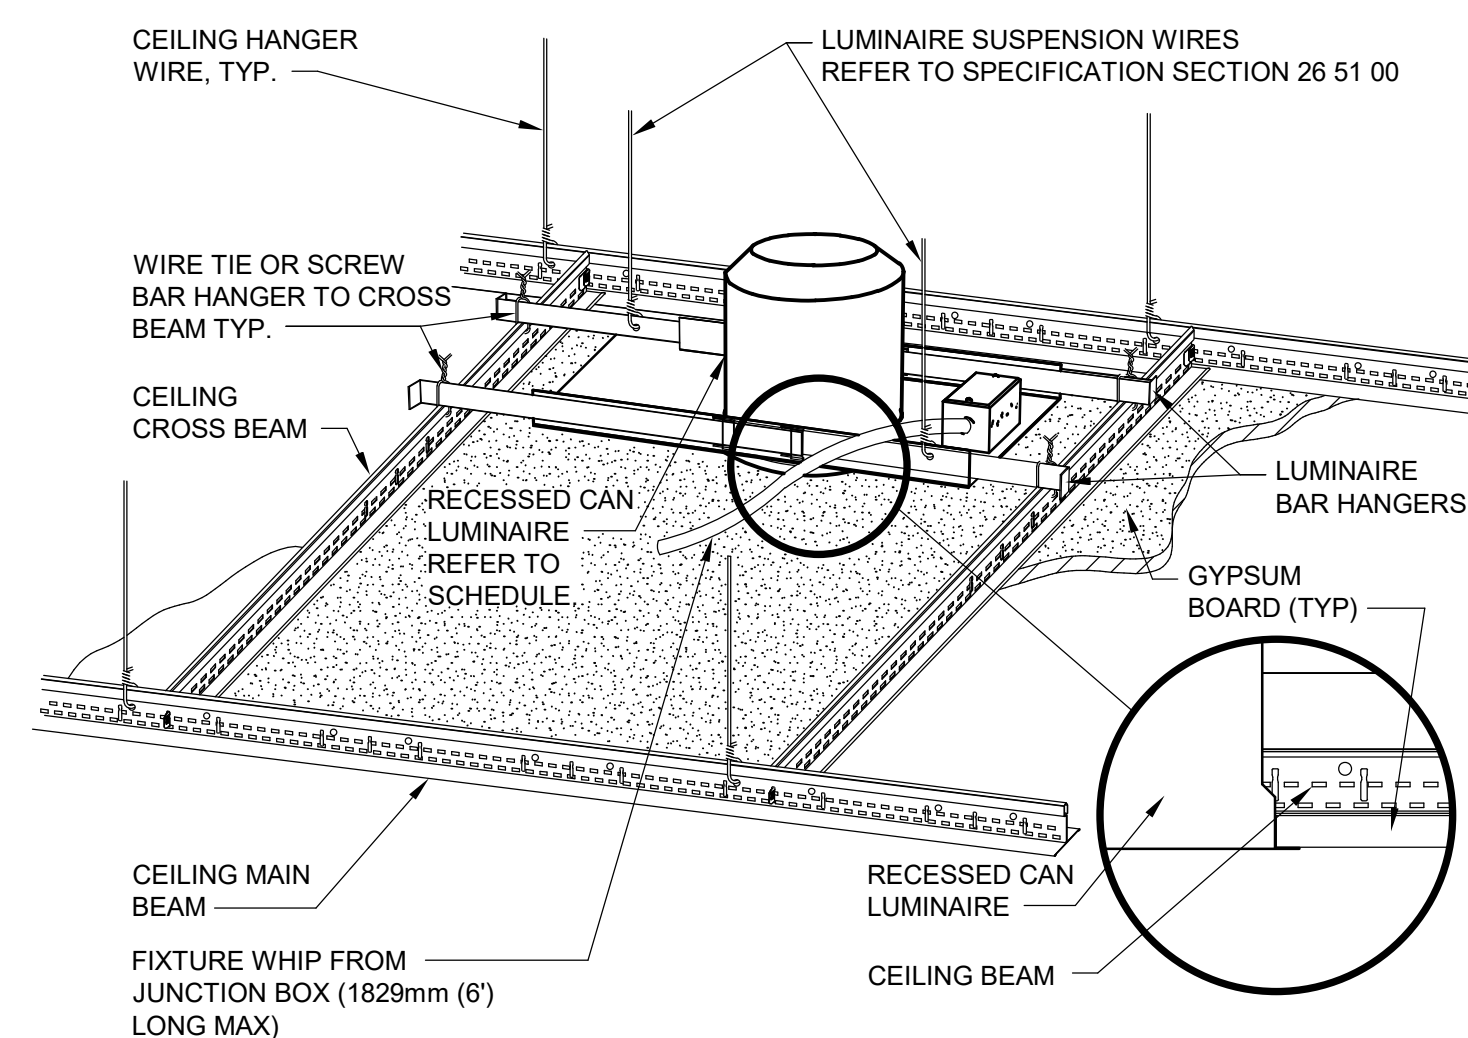


GENERAL NOTE

1. INSTALL IN ACCORDANCE WITH MANUFACTURER'S MOUNTING INSTRUCTIONS AND USING THE RECOMMENDED MOUNTING HARDWARE.

DOWNLIGHT MOUNTING - LAY-IN CEILING

NOT TO SCALE

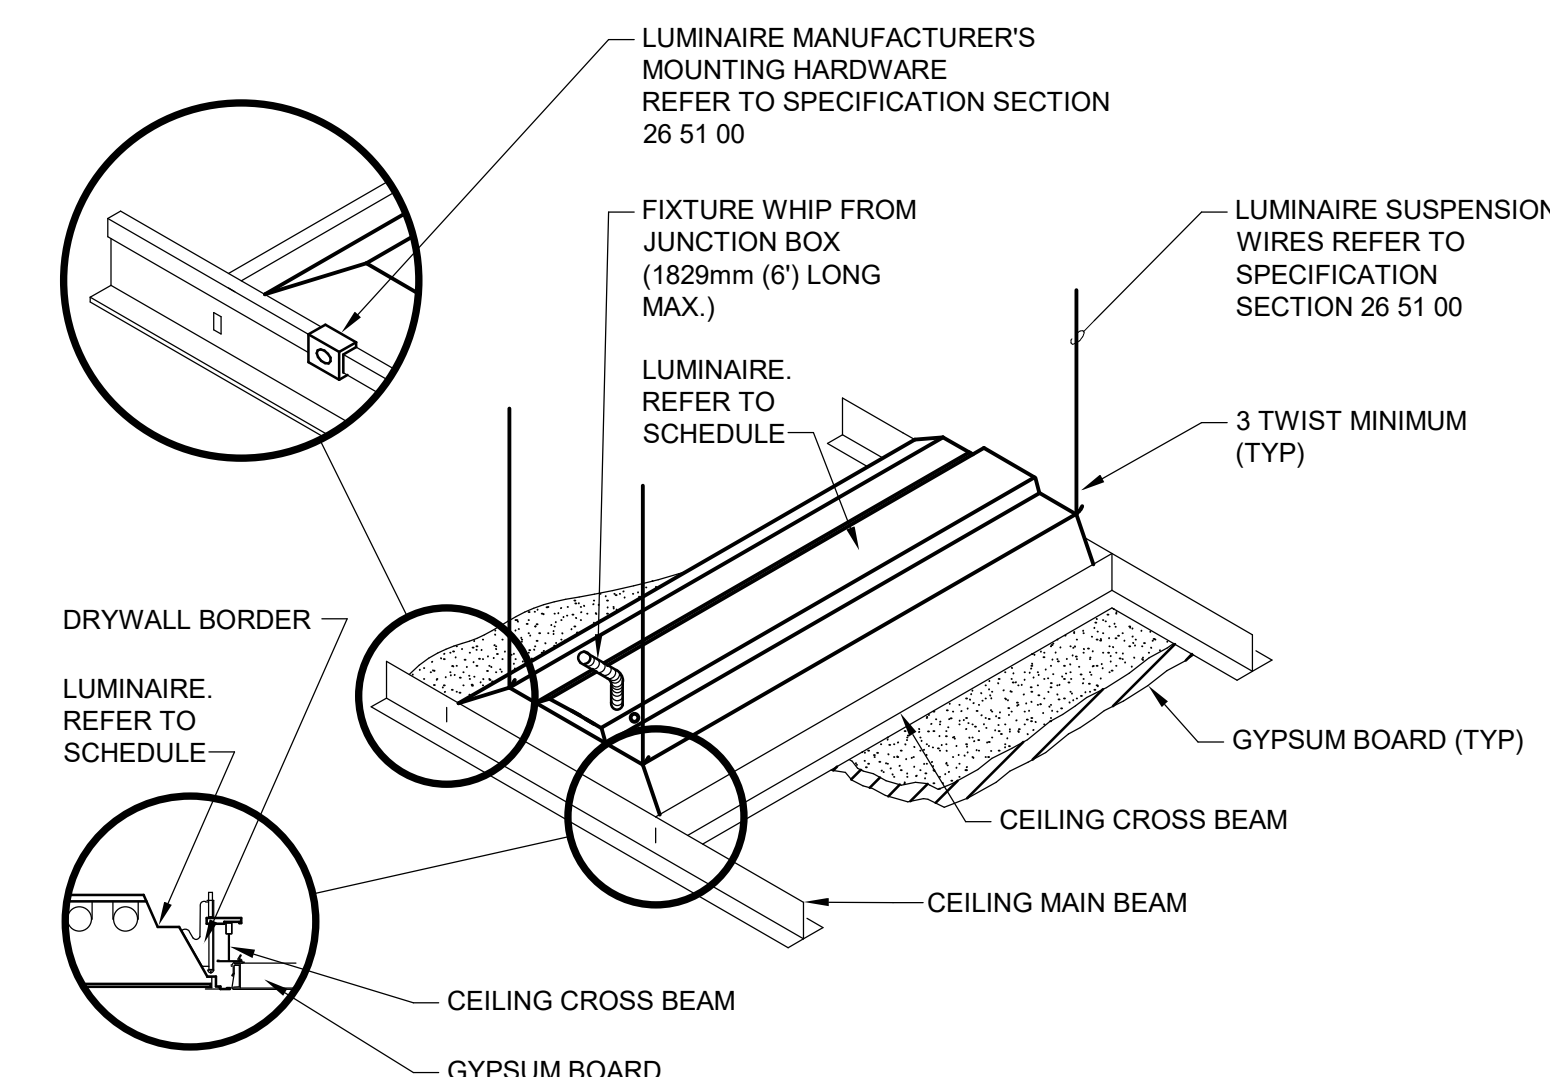


GENERAL NOTE

1. INSTALL IN ACCORDANCE WITH MANUFACTURER'S MOUNTING INSTRUCTIONS AND USING THE RECOMMENDED MOUNTING HARDWARE.

2 LUMINAIRE MOUNTING - LAY-IN CEILING

NOT TO SCALE

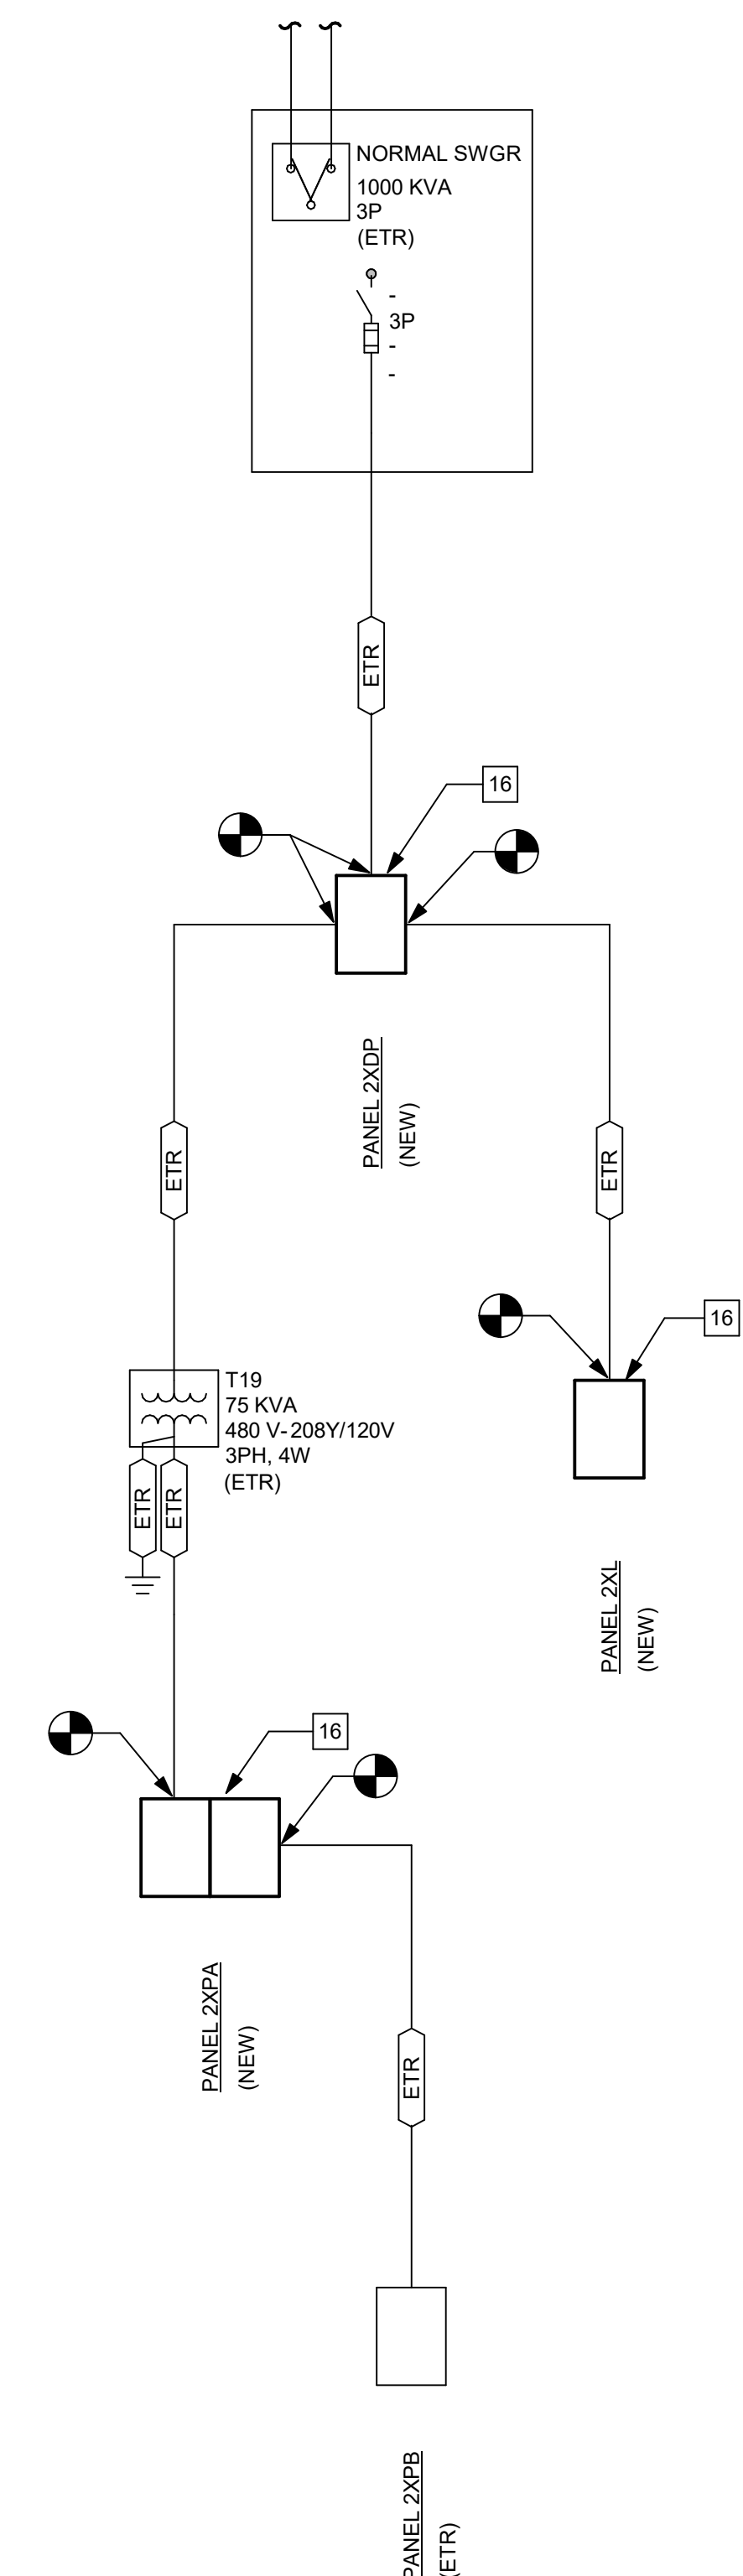

ELECTRICAL ONE-LINE DIAGRAM

NOT TO SCALE

[illegible]

ARCHITECT / ENGINEER:



SPULL
DESIGN


SPUR SBBL COLLABORATIVE JV, INC
100 N. STONE AVENUE, STE 1102
TUCSON, AZ 85701
(405) 842-6100

IL ARCH. LICENSE NO.: 001023503 EXP. 11/30/22
IL MECH. ENGR. LICENSE NO.: 062.071715 EXP. 11/30/22
IL ELECT. ENGR. LICENSE NO.: 062.072296 EXP. 11/30/22

MECH / ELEC / PLUMB / TECH ENGINEER

SPUR DESIGN
11020 KING STREET, SUITE 350
OVERLAND PARK, KS 66210
(405) 842-6100

STAMP:

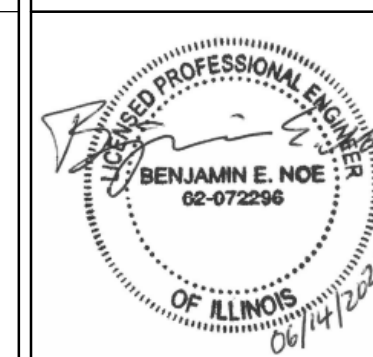

Drawing Title	ELECTRICAL ONE-LINE DIAGRAM AND DETAILS
---------------	--

VA Health Care System Approval:

Project Title	HINES FINANCE CENTER
---------------	-----------------------------

Location	STATION 201, BLDG 215, STE 200X 1ST AVENUE NORTH 22ND STREET HINES, IL 60141
----------	--

Date
06/14/2021

Check	BN
-------	----

Drawn
BP

Project Number	201VB3032
----------------	-----------

Drawing Number

EP-300

Drawing # 27 OF 29

Veterans
Benefits
Administration



PANELBOARD: PANEL 2XPB (ETR)	
BUS SIZE: 100 A					FAULT CURRENT: RE: ONE-LINE DIAGRAM										EQUIPMENT GROUND BUS																											
MAIN SIZE/TYPE: 100 A MCB					LOCATION: Room 200B																																					
VOLTS/PHASE: 208Y/120V, 3PH, 4W					SERVICES:																																					
MOUNTING: SURFACE					FED FROM: PANEL 2XPA (NEW)																																					
A.I.C RATING: EXISTING	
SECTIONS: 1	
VOLT-AMPS/PHASE	
CKT NO.	DESCRIPTION	LOAD TYPE	NOTE	WIRE SIZE	GND SIZE	BRKR AMP	P	A	B	C	A	B	C	P	BRKR AMP	GND SIZE	WIRE SIZE	NOTE	LOAD TYPE	DESCRIPTION	CKT NO.																					
1	COLUMN RECPT	--	--	--	--	20	1	0							1	20	--	--	--	WALL RECPT	2																					
3	COLUMN RECPT	--	--	--	--	20	1		0				0		1	20	--	--	--	WALL RECPT	4																					
5	COLUMN RECPT	--	--	--	--	20	1			0				0	1	20	--	--	--	WALL RECPT	6																					
7	SPARE	--	--	--	--	20	1	0							1	20	--	--	--	N WALL RECPT	8																					
9	SPARE	--	--	--	--	20	1		0						1	20	--	--	--	N WALL RECPT	10																					
11	DESKS MIDDLE	--	--	--	--	20	1			0				0	1	20	--	--	--	SPARE	12																					
13	DESKS MIDDLE	--	--	--	--	20	1	0							1	20	--	--	--	SPARE	14																					
15	SPARE	--	--	--	--	20	1		0					0	1	20	--	--	--	SPARE	16																					
17	SPARE	--	--	--	--	20	1							0	1	20	--	--	--	SPARE	18																					
19	UNDRFLR RECPT	--	--	--	--	20	1	0					0		1	20	--	--	--	SPARE	20																					
21	UNDRFLR RECPT	--	--	--	--	20	1		0					0	1	20	--	--	--	SPARE	22																					
23	UNDRFLR RECPT	--	--	--	--	20	1			0					1	20	--	--	--	SPARE	24																					
25	SPARE	--	--	--	--	20	1	0					0		1	20	--	--	--	SPARE	26																					
27	SPARE	--	--	--	--	20	1		0					0	1	20	--	--	--	SPARE	28																					
29	SPARE	--	--	--	--	20	1			0				0	1	20	--	--	--	SPARE	30																					
31																					32																					
33																					34																					
35																					36																					
37																					38																					
39																					40																					
41																					42																					
								PHASE A					PHASE B					PHASE C																								
								TOTAL PHASE LOAD (VA)					0 VA					0 VA					0 VA																			
								TOTAL PHASE LOAD (A)					0 A					0 A																								
LOAD TYPE	CONNECTED LOAD	NEC DEMAND	DEMAND LOAD																																							
EXISTING LOAD (E):	0 VA	125.00%	0 VA																																							
COOLING (C):	0 VA	0.00%	0 VA																																							
HEATING (H):	0 VA	0.00%	0 VA																																							
LIGHTING (L):	0 VA	125.00%	0 VA																																							
RECEPTACLES (R):	0 VA	100.00%	0 VA																																							
MOTORS (M):	0 VA	100.00%	0 VA																																							
LARGEST MOTOR (X):	0 VA	125.00%	0 VA																																							
SUPPLEMENTAL HEAT (Y):	0 VA	100.00%	0 VA																																							
MISC. EQUIPMENT (Z):	0 VA	100.00%	0 VA																																							
KITCHEN (K):	0 VA	100.00%	0 VA																																							
								PHASE A					PHASE B					PHASE C																								
								TOTAL PHASE LOAD (VA)					0 VA					0 VA					0 VA																			
								TOTAL PHASE LOAD (A)					0 A					0 A																								
								TOTAL CONNECTED					0 VA					0 VA																								
								TOTAL DEMAND					0 VA					0 A																								
								TOTALS:					0 A					0 A																								
								NOTES:																																		
								A. THE UPSTREAM FEEDER CONNECTION FOR THIS PANELBOARD IN PANEL 2XPA WILL BE DISCONNECTED, PRESERVED, AND RECONNECTED TO THE FUTURE NEW PANEL 2XPA. SERVICE TO THIS PANEL WILL BE TEMPORARILY DISCONNECT. ALL PLANNED OUTAGES NEED TO BE REPORTED AND COORDINATED WITH COR TWO WEEKS PRIOR TO OUTAGE.																																		

PANELBOARD: PANEL 2XDP (ETD)																								
BUS SIZE: 400 A					FAULT CURRENT: RE: ONE-LINE DIAGRAM										EQUIPMENT GROUND BUS									
MAIN SIZE/TYPE: 100 A MCB					LOCATION: Room 200K																			
VOLTS/PHASE: 480Y/277V, 3PH, 4W					SERVES:																			
MOUNTING: SURFACE					FED FROM:																			
A.I.C RATING: EXISTING																								
SECTIONS: 1																								
VOLT-AMPS/PHASE																								
CKT NO.	DESCRIPTION	LOAD TYPE	NOTE	WIRE SIZE	GND SIZE	BRKR AMP	P	A	B	C	A	B	C	P	BRKR AMP	GND SIZE	WIRE SIZE	NOTE	LOAD TYPE	DESCRIPTION	CKT NO.			
3	HP B16*, A5*, C18*	--	--	--	--	20	1	0		0				3	20	--	--	--	--	STAIRWELL HEATER	2			
3	HP B15*, A22*	--	--	--	--	20	1	0		0				3							4			
5	HP B3*, C15*, B6*	--	--	--	--	20	1			0				0	3						6			
7	HP B21	--	--	--	--	20	1	0		0		0		0							8			
9	HP C9, F20	--	--	--	--	20	1								3	20	--	--	--	HP F19, F20	10			
11	HP C3, A34, B11	--	--	--	--	20	1			0		0		0							12			
13								0			0		0								14			
15	HP E7	--	--	--	--	20	3								3	20	--	--	--	HP F17, E1	16			
19								0		0		0									18			
21	HP E8*, F16	--	--	--	--	20	3			0		0		0	3				--	MISC EXHAUST FANS	22			
23								0							0						24			
25								0							3						26			
27	HP XX, F15*	--	--	--	--	20	3			0		0		0	3			--	--	HP F14*, F13*	28			
29								0							0						30			
31								0							3	80	--	--	--	ACCUS, AH3, LIGHTS	32			
33	HP C21	--	--	--	--	80	3			0		0		0	3						34			
35								0													36			
37								0							3	150	--	--	--	ACCU2	38			
39	TRANSFORMER T19	--	--	--	--	125	3			0				0							40			
41								0						0							42			
								PHASE A			PHASE B			PHASE C										
TOTAL PHASE LOAD (VA)								0 VA			0 VA			0 VA										
TOTAL PHASE LOAD (A):								0 A			0 A			0 A										
LOAD TYPE		CONNECTED LOAD		NEC DEMAND		DEMAND LOAD								TOTAL CONNECTED		TOTAL DEMAND								
EXISTING LOAD (E):		0 VA		125.00%		0 VA								0 VA		0 VA								
COOLING (C):		0 VA		0.00%		0 VA								0 VA		0 VA								
HEATING (H):		0 VA		0.00%		0 VA								0 VA		0 VA								
LIGHTING (L):		0 VA		125.00%		0 VA								0 VA		0 VA								
RECEPTACLES (R):		0 VA		100.00%		0 VA								0 VA		0 VA								
MOTORS (M):		0 VA		100.00%		0 VA								0 VA		0 VA								
LARGEST MOTOR (X):		0 VA		125.00%		0 VA								0 VA		0 VA								
SUPPLEMENTAL HEAT (Y):		0 VA		100.00%		0 VA								0 VA		0 VA								
MISC. EQUIPMENT (Z):		0 VA		100.00%		0 VA								0 VA		0 VA								
KITCHEN (K):		0 VA		100.00%		0 VA								0 VA		0 VA								
NOTES:																								
A. CONTRACTOR TO REPLACE THIS PANELBOARD IN PLACE.																								
B. CONTRACTOR TO DISCONNECT AND DEMOLISH ALL CIRCUITS FOR EQUIPMENT IN THE AREA OF WORK.																								
C. CONTRACTOR TO DETERMINE EACH BRANCH CIRCUIT THAT FEEDS EQUIPMENT OUTSIDE THE AREA OF WORK AND FOR EQUIPMENT NOT IN THE SCOPE OF WORK. DISCONNECT THESE EXISTING BRANCH CIRCUITS AND PRESERVE FOR RECONNECTION TO THE FUTURE NEW PANELBOARD. CIRCUIT NAMES ARE APPROXIMATE AND BASED ON LIMITED EXISTING INFORMATION. RELOCATED HEAT PUMPS SHALL REMAIN ON THEIR EXISTING CIRCUIT. TRACE AND VERIFY ALL CIRCUITS AND UPDATE PANEL SCHEDULE ACCORDINGLY.																								
* THESE HEAT PUMPS ARE RELOCATED AND RENAMED. SEE NEW PANEL SCHEDULE FOR NEW NAMES AND UPDATE PANEL SCHEDULE AND SERVICE CIRCUITS AS NECESSARY.																								

PANELBOARD: PANEL 2XPA (NEW)																										
BUS SIZE: 225 A						FAULT CURRENT: RE: ONE-LINE DIAGRAM										EQUIPMENT GROUND BUS										
MAIN SIZE/TYPE: 225 A MCB						LOCATION: Room 200K																				
VOLTS/PHASE: 208Y/120V, 3PH, 4W						SERVES: 2ND FLOOR																				
MOUNTING: SURFACE						FED FROM:																				
A.I.C. RATINGS: MATCH EXISTING																										
SECTIONS: 2																										
VOLT-AMPS/PHASE																										
CKT NO	DESCRIPTION	LOAD TYPE	NOTE	WIRE SIZE	GND SIZE	BRKR AMP	P	A	B	C	A	B	C	P	BRKR AMP	GND SIZE	WIRE SIZE	NOTE	LOAD TYPE	DESCRIPTION	CKT NO					
1	FLR BOX / RECEPT (200.02)	R		20	1	1080					1080			1	20					R	FLR BOX / RECEPT (200.04)	2				
3	RECEPT (200.01 / 200A)	R		20	1	1260					1080			1	20					R	RECEPT (200.18/200.05)	4				
5	RECEPT (200.05)	R		20	1						1080			720	1	20				R	RECEPT (200.17 2/200.18)	6				
7	PRINTER RECEPT (200.17.2)	R		20	1	180					180			1	20					R	PRINTER RECEPT (200.17.2)	8				
9	WORKST FLR BOX (200.17)	R		20	1	0					1080			1	20					R	RECEPT (200.16/2006)	10				
11	RECEPT (200C)	R		20	1	1080					1080			1	20					R	FLR BOX / RECEPT (200.16)	12				
13	FLR BOX / RECEPT (200.13)	R		20	1	1260					1260			1	20					R	FLR BOX / RECEPT (200.15)	14				
15	FLR BOX / RECEPT (200.14)	R		20	1	1260					1260			1	20					R	FLR BOX / RECEPT (200.12)	16				
17	RECEPT (200.11)	R		20	1	720					660			1	20					R	RECEPT (200.11)	18				
19	RECEPT (200.11)	R		20	1	1650					1260			1	20					R	FLR BOX / RECEPT (200.10)	20				
21	FLR BOX / RECEPT (200.09)	R		20	1	1260					1260			1	20					R	FLR BOX / RECEPT (200.09)	22				
23	FLR BOX / RECEPT (200.07)	R		20	1	1260					1260			720	1	20				R	WORKST FLR BOX (200.16)	24				
25	FLR BOX / RECEPT (200.03)	R		20	1	1260					720			1	20					R	WORKST FLR BOX (200.16)	26				
27	WORKST FLR BOX (200.16)	R		20	1	1440					1440			1440	1	20				R	WORKST FLR BOX (200.16)	28				
29	WORKST FLR BOX (200.16)	R		20	1	1440					1440			1440	1	20				R	WORKST FLR BOX (200.17)	30				
31	WORKST FLR BOX (200.17)	R		20	1	1440					1620			1	20					R	CONF TABLE FLR BOX (200.05)	34				
35	WORKST FLR BOX (200.17)	R		20	1					0				1260	1	20				R	RECEPT (200.04)	36				
37	PRINTER RECEPT (200.16)	R		20	1	180				0	0			1	20							38				
39	SPARE	--	--	20	1	0				0				3	100					PANEL 2XPB (ETR)		40				
41	SPARE	--	--	20	1	0				0												42				
43	SPARE	--	--	20	1	0				0				1	20	--	--	--	--	SPARE		44				
45	SPARE	--	--	20	1	0				0				1	20	--	--	--	--	SPARE		46				
47	SPARE	--	--	20	1	0				0				0	1	20	--	--	--	SPARE		48				
49	SPARE	--	--	20	1	0				0				1	20	--	--	--	--	SPARE		50				
51	SPARE	--	--	20	1	0				0				1	20	--	--	--	--	SPARE		52				
53	SPARE	--	--	20	1	0				0				0	1	20	--	--	--	SPARE		54				
55	SPARE	--	--	20	1	0				0				0	1	20	--	--	--	SPARE		56				
57	SPARE	--	--	20	1	0				0				0	1	20	--	--	--	SPARE		58				
59	SPARE	--	--	20	1	0				0				0	1	20	--	--	--	SPARE		60				
61	SPARE	--	--	20	1	0				0				1	20	--	--	--	--	SPARE		62				
63	SPARE	--	--	20	1	0				0				1	20	--	--	--	--	SPARE		64				
65	SPARE	--	--	20	1	0				0				20	0	--	--	--	--	SPARE		66				
67	SPARE	--	--	20	1	0				0				1	20	--	--	--	--	SPARE		68				
69	SPARE	--	--	20	1	0				0				1	20	--	--	--	--	SPARE		70				
71	SPARE	--	--	20	1	0				0				0	1	20	--	--	--	SPARE		72				
73	SPARE	--	--	20	1	0				0				0	1	20	--	--	--	SPARE		74				
75	SPARE	--	--	20	1	0				0				1	20	--	--	--	--	SPARE		76				
77	SPARE	--	--	20	1	0				0				0	1	20	--	--	--	SPARE		78				
79	SPARE	--	--	20	1	0				0				1	20	--	--	--	--	SPARE		80				
81	SPARE	--	--	20	1	0				0				0	1	20	--	--	--	SPARE		82				
83	SPARE	--	--	20	1	0				0				0	1	20	--	--	--	SPARE		84				
						PHASE A		PHASE B		PHASE C																
						TOTAL PHASE LOAD (VA)		13890 VA		14400 VA																
						TOTAL PHASE LOAD (A):		119 A		123 A																
LOAD TYPE	CONNECTED LOAD	NEC DEMAND	DEMAND LOAD					PANELBOARD				TOTALS:				TOTAL CONNECTED				TOTAL DEMAND						
EXISTING LOAD (E):	0 VA	125.00%	0 VA									39750 VA				24875 VA										
COOLING (C):	0 VA	0.00%	0 VA													69 A										
HEATING (H):	0 VA	0.00%	0 VA																							
LIGHTING (L):	0 VA	125.00%	0 VA																							
RECEPTACLES (R):	39750 VA	62.58%	24875 VA																							
MOTORS (M):	0 VA	100.00%	0 VA																							
LARGEST MOTOR (X):	0 VA	125.00%	0 VA																							
SUPPLEMENTAL HEAT (Y):	0 VA	100.00%	0 VA																							
MISC. EQUIPMENT (Z):	0 VA	100.00%	0 VA																							
KITCHEN (K):	0 VA	100.00%	0 VA																							
NOTES:																										
A. SUPPLY PANELBOARD WITH FEED THROUGH LUIS8 WITH 4/0 CONNECTION. RECONNECT FEED TO EXISTING PANEL 2XPB LOADS IN ROOM 200B ON THE WEST SIDE OF LEVEL 2.																										
B. ALL BRANCH CIRCUITS WITH LOADS SHOWN ARE NEW.																										
C. NOT SHOWN - BRANCH CIRCUIT LOADS FROM THE PREVIOUS EXISTING PANEL, NOW REPLACED ARE TO BE EVALUATED BY THE CONTRACTOR TO DETERMINE ANY THAT RE LOADS OUTSIDE THE AREA OF WORK. ANY PRESERVED OUTSIDE LOADS SHALL BE RECONNECTED. TRACE CIRCUITS AND PROVIDE AN ACCURATE PANEL SCHEDULE.																										